SHEM

ШИНКЕВИЧ ЕКАТЕРИНА

дизайнер интерьеров

ОБЪЕКТ :	Квартира
МЕСТОРАСПОЛОЖЕНИЕ ОБЪЕКТА :	Адрес
ЗАКАЗЧИК :	Заказчик
ТЕЛЕФОН ЗАКАЗЧИКА :	Телефон
ЧЕРТИЛ :	Шинкевич Екатерина
ТЕЛЕФОН ЧЕРТИЛЫ :	+7 (931) 271-59-56

2026

Листа	Наименование	Примечание
01	Общие данные	
02	План обмеров	
03	План демонтажа	
04	План возводимых перегородок с маркировкой дверных проемов	
05	План после перепланировки	
06	План расстановки мебели	
07	План с мебельными размерами и описанием	
08	План размещения осветительных приборов, привязка выпусков освещения	
09	План выключателей с указанием включения групп светильников	
10	План размещения электрических розеток с привязкой размеров	
11	План потолков и гипсокартонных конструкций	
12	План полов с указанием типа напольных покрытий	
13	План расположения систем отопления и вентиляции	
14	План размещения санитарно-технического оборудования	
15	План отделочных материалов по стенам	
16	Развертки по стенам. Студия	
17	Визуализация	
18	Визуализация	
19	Визуализация	
20	Визуализация	
21	Развертки по стенам. Санузел	
22	Визуализация	
23	Визуализация. Балкон	
24	Мебель на заказ	
25	Спецификация мебели	
26	Спецификация осветительного оборудования	

ПОЯСНИТЕЛЬНАЯ ЗАПИСКА

К дизайн-проекту интерьера квартиры, расположенной по адресу: Адрес
Проект выполнен на основании обмеров. Квартира имеет общую площадь: 28,33 м2

1. Все замеры производились по черновому полу.
2. В проекте за относительную отметку 0,000 принят уровень чистового пола.
3. Опуски потолков минимальны.
4. Выкрасы производить совместо с дизайнером, соблюдая все рекомендации производителя краски. Выбор оттенка ТОЛЬКО после выкрасов.
5. Точная высота стяжки и пирог пола согласовываются по месту.
6. В санузле провести гидроизоляцию пола и всех стен до потолка. Гидроизоляция пола по всей квартире с заходом на стены 100мм.
7. Все размеры заказной мебели уточнить на месте с представителем-изготовителем.
8. Местоположение розеток и техники на кухне согласовать с производителем мебели.
9. Устроить шумоизоляцию шахт.


Проект квартиры полностью удовлетворяет пожеланиям Заказчика.

Необходимо произвести следующие работы:

1. Произвести демонтаж конструкций согласно РП-03;
2. Возвести новые конструкции согласно РП-04;
3. Устроить потолки согласно РП-11;
4. Выполнить электропроводку согласно РП-08, РП-09, РП-10;
5. Полы устроить согласно РП-13 и РП-12;
6. Произвести отделку согласно РП-15, РП-16 – РП-21.

Дизайн-проект квартиры по адресу: Адрес	Заказчик Заказчик	Общие данные	Масштаб	Лист	Листов	чертёжник	Шинкевич Екатерина	SHEM
				01	26	телефон	+7 (931) 271-59-56	

План обмеров

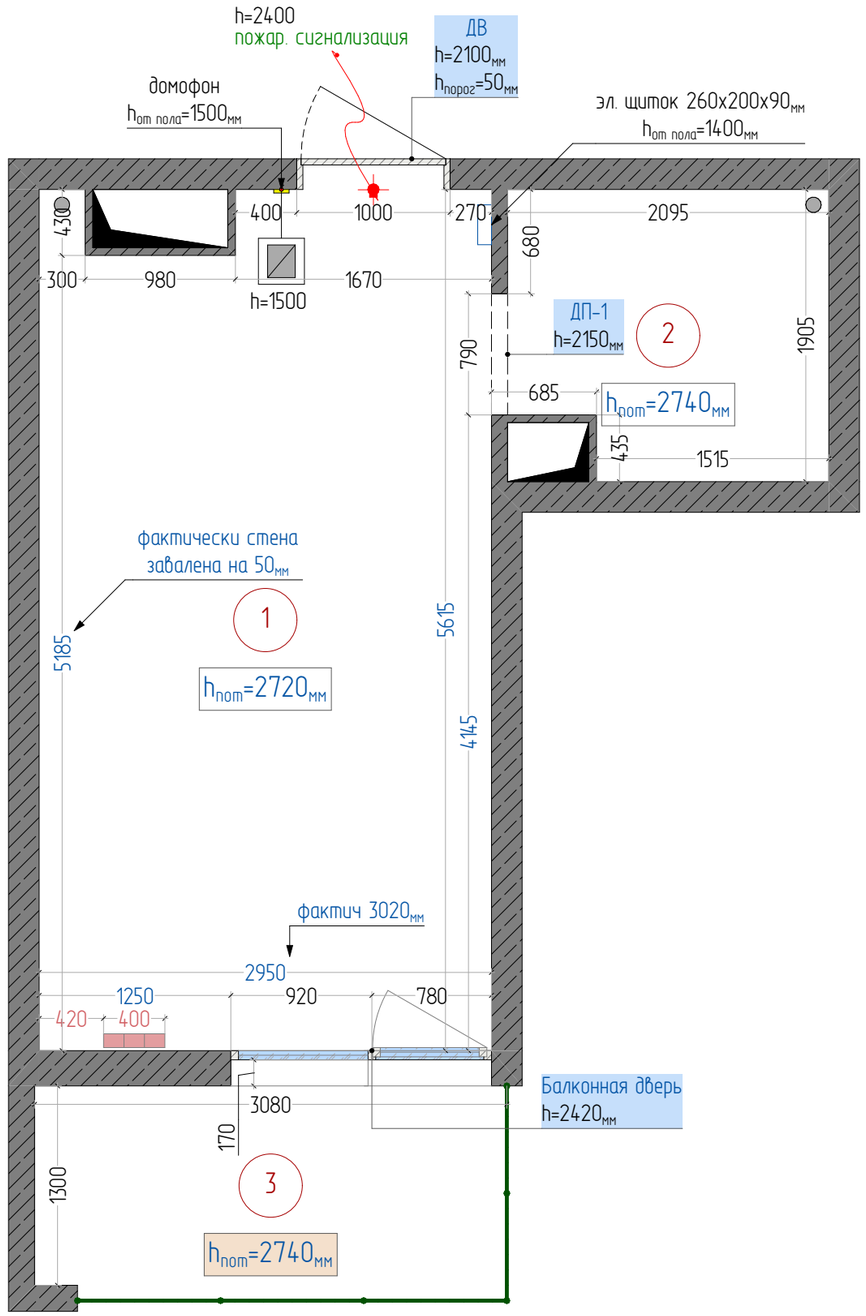


Условные обозначения:

2 – номер помещения

– существующие конструкции

– вентиляционная шахта

– канализационная труба

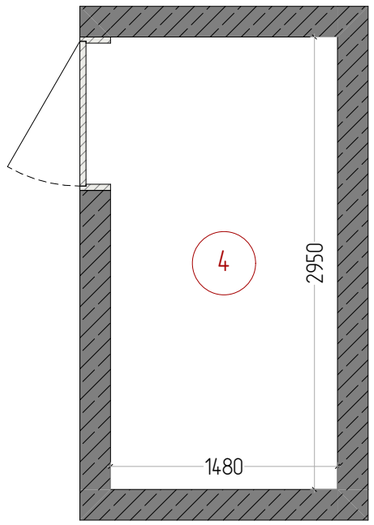


Экспликация помещений на этапе обмеров		
№	Название помещения	Площадь, кв.м
1	Гостиная	16,14
2	Санузел	3,82
3	Балкон	4,00
4	Кладовка	4,37
		28,33 м²

Примечание:

1. Все размеры даны в миллиметрах с учетом округления до 5мм.
2. Обмерный план выполнен на основании обмеров. Погрешность не превышает 30мм.
3. Замеры производились в помещении без отделки.
4. Все размеры и отметки проверить перед началом строительных работ.
5. Несоответствие размеров и отметок согласовать с дизайнером.
6. Площадь помещений посчитана без учёта перегородок и дверных проёмов.

Дизайн-проект квартиры по адресу: Адрес	Заказчик Заказчик	План обмеров	Масштаб 1:40	Лист	Листов	чертёжник	Шинкевич Екатерина	SHEM
				02	26	телефон	+7 (931) 271-59-56	

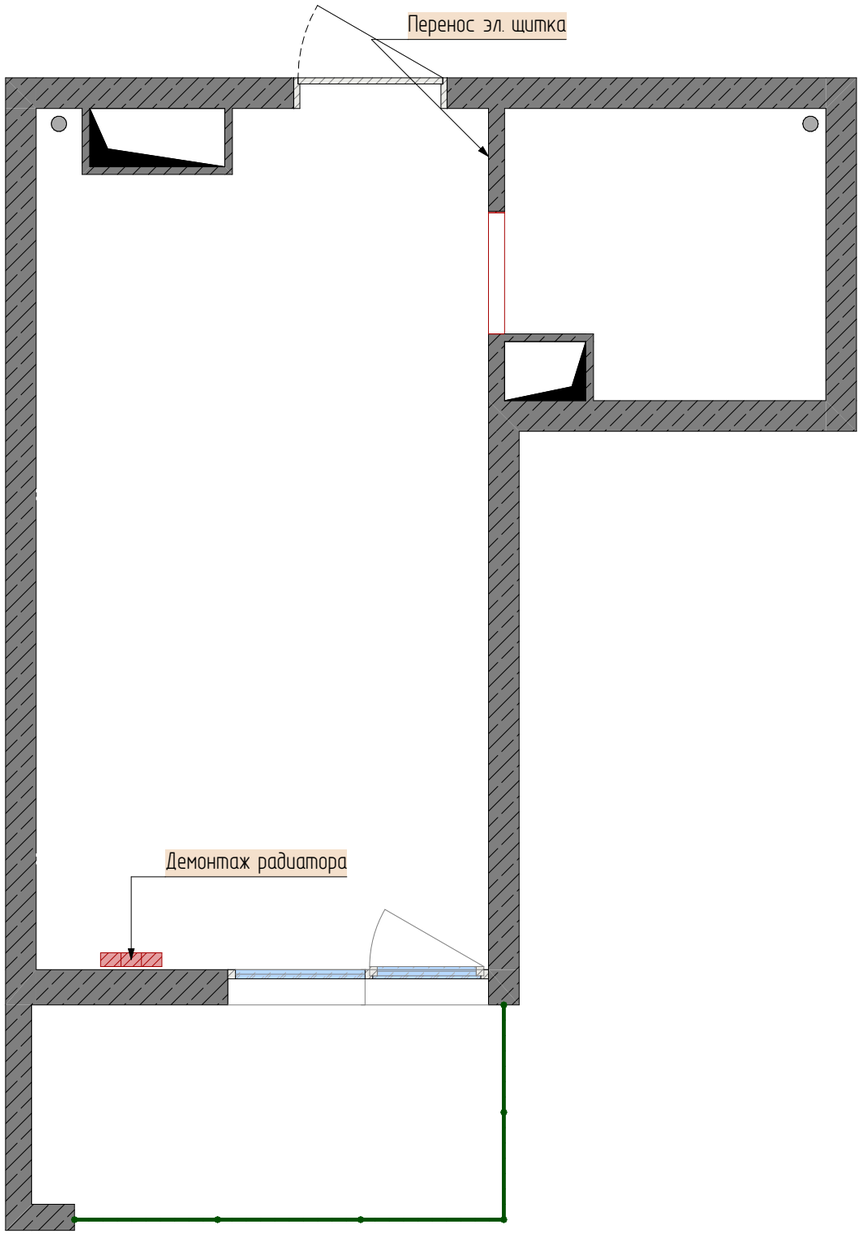

Условные обозначения:

– существующие конструкции


– демонтируемые конструкции

Примечание:

1. Все размеры указаны в миллиметрах с учетом округления до 5мм.
2. Все размеры и отметки проверить по месту перед началом строительных работ.
3. Несоответствие размеров и отметок согласовать с дизайнером.
4. Для работ, затрагивающих несущие конструкции или общедомовые инженерные сети, Заказчик обязан привлечь организацию с допуском СРО. Исполнитель не несет ответственности за последствия реализации таких решений без СРО.

Дизайн-проект квартиры по адресу: Адрес	Заказчик Заказчик	План демонтажа	Масштаб 1:40	Лист 03	Листов 26	чертёжник телефон	Шинкевич Екатерина +7 (931) 271-59-56	SHEM

План возводимых перегородок с маркировкой дверных проемов

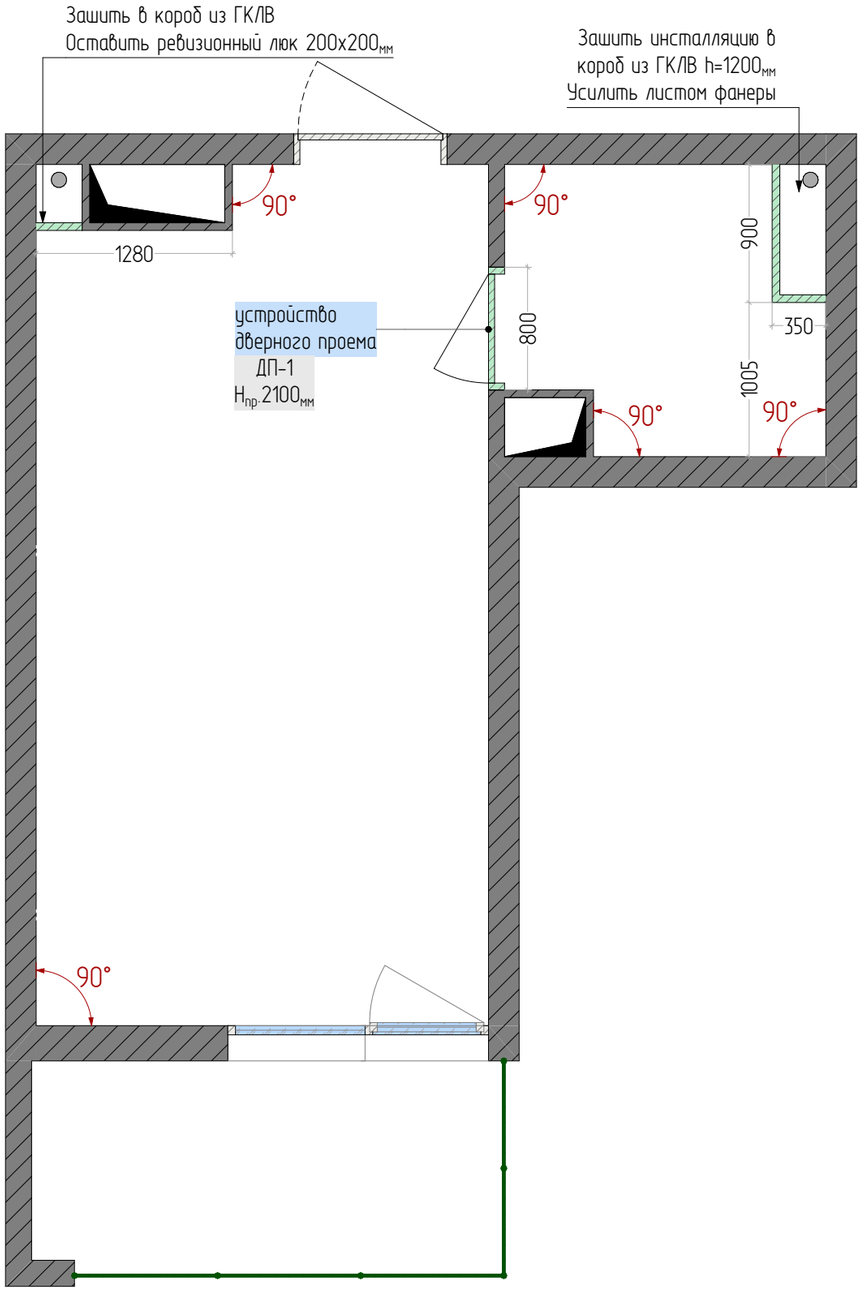

Условные обозначения:

- существующие конструкции
- новые конструкции

Специцикация дверей				
ID	Размеры проёма	Толщина стены, мм	Расположение	Примечание
ДВ	1000×2100	200	входная группа	накладка в цвет стен
ДП-1	800×2100	105	санузел	покраска в цвет стен


Примечание:


1. В первую очередь обращать внимание на выносные надписи.
2. Все размеры и отметки проверить перед началом строительных работ. Несоответствие размеров и отметок согласовать с дизайнером.
3. Размеры указаны в готовом виде с учётом выравнивания и отделки чистовыми материалами.
4. Высота всех перегородок и конструкций до потолка, если не указано на плане.
5. Размеры выделенные красным обязательны к соблюдению.
6. Материалы возводимых перегородок, способ, материалы крепления и усиления требуют согласования со специалистом-строителем.
7. Высота всех проемов указана от уровня чистового пола.
8. Все стены выровнять под 90 градусов (для точного примыкания ко встроенной мебели), а также откосы окон и проемов
9. Расположение счетчиков, коллекторного узла, скрытых люков ревизии для доступа к счетчикам и коммуникациям определяются прорабом.

Дизайн-проект квартиры по адресу: Адрес	Заказчик Заказчик	План возводимых перегородок с маркировкой дверных проемов	Масштаб 1:40	Лист	Листов	чертёжник	Шинкевич Екатерина	SHEM
				04	26	телефон	+7 (931) 271-59-56	

План после перепланировки

Экспликация помещений		
№	Название помещения	Площадь, кв.м
1	Студия	16,14
2	Санузел	3,74
3	Балкон	4,00
4	Кладовая	4,37
		28,25 м²

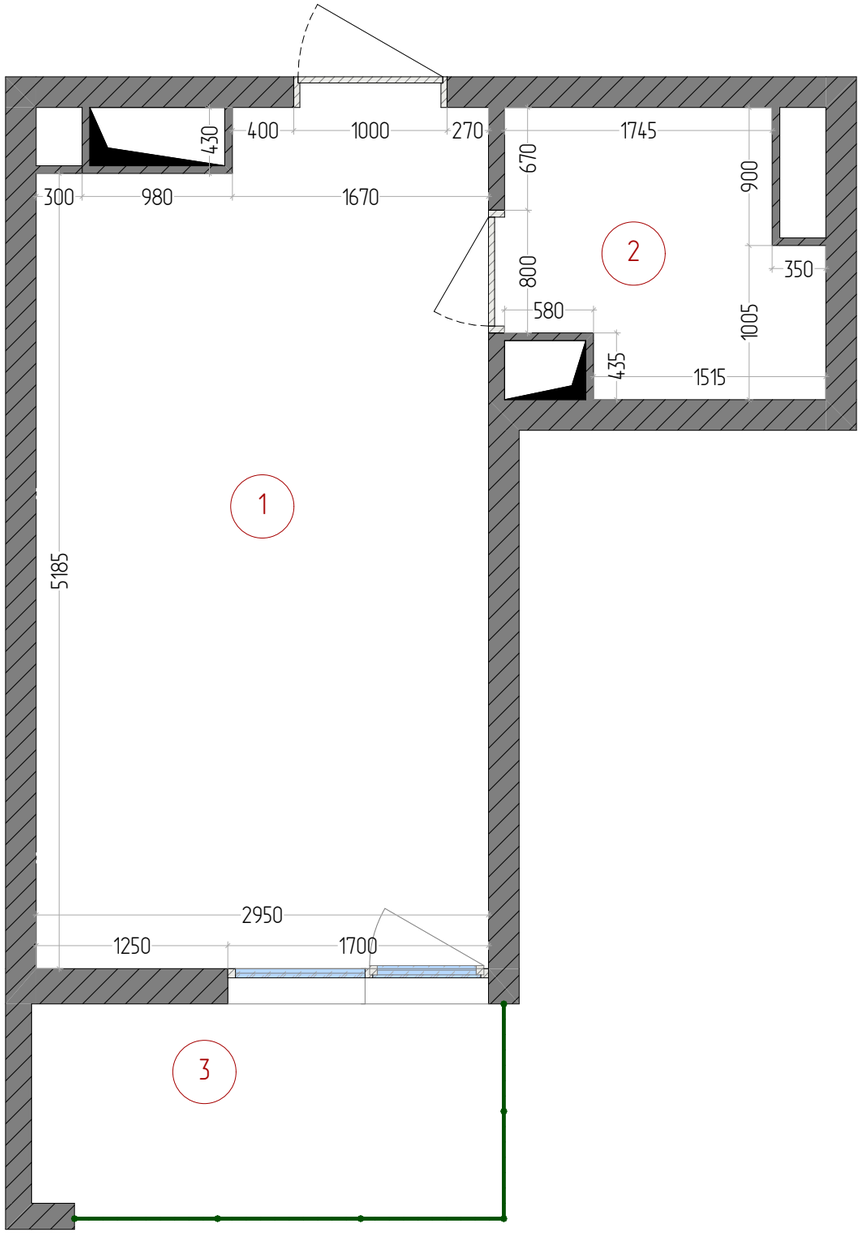

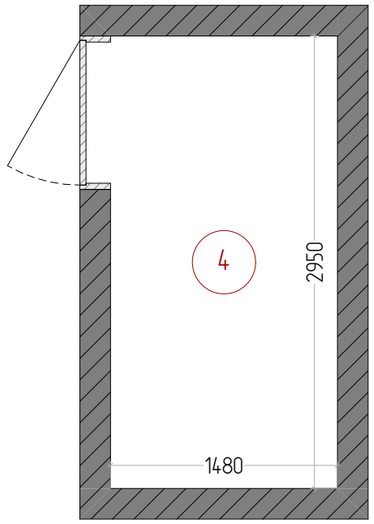



Примечание:
1. Все размеры являются проектируемыми и требуют уточнения на этапе чистовой отделки.
2. В проекте не учтены отклонения на кривизну стен и перекрытий.
3. После возведения перегородок и конструкций произвести контрольный обмер помещения.

Дизайн-проект квартиры по адресу: Адрес	Заказчик Заказчик	План после перепланировки	Масштаб 1:40	Лист	Листов	чертёжник	Шинкевич Екатерина
				05	26	телефон	+7 (931) 271-59-56

План расстановки мебели

Экспликация помещений		
№	Название помещения	Площадь, кв.м
1	Студия	16,14
2	Санузел	3,74
3	Балкон	4,00
4	Кладовая	4,37
		28,25 м²

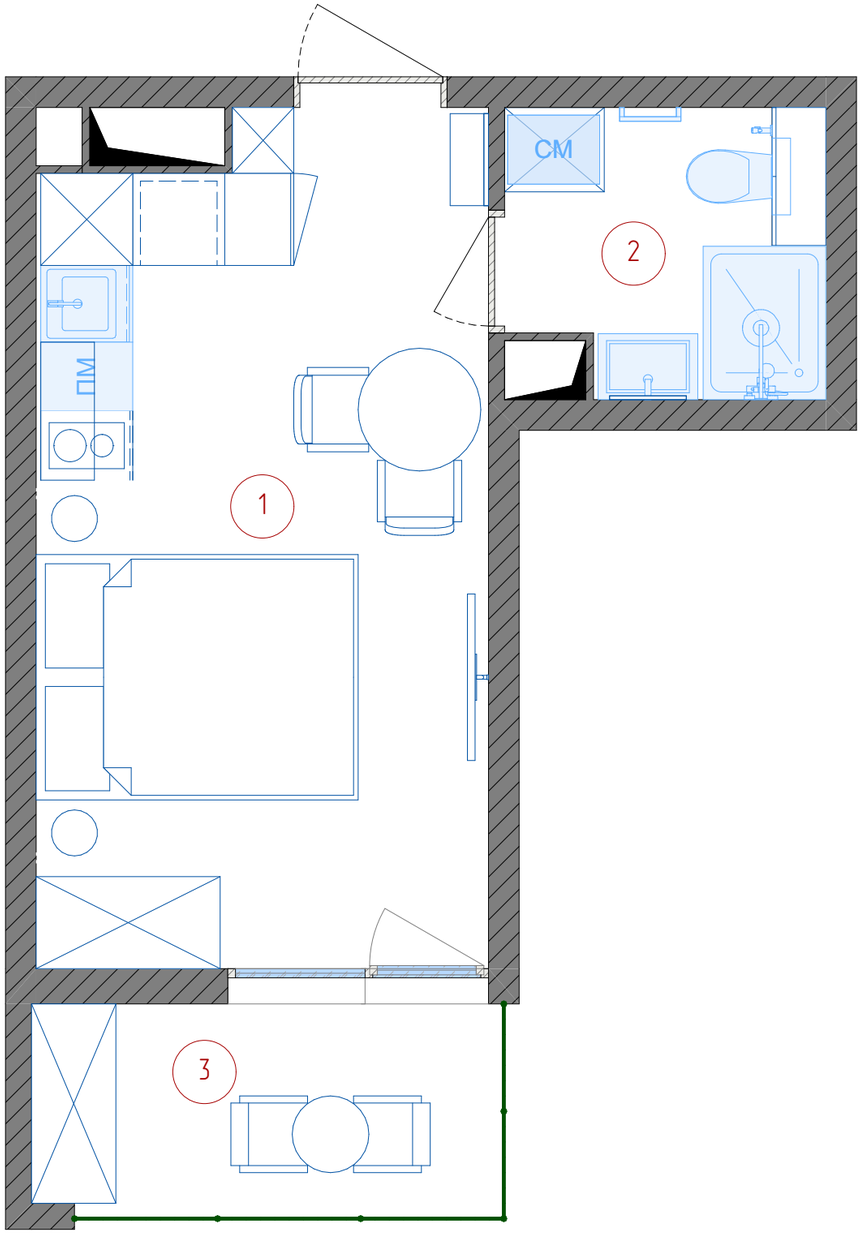

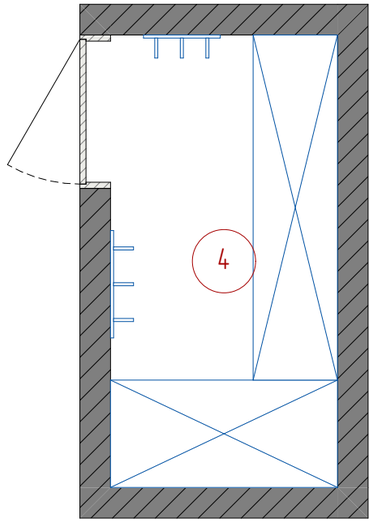



Примечание:
1. Планировочное решение носит рекомендательный характер, НЕ ЯВЛЯЕТСЯ проектом перепланировки (ст. 26 ЖК РФ).

Дизайн-проект квартиры по адресу: Адрес	Заказчик Заказчик	План расстановки мебели	Масштаб 1:40	Лист	Листов	чертёжник	Шинкевич Екатерина
				06	26	телефон	+7 (931) 271-59-56

План с мебельными размерами и описанием

Экспликация помещений		
№	Название помещения	Площадь, кв.м
1	Студия	16,14
2	Санузел	3,74
3	Балкон	4,00
4	Кладовая	4,37
		28,25 м²

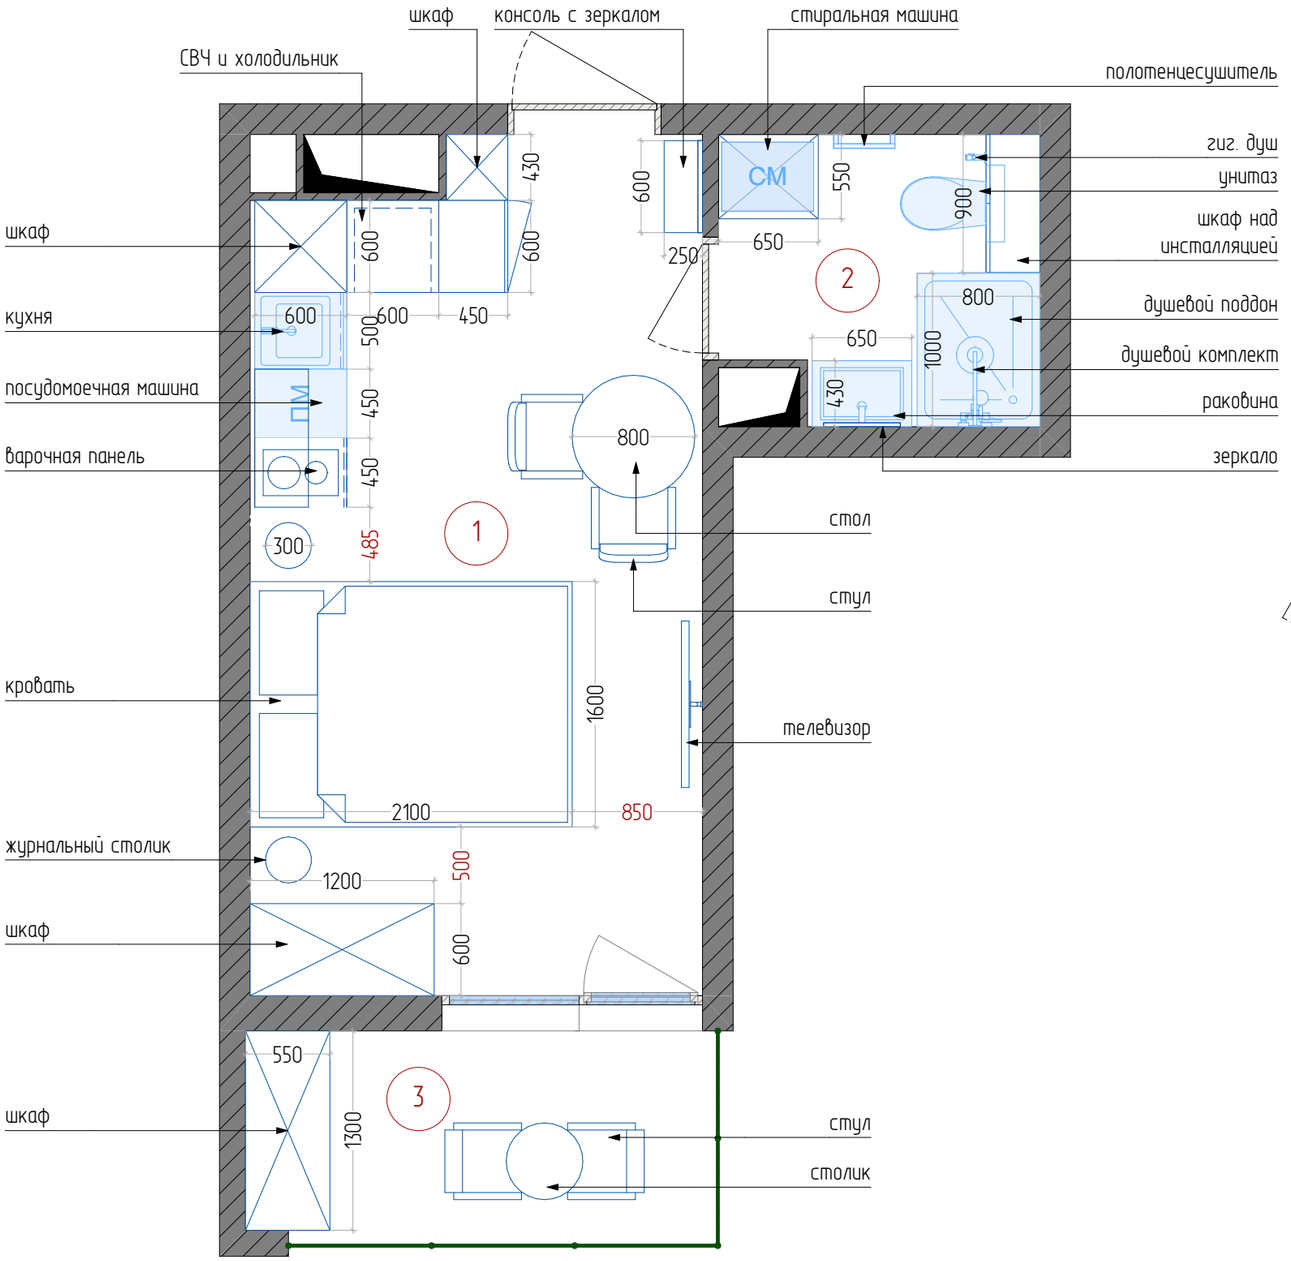

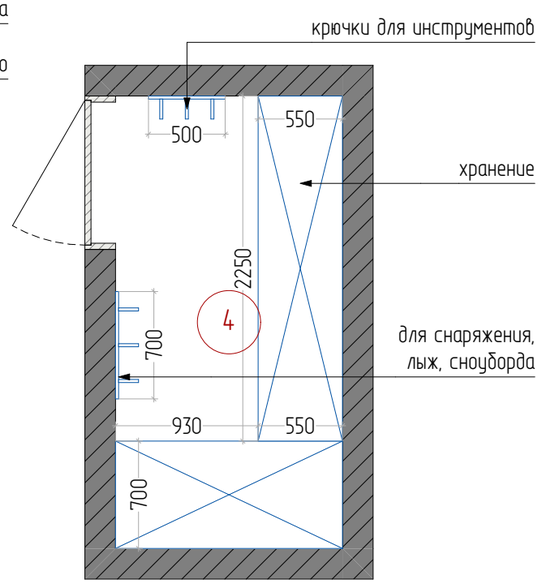

Примечание:

1. Все размеры являются проектируемыми.
2. Красным цветом выделены расстояния между предметами.
3. Перед заказом встраиваемой мебели или иного оборудования требуется предварительный замер фирмой производителем.
4. Закупку мебели производить после чистовой отделки.

Дизайн-проект квартиры по адресу: Адрес	Заказчик Заказчик	План с мебельными размерами и описанием	Масштаб 1:40	Лист	Листов	чертёжник	Шинкевич Екатерина	SHEM
				07	26	телефон	+7 (931) 271-59-56	

План размещения осветительных приборов, привязка выпусков освещения



Условные обозначения:

– Электровывод

Условное обозначение светильников			
ID	Изображение	Тип светильника	Кол-во
C01		потолочный накладной светильник	7
C02		подвесной светильник	2
C03		люстра потолочная	1
C04		люстра подвесная	1
C05		настенный светильник (бра)	2
C06		уличный светильник	1
			14


LED лента			
ID	Условное обозначение	Наименование	Длина, мм
C01		"парящий" потолок	16850
C02		подсветка полок и ниш	860

Примечание:

1. В санузле установить влагозащитные светильники.
2. В первую очередь обращать внимание на выносные надписи.
3. Все размеры даны по осям осветительных приборов.
4. Расположение светодиодных лент смотреть в развертках.

Дизайн-проект квартиры по адресу: Адрес	Заказчик Заказчик	План размещения осветительных приборов, привязка выпусков освещения	Масштаб 1:40	Лист	Листов	чертёжник	Шинкевич Екатерина	SHEM
				08	26	телефон	+7 (931) 271-59-56	

План выключателей с указанием включения групп светильников

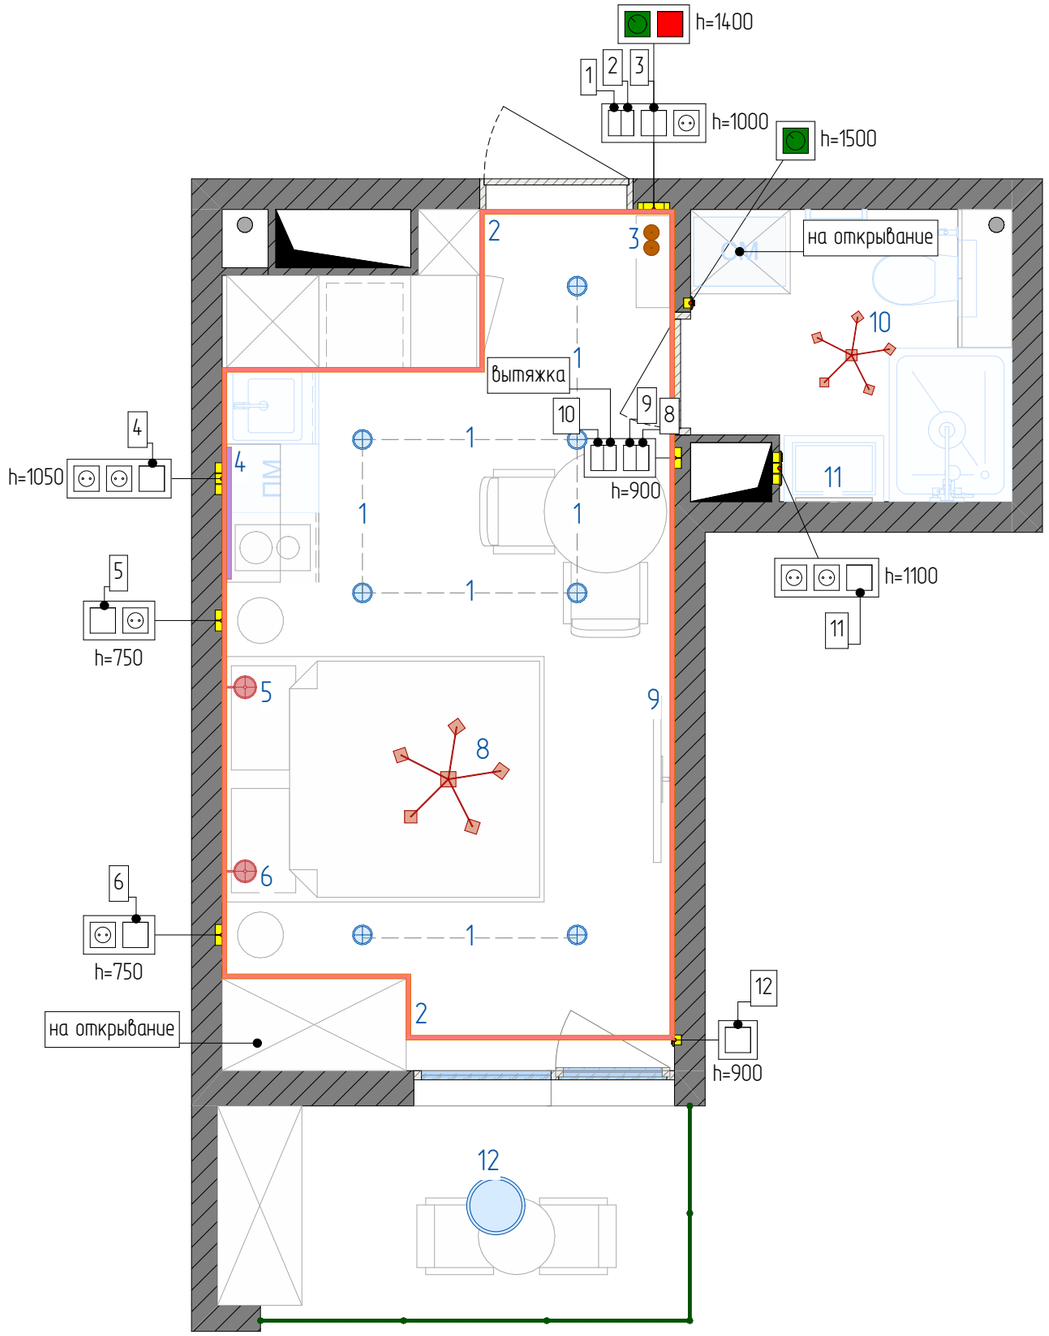

Условное обозначение светильников			
ID	Изображение	Тип светильника	Кол-во
C01		потолочный накладной светильник	7
C02		подвесной светильник	2
C03		люстра потолочная	1
C04		люстра подвесная	1
C05		настенный светильник (бра)	2
C06		уличный светильник	1
			14


Выключатели		
Условное обозначение	Наименование	Кол-во, шт
	Выключатель двухклавишный	4
	Выключатель одноклавишный	5
	Мастер-выключатель	1
	Регулятор тёплого пола	2

Примечание:

1. Все высоты даны от уровня чистового пола.
2. Выключатели располагать на высоте 900$_{мм}$, если не указано другое.
3. Размещение подрозетников в монолитных стенах возможно только после получения технического заключения о том, что штукатурный слой в каждом конкретном месте позволяет выполнить штробление, на затрагивая арматуру и не ослабляя конструкцию стены.
4. Данный лист смотреть совместно с листами освещения и спецификации.

Дизайн-проект квартиры по адресу: Адрес	Заказчик Заказчик	План выключателей с указанием включения групп светильников	Масштаб 1:40	Лист	Листов	чертёжник	Шинкевич Екатерина	SHEM
				09	26	телефон	+7 (931) 271-59-56	

План размещения электрических розеток с привязкой размеров

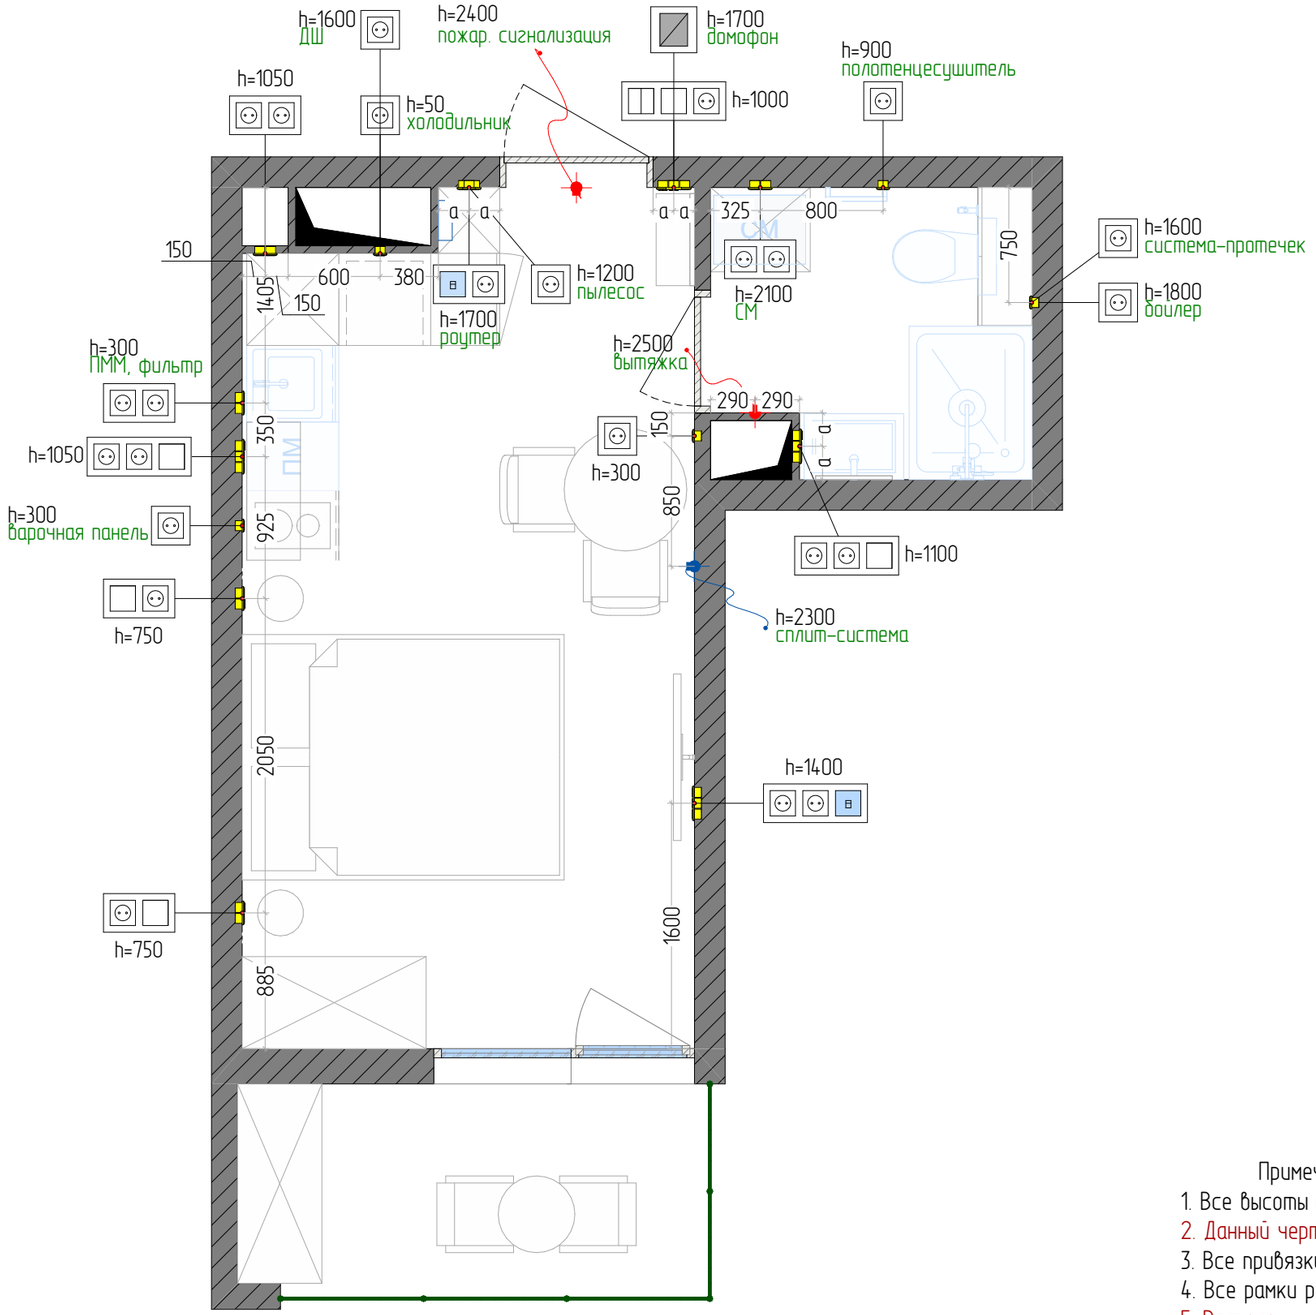

Условные обозначения:

- Электровывод

Рамки (общее количество)		
Тип рамки (блока)	Рамка ориентация	Кол-во
Рамка x1	Горизонтальная	10
Рамка x2	Горизонтальная	7
Рамка x3	Горизонтальная	4


Условное обозначение	Наименование	Кол-во, шт
	Интернет-розетка	2
	Розетка бытовая	24

Примечание:

1. Все высоты указаны в миллиметрах от уровня чистового пола, если не указано иное.
2. Данный чертеж является техническим заданием для электропроекта.
3. Все привязки указаны до центра рамок.
4. Все рамки расположены горизонтально, если не указано иное.
5. Расположение электровыводов за кухонной мебелью согласовать с производителем кухни. Окончательное расположение розеток на кухне определяет электрик по техническому заданию кухни.
6. Предусмотреть влагозащитные розетки (класс защиты не менее IP44) во влажных помещениях.
7. Уточнить способ подключения и место вывода для вытяжки, варочной панели, духового шкафа и полотенцесушителя (модель поставляется с вилкой или кабелем).
8. Точное размещение силового и слаботочного электрощитов согласовать с лицом, осуществляющим авторский надзор.

Дизайн-проект квартиры по адресу: Адрес	Заказчик Заказчик	План размещения электрических розеток с привязкой размеров	Масштаб 1:40	Лист	Листов	чертёжник	Шинкевич Екатерина
				10	26	телефон	+7 (931) 271-59-56

План потолков и гипсокартонных конструкций

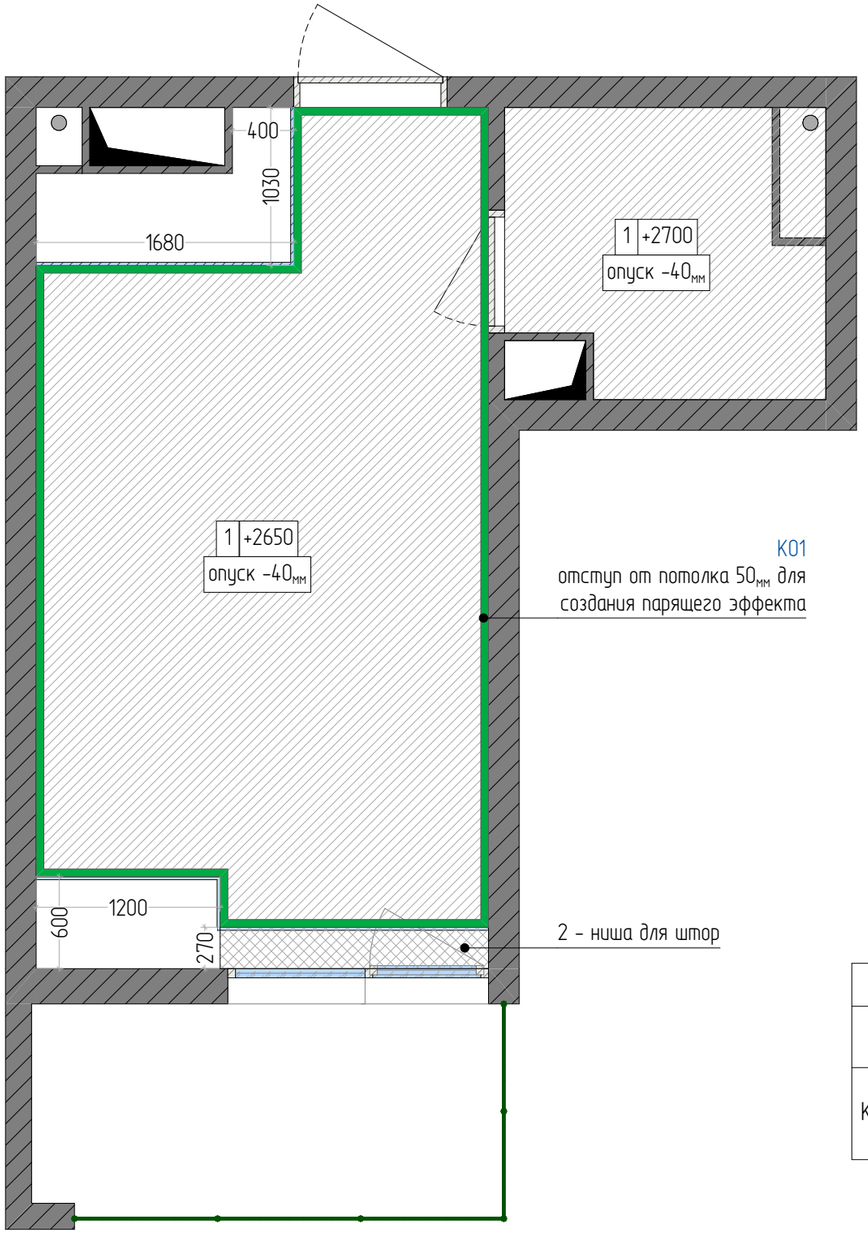

Условные обозначения:

02 - обозначение типа потолка

+2 900 - отметка высоты относительно чистового пола

- фальшпланка для монтажа потолка

карниз 1.50.121

Ведомость потолков

ID	Условное обозначение	Наименование	Площадь, кв.м (без запаса)
1		Натяжной потолок	17,38
2		Штукатурка и покраска	0,47

Спецификация карниза


ID	Условное обозначение	Сечение	Изображение	Наименование	Артикул	Производитель	Длина, мм	Примечание
K01				Карниз	1.50.121	Европласт	16790	101x50x2000мм разместить с отсупом от чистового потолка на 50мм

Примечание:

1. За отметку 0,000 принята высота чистового пола.
2. Подвесной потолок опустить на минимальную высоту (80мм), от самой нижней точки чернового потолка в конкретном помещении.
3. Отметки высот указаны от чистового пола.
4. На развертках все высоты даны от чистового пола.

Дизайн-проект квартиры по адресу: Адрес	Заказчик Заказчик	План потолков и гипсокартонных конструкций	Масштаб 1:40	Лист 11	Листов 26	чертёжник телефон	Шинкевич Екатерина +7 (931) 271-59-56	SHEM

План полов с указанием типа напольных покрытий

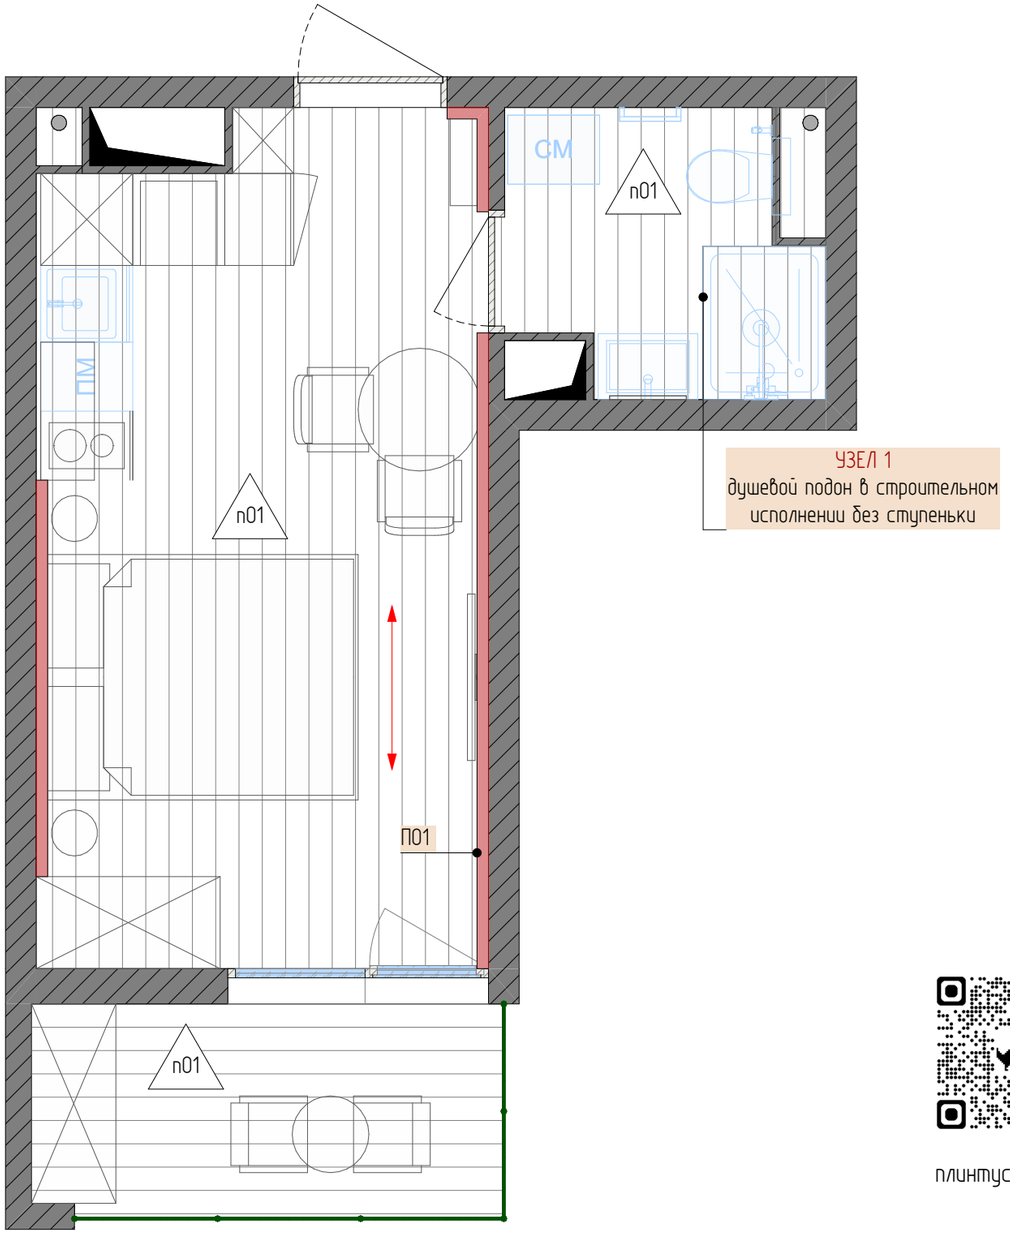


УЗЕЛ 1
душевой подон в строительном исполнении без ступеньки

Условные обозначения:

– направление укладки плитки

п02 – обозначение типа пола

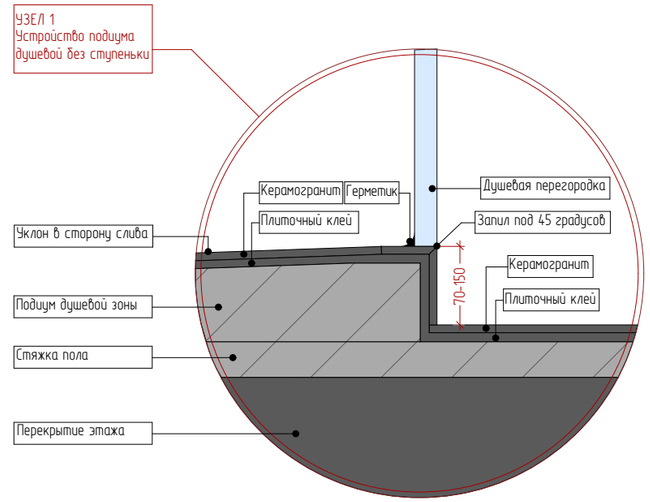

Напольные покрытия				
ID	Условное обозначение	Наименование	Площадь, кв.м (без запаса)	Примечание
п01		Керамогранит под дерево	24,24	раскладка палубная

плинтус 6.53.124


Спецификация плинтуса							
ID	Условное обозначение	Сечение	Изображение	Наименование	Артикул	Производитель	Длина, мм
П01				Плинтус	6.53.124	Европласт	7680

Примечание:

1. Все размеры даны в миллиметрах
2. Все размеры даны по неоштукатуренным стенам и перегородкам.
3. Для стыковки плитки и ламината применить пробковый компенсатор или силиконовый клей-герметик.
4. Метраж плинтуса уточнить после согласования финальных размеров мебели. Закупку и заказ мебели производить после чистовой отделки помещений.

Дизайн-проект квартиры по адресу: Адрес	Заказчик Заказчик	План полов с указанием типа напольных покрытий	Масштаб 1:40, 1:5,41	Лист	Листов	чертёжник	Шинкевич Екатерина	SHEM
				12	26	телефон	+7 (931) 271-59-56	


План расположения систем отопления и вентиляции

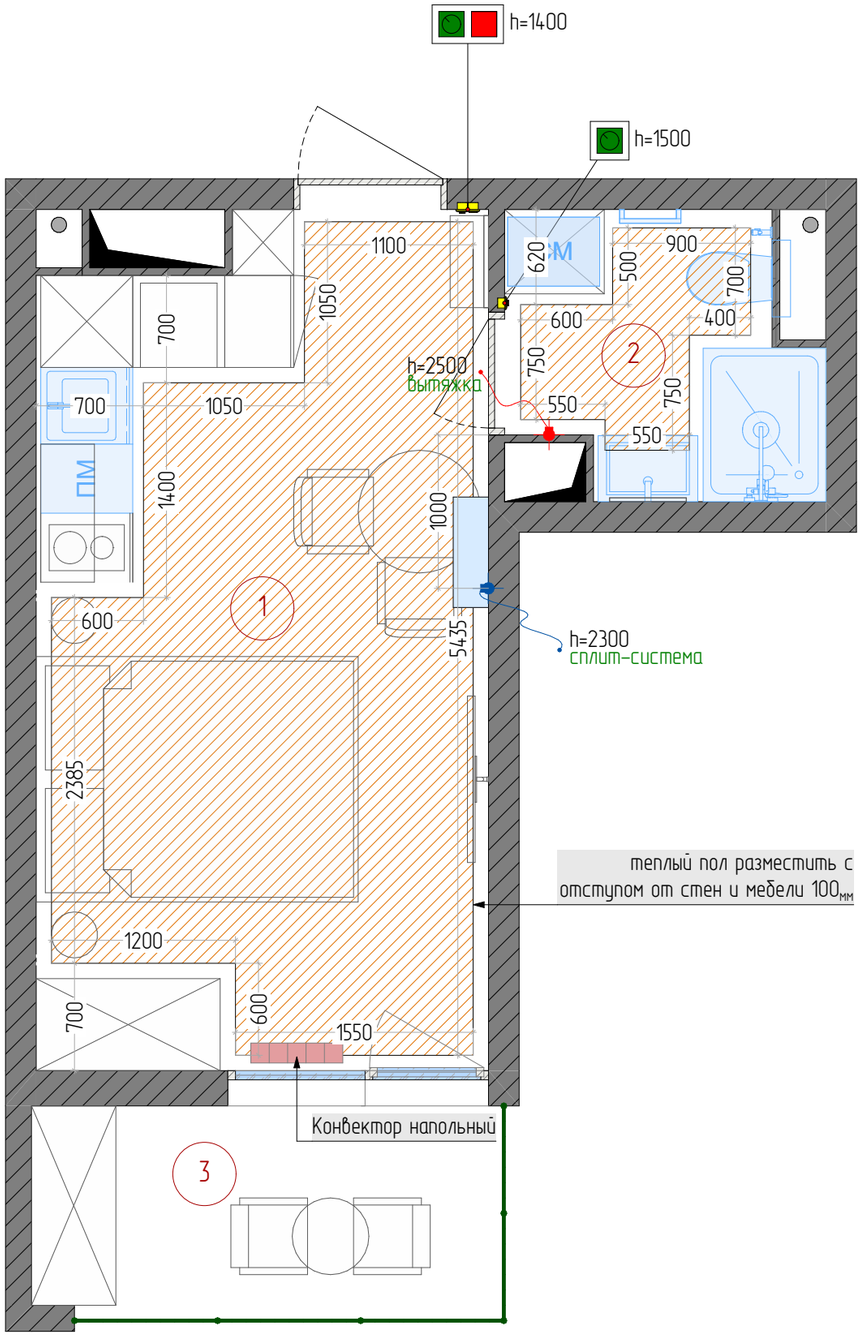

Условные обозначения:

– радиаторы отопления

Экспликация помещений		
№	Название помещения	Площадь, кв.м
1	Студия	16,14
2	Санузел	3,74
3	Балкон	4,00
4	Кладовая	4,37
		28,25 м²

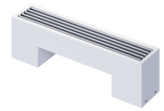

Конвектор напольный Royal Thermo STEP-80/130/600-1-N-WT-LG-NA

Регулятор тёплого пола		
Условное обозначение	Наименование	Кол-во, шт
	Регулятор теплого пола	2


Теплый пол		
Условное обозначение	Наименование	Площадь, кв.м
	Тёплый пол	13,11
		13,11 м²

Примечание:

1. Проверить совместимость напольного покрытия с тёплым полом и максимальную температуру нагрева.
2. Предусмотреть технологический отступ от стен и габаритных предметов интерьера не менее 100мм. Уточнить в тех.карте к изделию.
3. Данный план смотреть совместно с планом полов и планом электрики.

Дизайн-проект квартиры по адресу: Адрес	Заказчик Заказчик	План расположения систем отопления и вентиляции	Масштаб 1:40	Лист 13	Листов 26	чертёжник телефон	Шинкевич Екатерина +7 (931) 271-59-56	SHEM

План размещения санитарно-технического оборудования

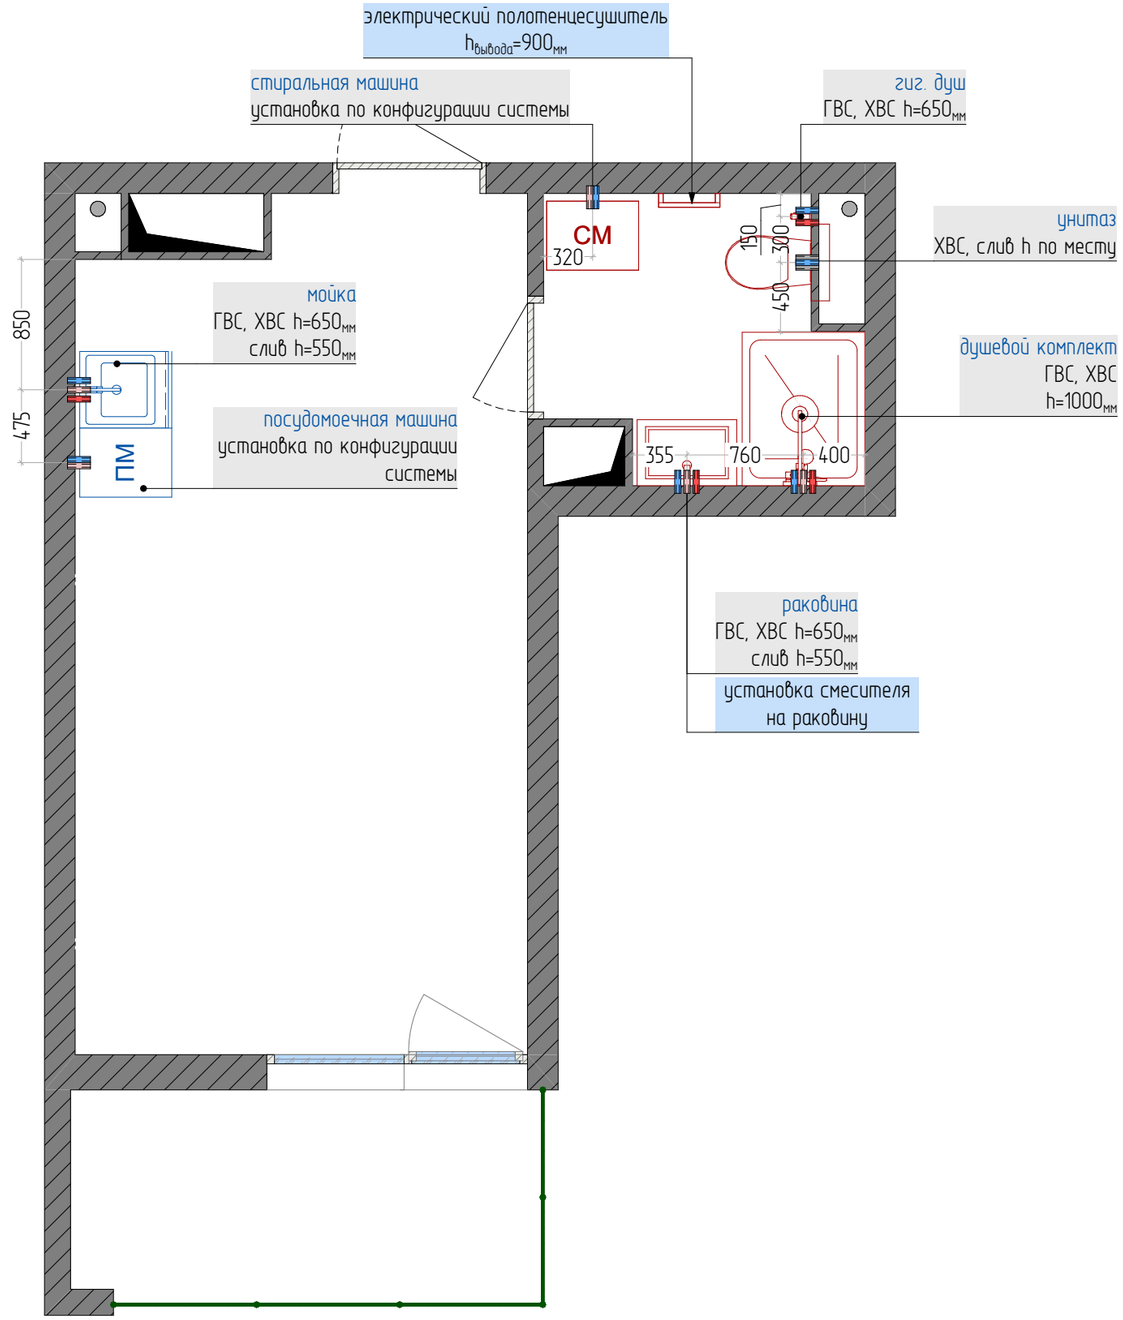

Условные обозначения:


- канализационная труба
- труба подачи горячего водоснабжения
- труба подачи холодного водоснабжения
- размещение стока раковин и сливов

Примечание:

1. Перед началом работ все размеры уточнить по месту специалистом.
2. Все размеры даны по конструкциям, без учета плитки и клея.
3. Организовать гидроизоляцию стен и пола в ванных комнатах.

Дизайн-проект квартиры по адресу: Адрес	Заказчик Заказчик	План размещения санитарно-технического оборудования	Масштаб 1:40	Лист	Листов	чертёжник	Шинкевич Екатерина	SHEM
				14	26	телефон	+7 (931) 271-59-56	

План отделочных материалов по стенам

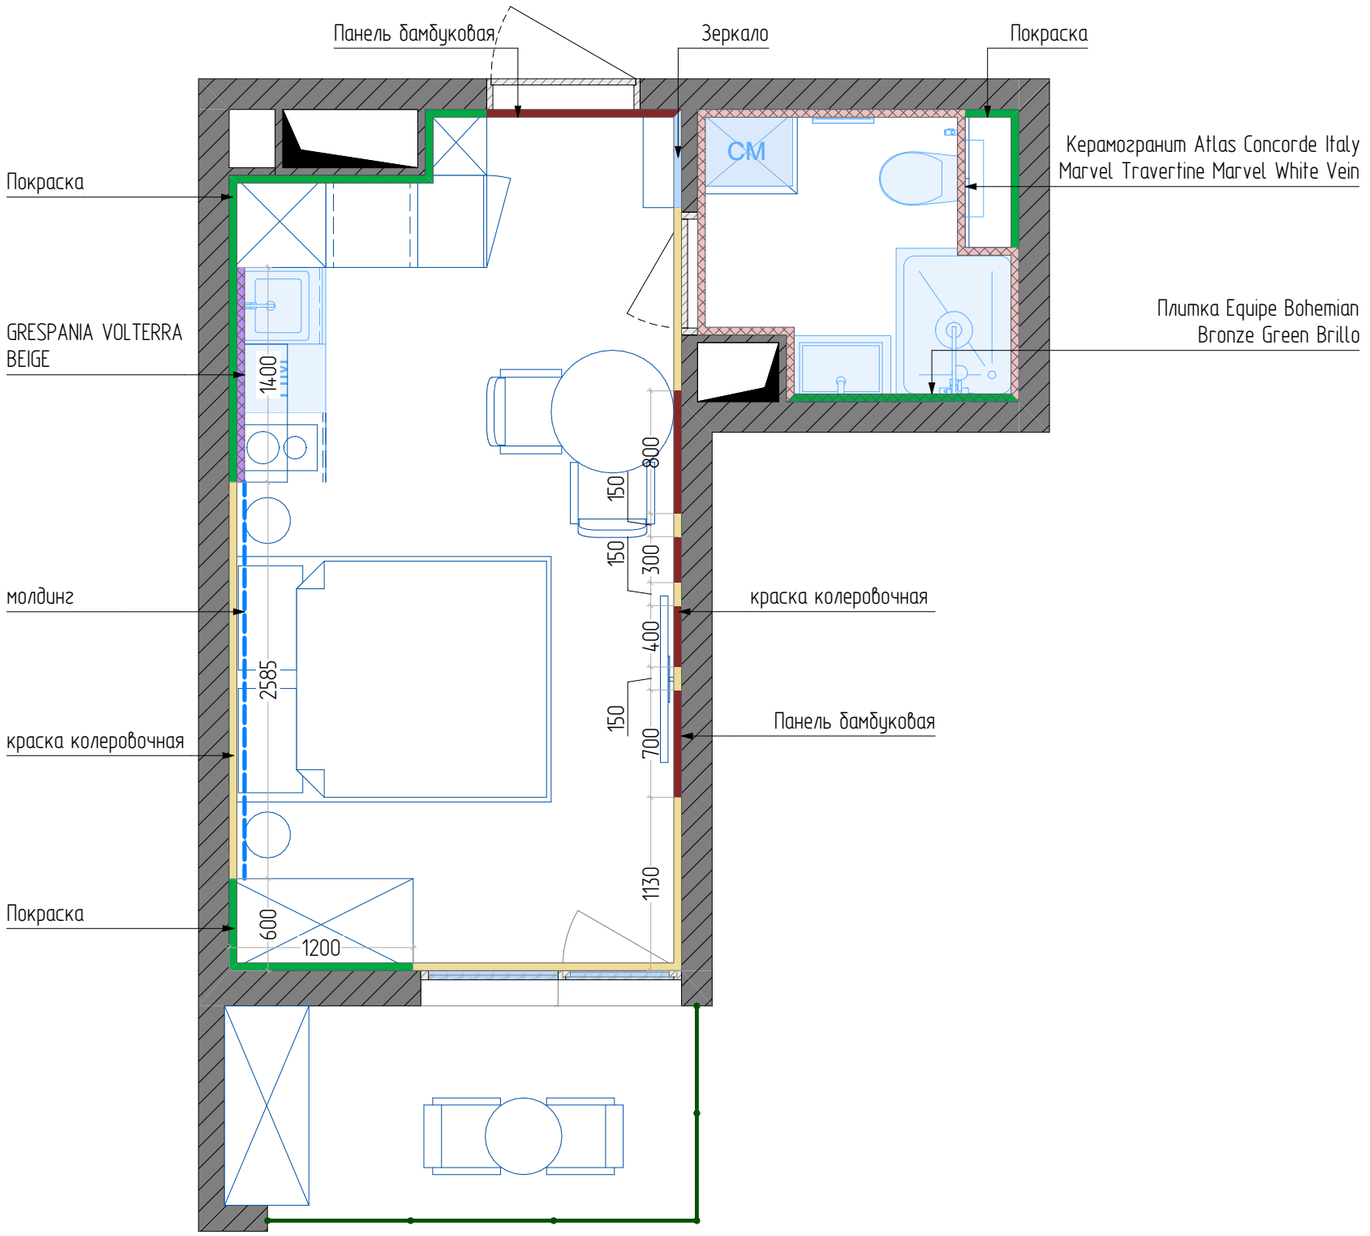



Условное обозначение	Наименование
	Покраска
	GRESPANIA VOLTERRA BEIGE
	Панель бамбуковая
	краска колеровочная
	Зеркало
	Керамогранит Atlas Concorde Italy Marvel Travertine Marvel White Vein
	Плитка Equipe Bohemian Bronze Green Brillo


Примечание:
1. Все размеры даны в миллиметрах
2. Точное расположение покрытий смотреть на развертках соответствующих помещений.


Дизайн-проект квартиры по адресу: Адрес	Заказчик Заказчик	План отделочных материалов по стенам	Масштаб 1:40	Лист	Листов	чертёжник	Шинкевич Екатерина	SHEM
				15	26	телефон	+7 (931) 271-59-56	


Развертки по стенам. Студия

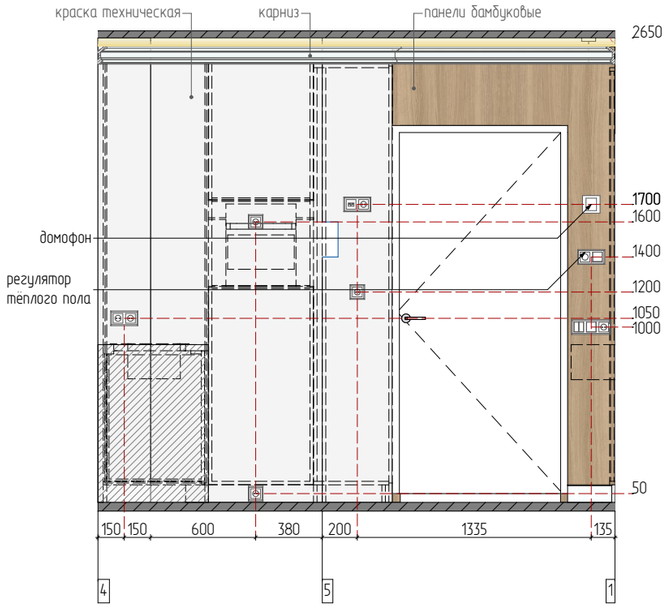

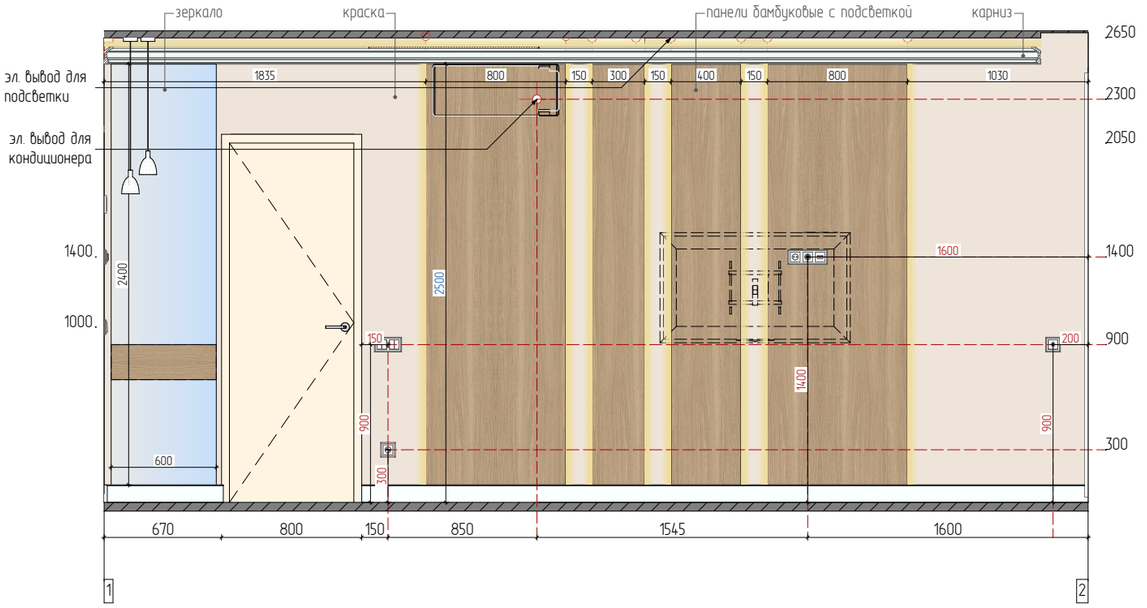

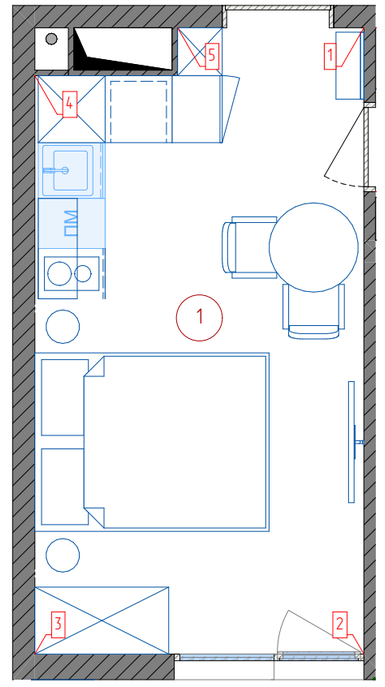

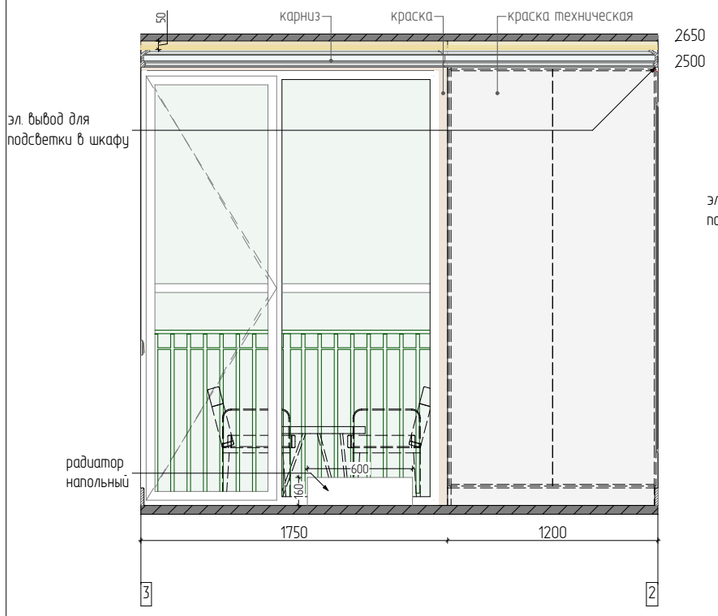

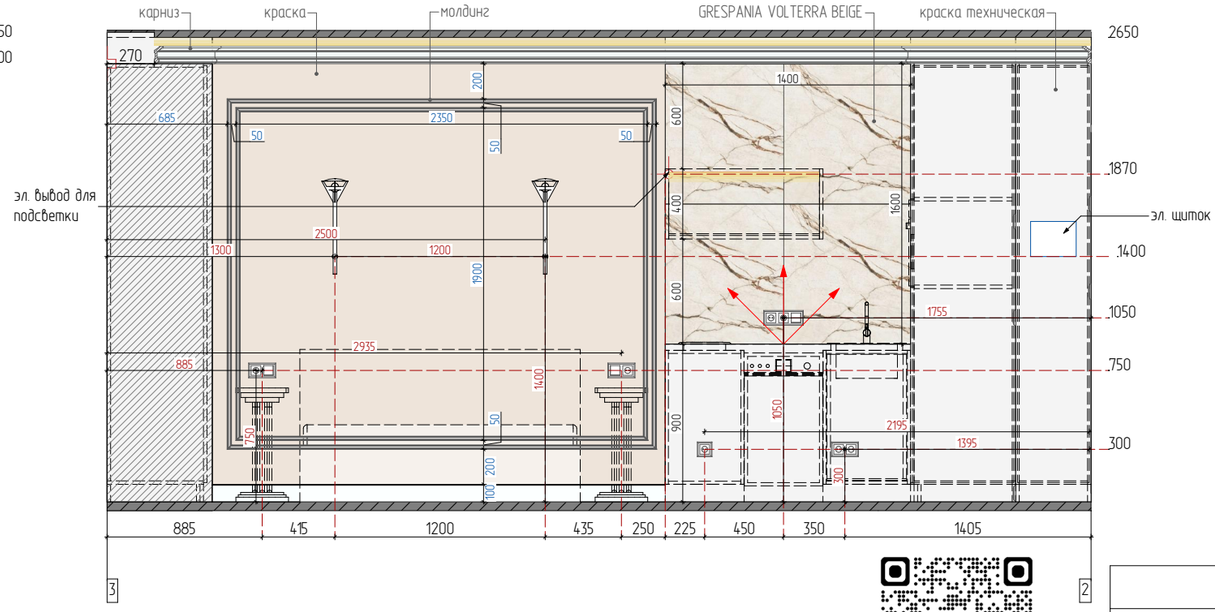

Панели бамбуковые 120x280 - 2 шт



GRESPANIA VOLTERRA BEIGE 80x80

молдинг 1.51.322

Расход материалов. Студия			
Наименование	Условное обозначение	Площадь, кв.м (без запаса)	Примечание
GRESPANIA VOLTERRA BEIGE		2,24	80x80см, 4 штуки
Краска		17,67	подбирается после выкрасов с дизайнером
Краска черновая		13,22	за мебелью

Расход материалов Молдинги				
Наименование	Длина, мм	Производитель	Артикул	Примечание
M01	17400	Европласт	1.51.322	25x12x2000 мм

Примечание:
1. Количество материала для отделки стен дано без запаса.
2. Пересчитать все материалы перед заказом с менеджером бренда (используя данные проекта).
3. Согласовать все размеры при заказе мебели.

Дизайн-проект квартиры по адресу: Адрес	Заказчик Заказчик	Развертки по стенам. Студия	Масштаб 1:35	Лист 16	Листов 26	чертёжник телефон	Шинкевич Екатерина +7 (931) 271-59-56	SHEM







Дизайн-проект квартиры по адресу: Адрес	Заказчик Заказчик	Визуализация	Масштаб	Лист 17	Листов 26	чертёжник телефон	Шинкевич Екатерина +7 (931) 271-59-56	SHEM





Дизайн-проект квартиры по адресу: Адрес	Заказчик Заказчик	Визуализация	Масштаб	Лист 18	Листов 26	чертёжник телефон	Шинкевич Екатерина +7 (931) 271-59-56	SHEM






Дизайн-проект квартиры по адресу: Адрес	Заказчик Заказчик	Визуализация	Масштаб	Лист 19	Листов 26	чертёжник телефон	Шинкевич Екатерина +7 (931) 271-59-56	SHEM








Дизайн-проект квартиры по адресу: Адрес	Заказчик Заказчик	Визуализация	Масштаб	Лист 20	Листов 26	чертёжник телефон	Шинкевич Екатерина +7 (931) 271-59-56	SHEM


Развертки по стенам. Санузел

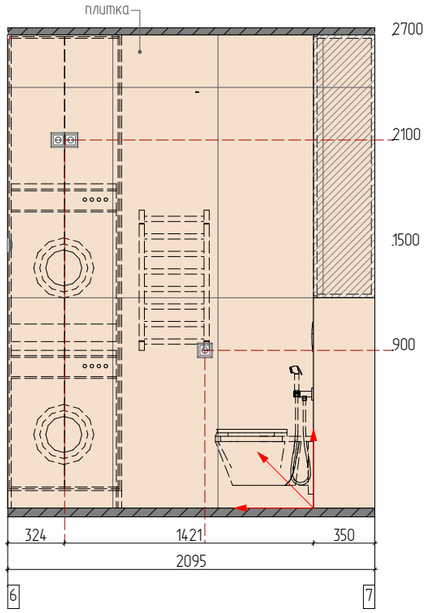

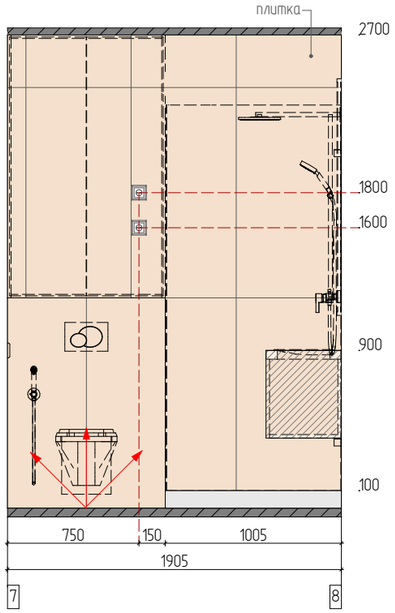

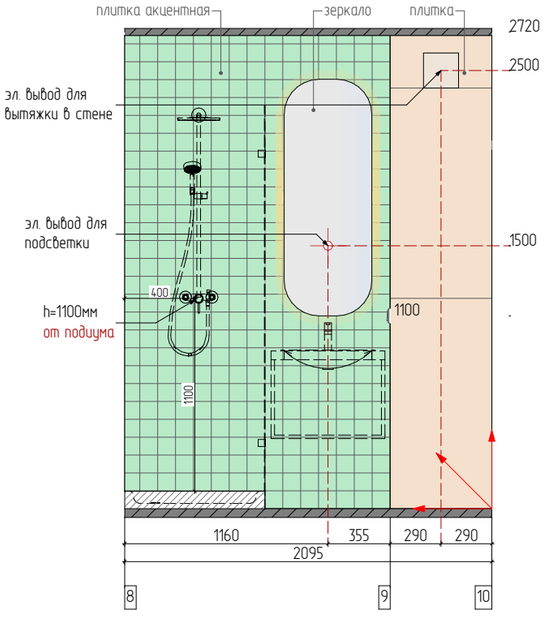

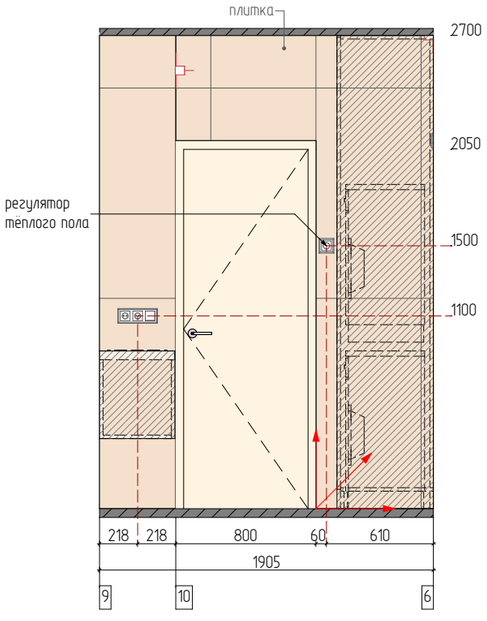

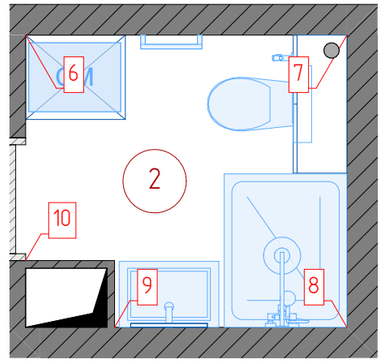

Плитка Equipe Bohemian Bronze Green Brillo 10x10H0.8

Керамогранит Atlas Concorde Italy Marvel Travertine Marvel White Vein 60x120 Бежевый

Примечание:
1. Количество материала для отделки стен дано без запаса.
2. Пересчитать все материалы перед заказом с менеджером бренда (используя данные проекта).
3. Согласовать все размеры при заказе мебели.

Расход материалов. Санузел			
Наименование	Условное обозначение	Площадь, кв.м (без запаса)	Примечание
Керамогранит Atlas Concorde Italy Marvel Travertine Marvel White Vein		15,71	60x120 Бежевый
Плитка Equipe Bohemian Bronze Green Brillo		4,09	10x10H0.8

Дизайн-проект квартиры по адресу: Адрес	Заказчик Заказчик	Развертки по стенам. Санузел	Масштаб 1:35	Лист 21	Листов 26	чертёжник телефон	Шинкевич Екатерина +7 (931) 271-59-56








Дизайн-проект квартиры по адресу: Адрес	Заказчик Заказчик	Визуализация	Масштаб	Лист	Листов	чертёжник	Шинкевич Екатерина	SHEM
				22	26	телефон	+7 (931) 271-59-56	







Дизайн-проект квартиры по адресу: Адрес	Заказчик Заказчик	Визуализация. Балкон	Масштаб	Лист 23	Листов 26	чертёжник телефон	Шинкевич Екатерина +7 (931) 271-59-56	SHEM

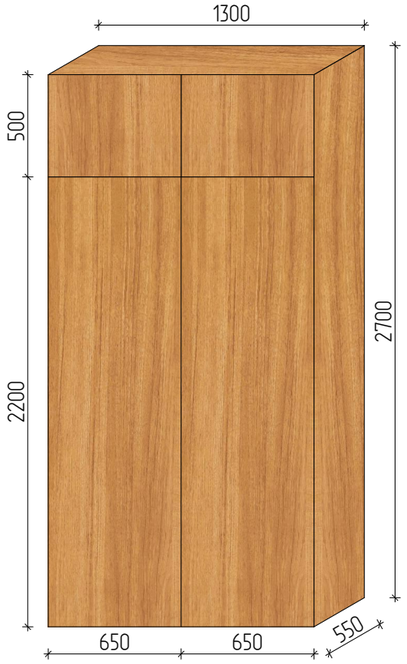


тип мебели: шкаф
местоположение: балкон
ручки подбираются с дизайнером
внутреннее наполнение согласовать с Заказчиком

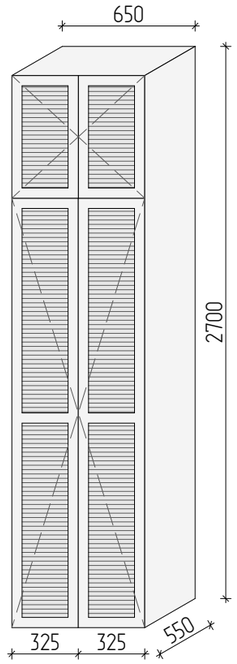


тип мебели: шкаф для стиральной машины
местоположение: санузел
ручки подбираются с дизайнером

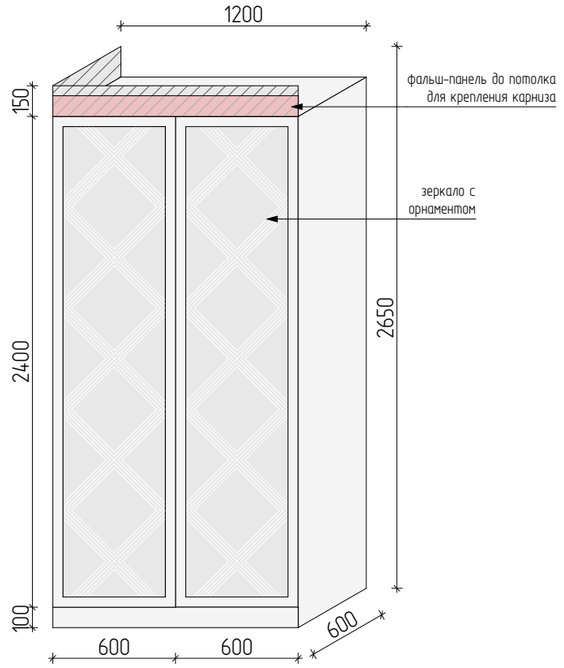


тип мебели: шкаф-купе
местоположение: студия

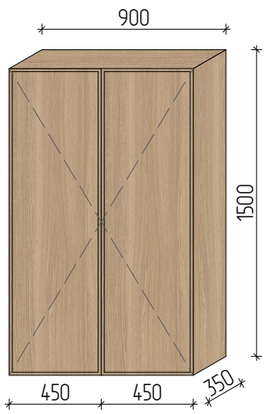


тип мебели: шкаф над инсталляцией
местоположение: санузел

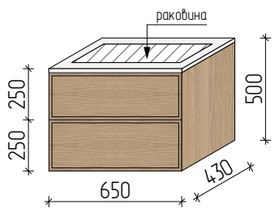

тип мебели: тумба под раковину
местоположение: санузел
установка смесителя на раковину
ручки подбираются с дизайнером

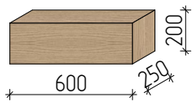

тип мебели: консоль
местоположение: студия

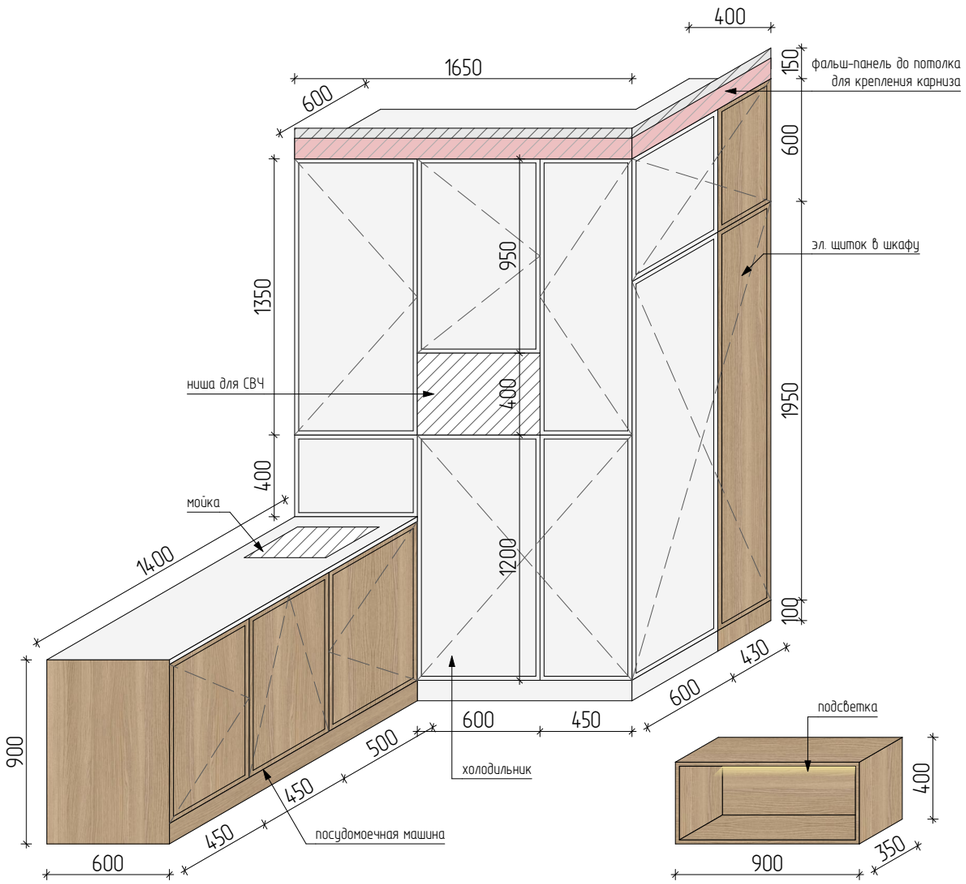

тип мебели: кухонный гарнитур и шкаф в прихожей
местоположение: студия
Все отверстия под технику уточняются после приобретения конкретных моделей
Фрезеровка фасадов

Дизайн-проект квартиры по адресу: Адрес	Заказчик Заказчик	Мебель на заказ	Масштаб 1:30	Лист 24	Листов 26	чертёжник телефон	Шинкевич Екатерина +7 (931) 271-59-56	SHEM

Спецификация мебели

Спецификация мебели								
Тип мебели	Артикул	Производитель	Наименование	QR-код	Изображение	Кол-во	Наименование помещения	Примечание
журнальный столик	69-22446	Гарда Декор	Блеск (Luster)			2	студия	
зеркало	IMR-1566966	InMyRoom	Nolvis NF LED M			1	санузел	с контурной тёплой подсветкой, МДФ, 3000К
стол	IMR-2097766	InMyRoom	Имар			1	кухня	из массива манго, бежевый, 90×90×76 см
стул	IMR-2167636	InMyRoom	Aska			2	кухня	без подлокотников, массив ясеня, рогожка, орех/бежевый, скандинавский стиль, 52×55×84 см

Дизайн-проект квартиры по адресу: Адрес	Заказчик Заказчик	Спецификация мебели	Масштаб	Лист 25	Листов 26	чертёжник телефон	Шинкевич Екатерина +7 (931) 271-59-56	SHEM

Спецификация осветительного оборудования

Спецификация осветительного оборудования								
Тип светильника	Артикул	Производитель	Наименование	QR-код	Изображение	Количество	Расположение	Примечание
уличный светильник	359289	Novotech	Virtuo Street			1	балкон	
подвесной светильник	Lux New SP1 B Amber	Crystal Lux	Lux New			2	прихожая	Мощность 60W, тип цоколя G9
люстра потолочная	ML.2400.500 GD	MODELUX	MODESTYLE			1	санузел	Мощность 60W, тип цоколя LED
люстра подвесная	MS.2106.10 GD	MODELUX	MODESTYLE			1	спальня	Мощность 10x40W, тип цоколя E14
потолочный накладной светильник	a064288	Elektrostandard	Porter			7	студия	Мощность 15W, тип монтажа нкаладной, степень защиты IP20
настенный светильник (бра)	MS.2102.350 GD	MODELUX	MODESTYLE			2	студия	Мощность 3xG9, тип цоколя G9

Дизайн-проект квартиры по адресу: Адрес	Заказчик Заказчик	Спецификация осветительного оборудования	Масштаб	Лист	Листов	чертёжник	Шинкевич Екатерина	SHEM
				26	26	телефон	+7 (931) 271-59-56	