
SHEM

ШИНКЕВИЧ ЕКАТЕРИНА

дизайнер интерьеров

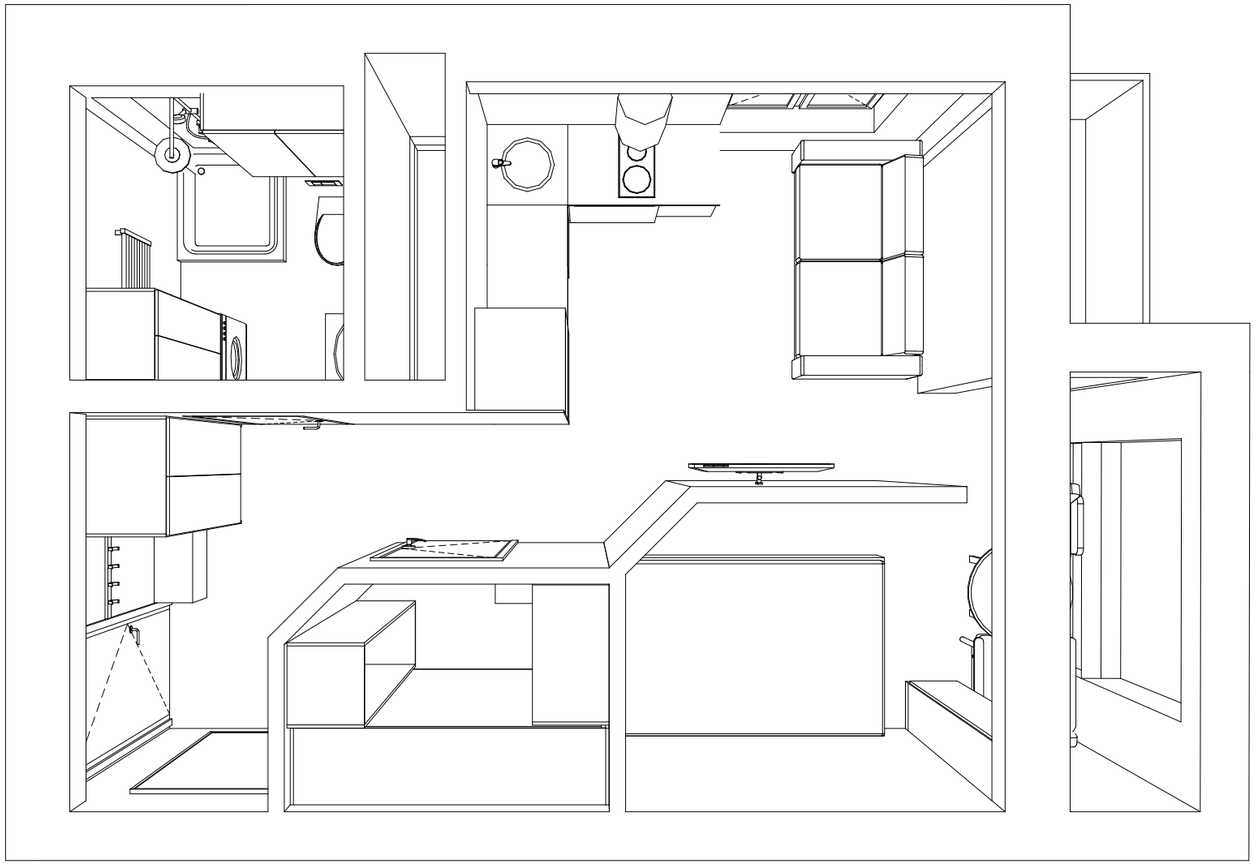

Дизайн-проект квартиры: рабочий проект

ОБЪЕКТ :	квартира
ЗАКАЗЧИК :	заказчик
МЕСТОРАСПОЛОЖЕНИЕ ОБЪЕКТА :	адрес
ТЕЛЕФОН ЗАКАЗЧИКА :	номер

2024

№ листа	Наименование	Примечание
01	Общие данные	
02	Фотофиксация	
03	План обмеров	
04	План демонтажа	
05	План возводимых перегородок и конструкций	
06	План после перепланировки	
07	План расстановки мебели	
08	План с мебельными размерами и описанием	
09	План размещения осветительных приборов, привязка выпусков освещения	
10	План выключателей с указанием включения групп светильников	
11	План размещения электрических розеток с привязкой размеров	
12	План потолков с указанием типа используемых материалов	
13	План полов с указанием типа напольных покрытий	
14	План размещения санитарно-технического оборудования	

№ листа	Наименование	Примечание
15	План расположения систем отопления и вентиляции	
16	План отделочных материалов по стенам	
17	Развертки по стенам. Коридор, кухня, спальня	
18	Развертки по стенам. Коридор, кухня, спальня	
19	Развертки по стенам. Коридор, кухня, спальня	
20	Развертки по стенам. Санузел	
21	Развертки по стенам. Гардеробная	
22	Ниша за диваном	
23	Спецификация отделочных материалов	
24	Коллаж	
25	Коллаж	
26	Коллаж	
27	Коллаж	
28	Коллаж	

ПОЯСНИТЕЛЬНАЯ ЗАПИСКА


К дизайн-проекту интерьера квартиры, расположенной по адресу: адрес
Проект выполнен на основании обмеров. Квартира имеет общую площадь: 28,64 м^2
Благоустройство квартиры: централизованная система отопления, система очистки воды, электроснабжение, центральная канализация, бойлер.
Наружные стены - кирпич. Внутренние стены - газоблок.

Необходимо произвести следующие работы:
1. Возвести новые перегородки из кирпича согласно РП-05;
1. Устроить потолки согласно РП-12;
2. Выполнить электропроводку согласно РП-09, РП-10, РП-11;
3. Полы устроить согласно РП-13 и РП-15;
4. Произвести отделку согласно РП-16.

Проект квартиры полностью удовлетворяет пожеланиям Заказчика.

Дизайнер	Шинкевич Екатерина	Дизайн-проект квартиры по адресу:	Общие данные	Стадия	Лист	Листов
				РП	01	28
телефон	+7 (931) 271-59-56	адрес	Масштаб	SHEM		

План обмеров

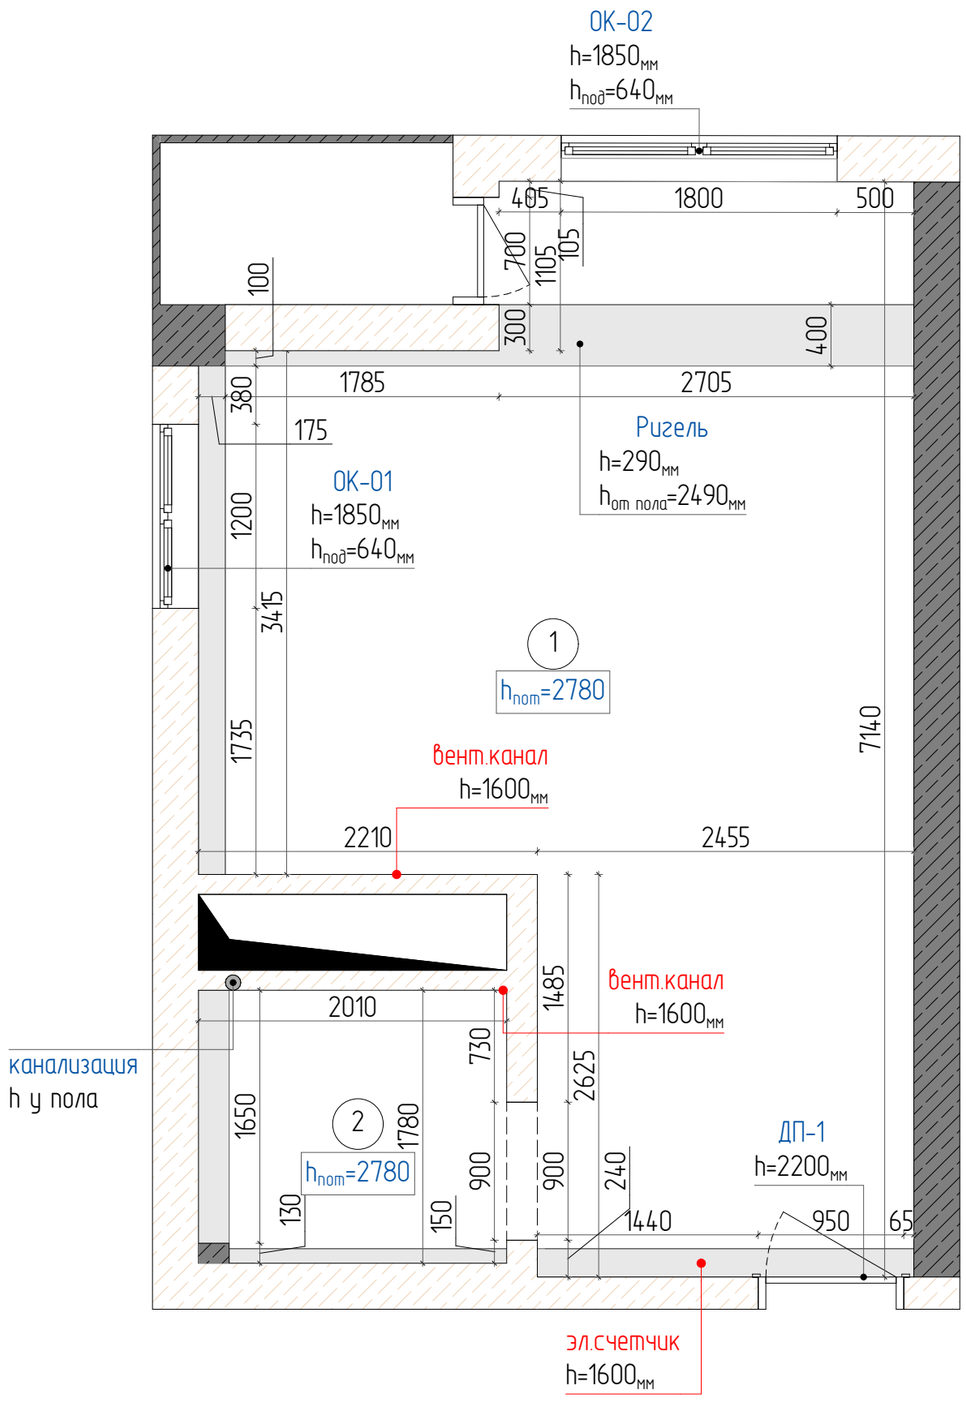

Условные обозначения:

- канализационная труба
- существующие конструкции из монолита
- существующие конструкции из газобетона
- ригель


Экспликация помещений на этапе обмеров		
№	Название помещения	Площадь, кв.м
1	Помещение 1	25,03
2	Помещение 2	3,61
		28,64 м²

Примечание:

1. Все размеры даны в мм.
2. Обмерный план выполнен на основании обмера. Погрешность составляет не более 30мм.
3. Высота потолка 2780мм.

Дизайнер	Шинкевич Екатерина	Дизайн-проект квартиры по адресу:	План обмеров	Стадия	Лист	Листов
				РП	03	28
телефон	+7 (931) 271-59-56	адрес	Масштаб 1:40	SHEM		

План демонтажа

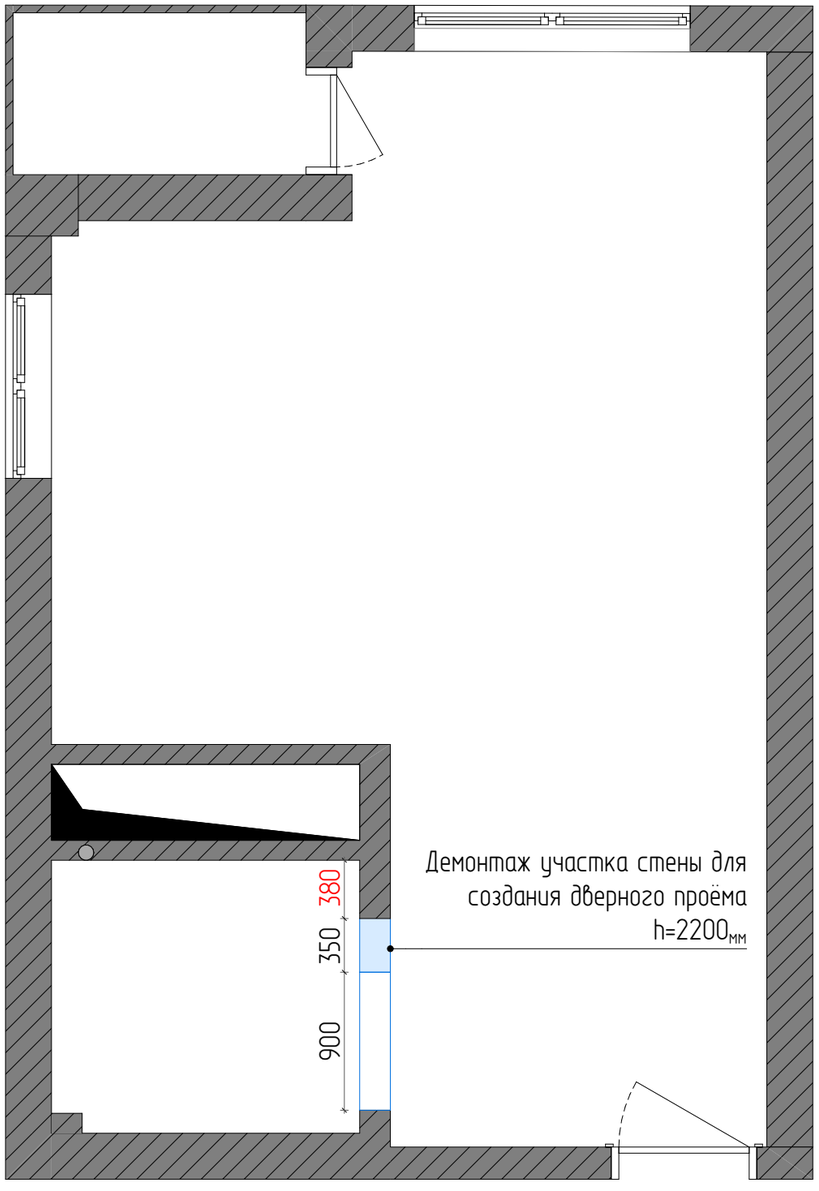

Условные обозначения:


- демонтируемые конструкции
- существующие конструкции

Примечание:

1. Размеры уточнить по месту.
2. Данный лист смотреть совместно со схемой монтажа.

Дизайнер	Шинкевич Екатерина	Дизайн-проект квартиры по адресу:	План демонтажа	Стадия	Лист	Листов
				РП	04	28
телефон	+7 (931) 271-59-56	адрес	Масштаб 1:40	SHEM		

План возводимых перегородок и конструкций

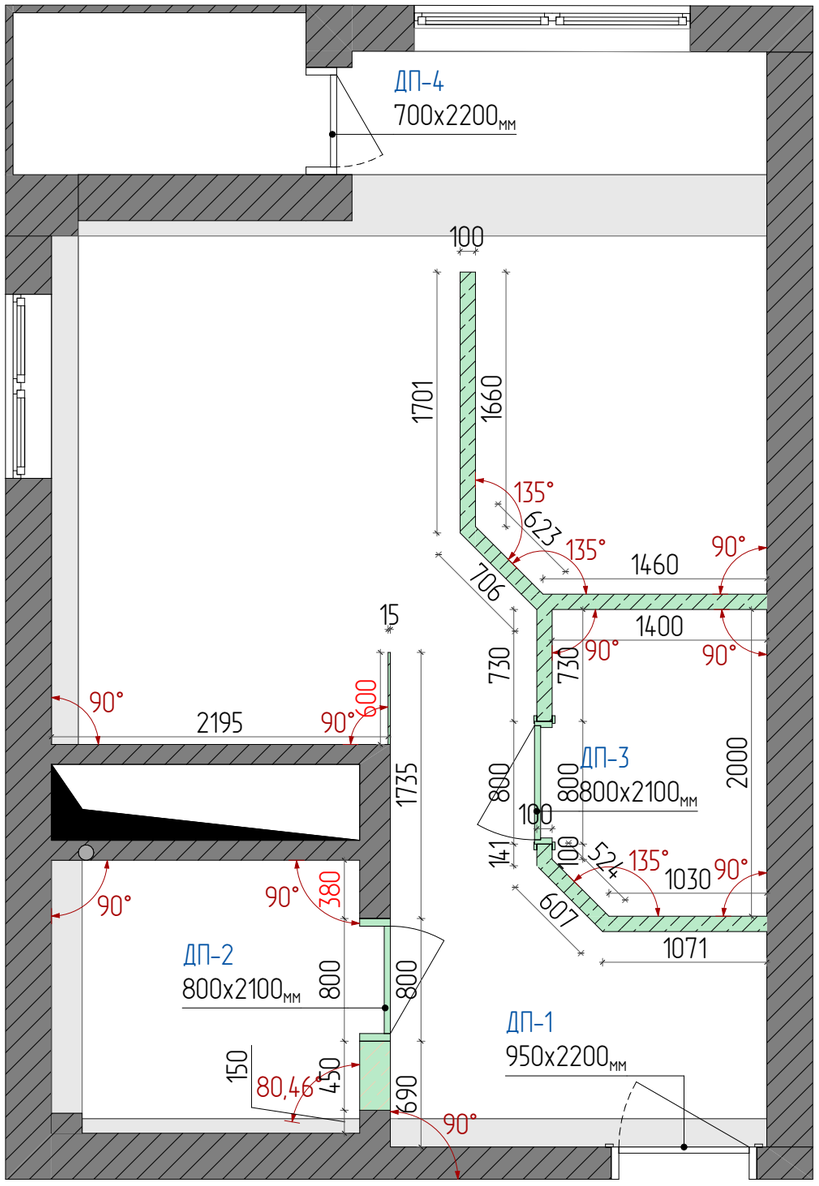

Условные обозначения:


- существующие конструкции
- ригель
- новые конструкции

Примечание:

1. В первую очередь обращать внимание на выносные надписи.
2. Возвести перегородки.
3. Высота всех проемов указана от уровня чистового пола.
4. Указанные стены выровнять под 90 градусов (для точного примыкания ко встроенной мебели).

Дизайнер	Шинкевич Екатерина	Дизайн-проект квартиры по адресу:	План возводимых перегородок и конструкций	Стадия	Лист	Листов
				РП	05	28
телефон	+7 (931) 271-59-56	адрес	Масштаб 1:40	SHEM		

План после перепланировки

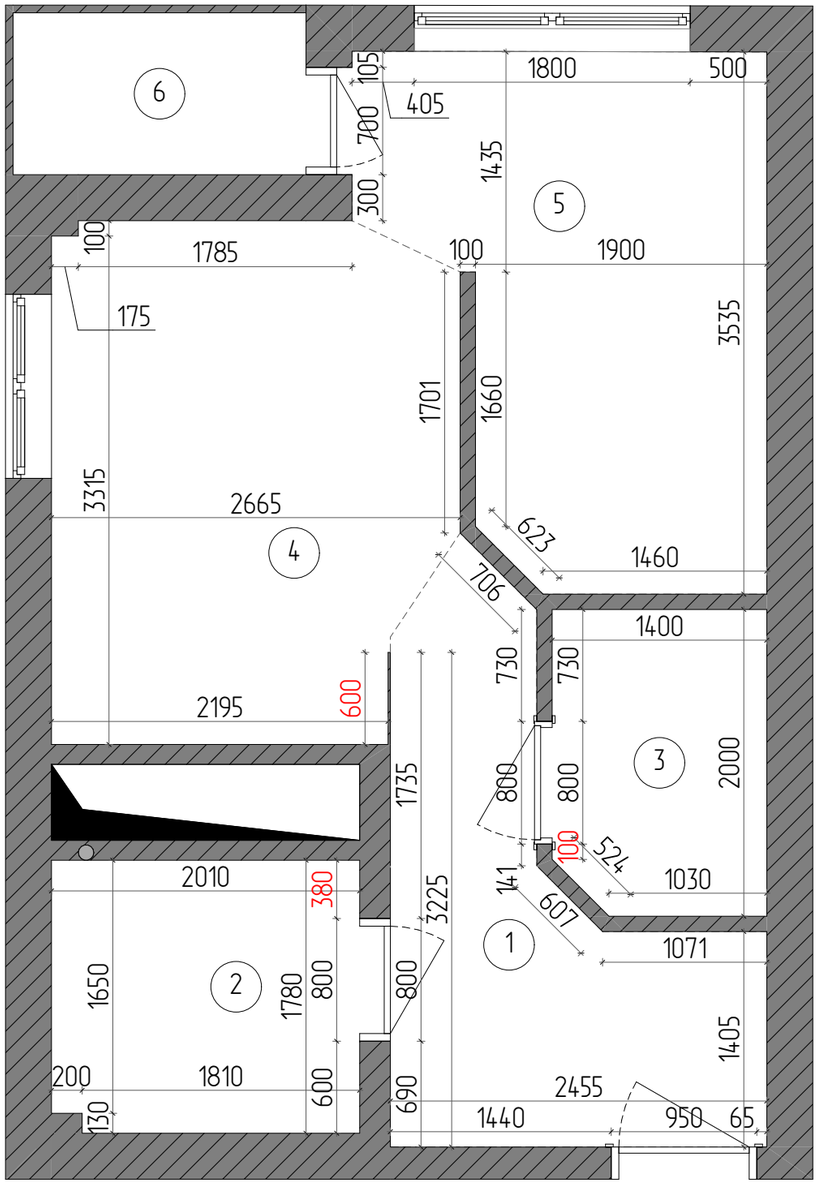


Экспликация помещений		
№	Название помещения	S, кв.м
1	Коридор	5,74
2	Санузел	3,49
3	Гардеробная	2,73
4	Кухня-гостиная	8,48
5	Спальня	7,73
6	Балкон	2,02
		30,19 м²

Примечание:

1. В первую очередь обращать внимание на выносные надписи.
2. Все критичные размеры отмечены красным на чертеже.

Дизайнер	Шинкевич Екатерина	Дизайн-проект квартиры по адресу:	План после перепланировки	Стадия	Лист	Листов
				РП	06	28
телефон	+7 (931) 271-59-56	адрес	Масштаб 1:40	SHEM		


План расстановки мебели

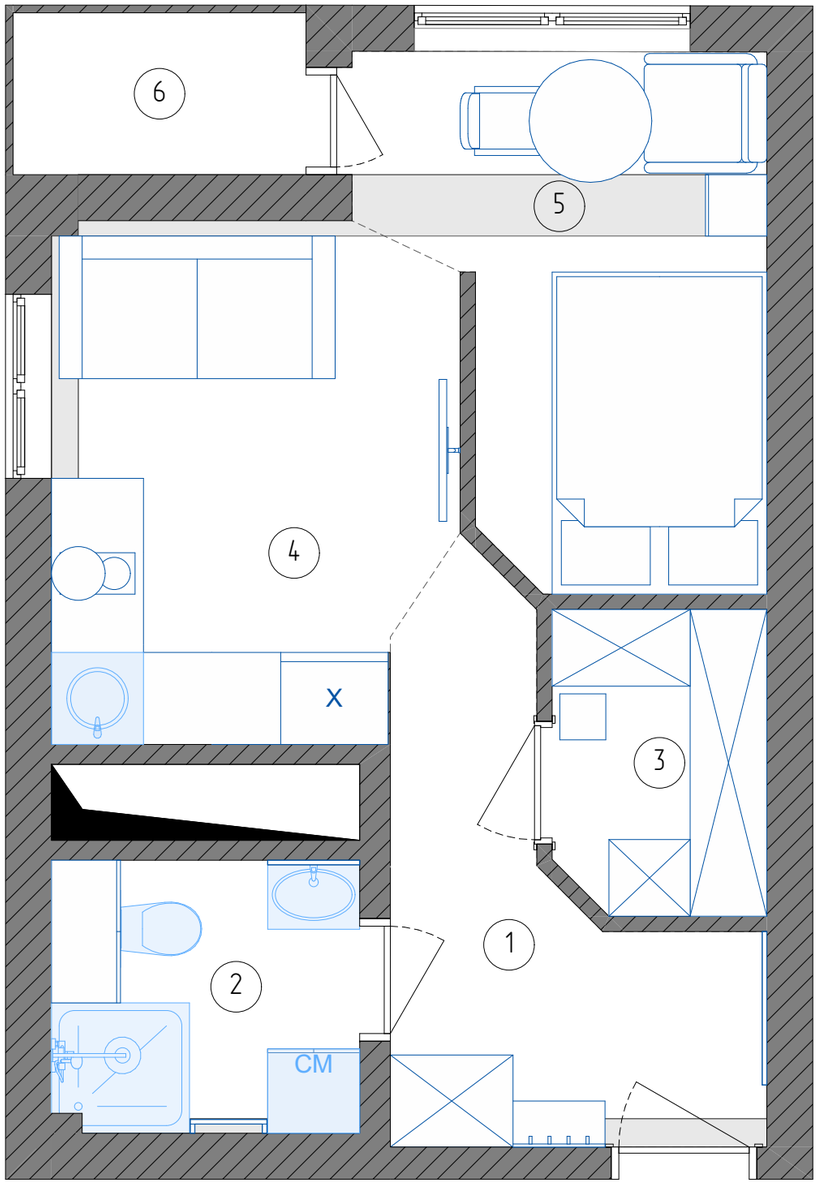

Экспликация помещений		
№	Название помещения	S, кв.м
1	Коридор	5,74
2	Санузел	3,49
3	Гардеробная	2,73
4	Кухня-гостиная	8,48
5	Спальня	7,73
6	Балкон	2,02
		30,19 м²

Дизайнер	Шинкевич Екатерина	Дизайн-проект квартиры по адресу:	План расстановки мебели	Стадия	Лист / Листов
				РП	07 / 28
телефон	+7 (931) 271-59-56	адрес	Масштаб 1:40	SHEM	

План с мебельными размерами и описанием

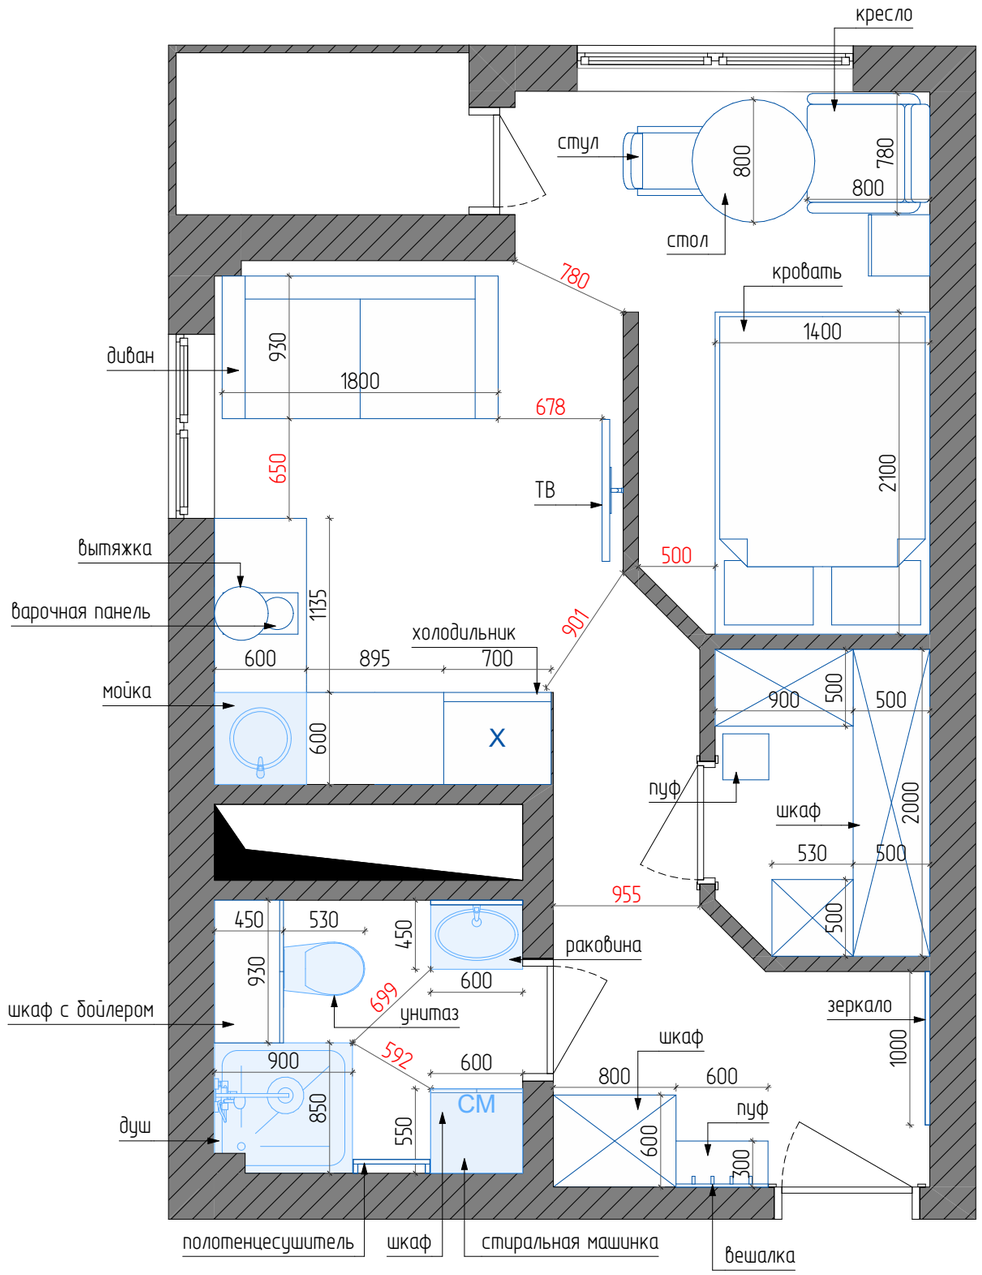


Экспликация помещений		
№	Название помещения	S, кв.м
1	Коридор	5,74
2	Санузел	3,49
3	Гардеробная	2,73
4	Кухня-гостиная	8,48
5	Спальня	7,73
6	Балкон	2,02
		30,19 м²

Примечание:

1. Размеры проходов между стенами и мебелью отмечены красным на чертеже.

Дизайнер	Шинкевич Екатерина	Дизайн-проект квартиры по адресу:	План с мебельными размерами и описанием	Стадия	Лист	Листов
				РП	08	28
телефон	+7 (931) 271-59-56	адрес	Масштаб 1:40	SHEM		

План размещения осветительных приборов, привязка выпусков освещения

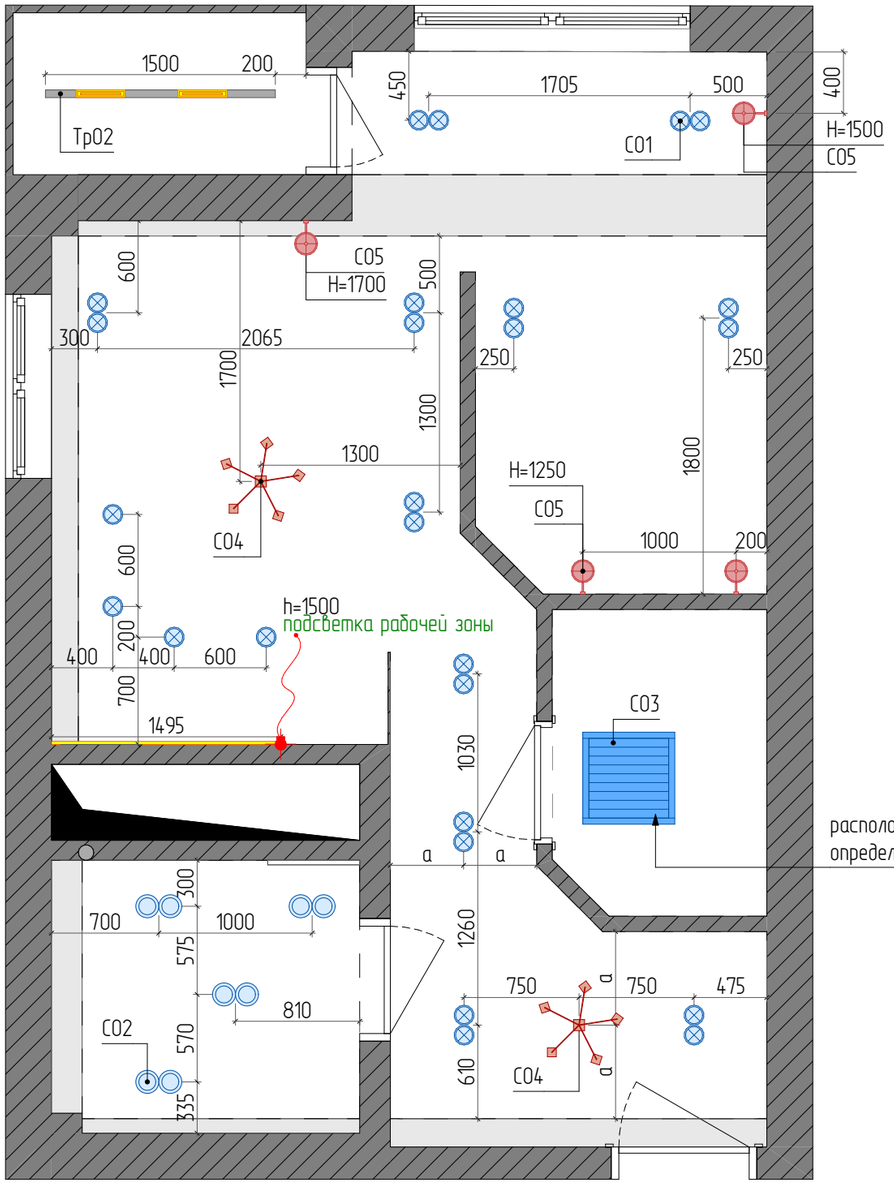

Условное обозначение светильников			
ID	Изображение	Тип светильника	Кол-во
C01		потолочный светильник	26
C02		влагозащитный светильник	8
C03		потолочный светильник	1
C04		люстра	2
C05		бра	4
C06		трековый свтеильник	2

LED лента			
ID	Условное обозначение	Наименование	Длина, мм
C01			1495


Спецификация трека/шинопровода			
ID	Условное обозначение	Наименование	Длина, мм
Тр02		Трек/Шинопровод	1500

Примечание:

1. В первую очередь обращать внимание на выносные надписи.
2. Все размеры даны по осям осветительных приборов.
3. Расположение светодиодных лент смотреть в развертках.

Дизайнер	Шинкевич Екатерина	Дизайн-проект квартиры по адресу:	План размещения осветительных приборов, привязка выпусков освещения	Стадия	Лист	Листов
				РП	09	28
телефон	+7 (931) 271-59-56	адрес	Масштаб 1:40	SHEM		

План выключателей с указанием включения групп светильников

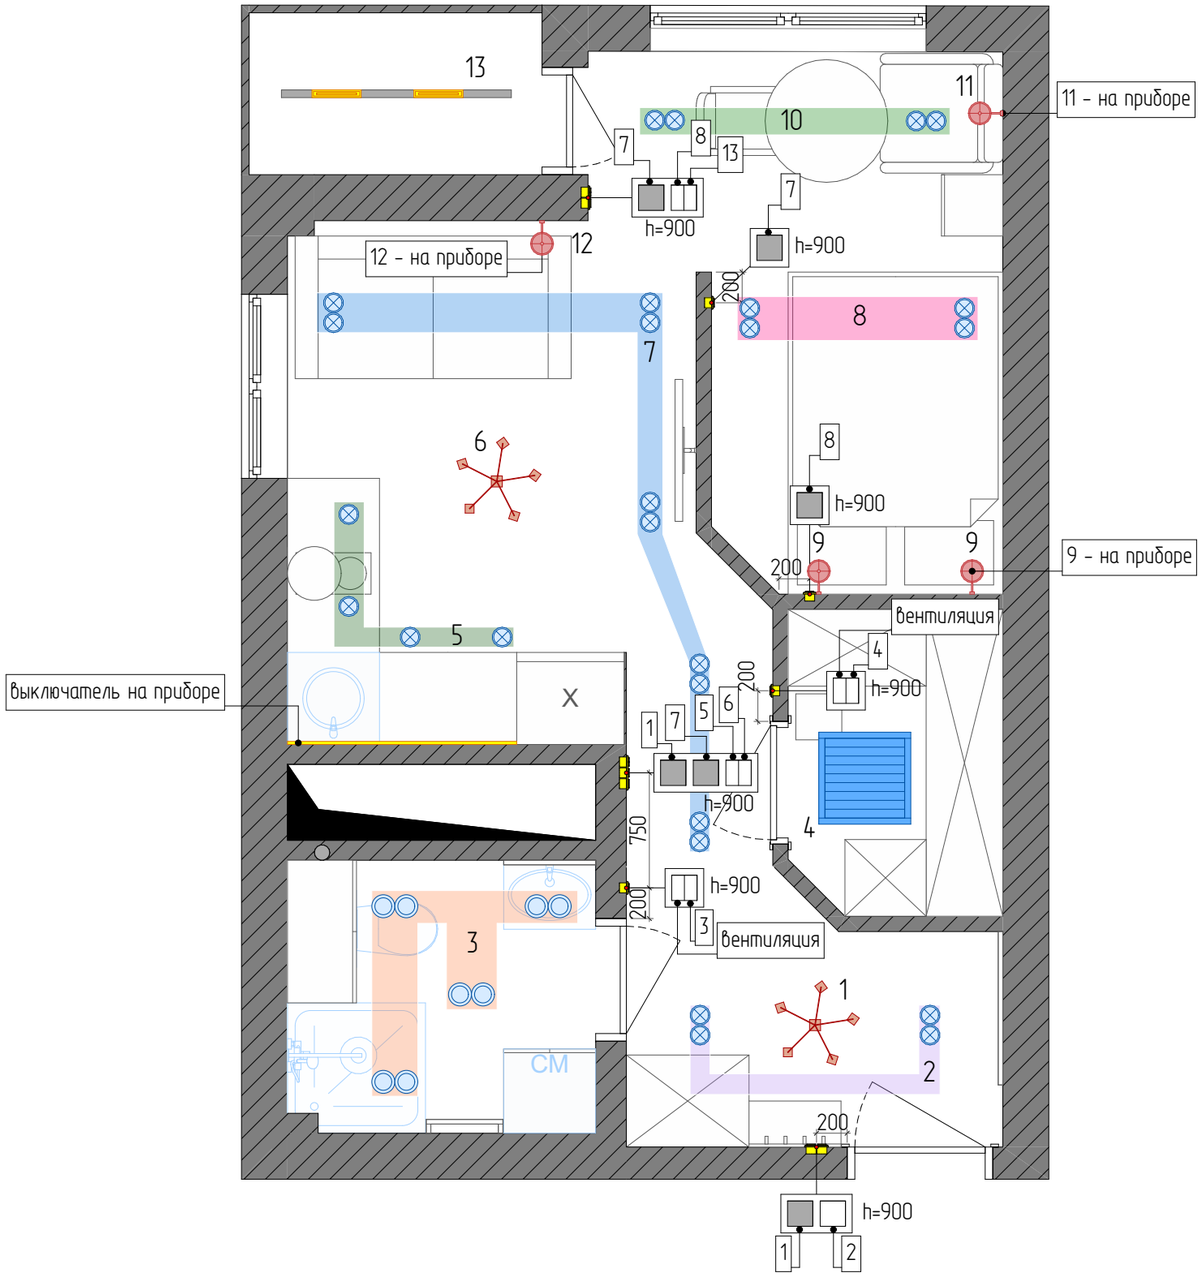

Условное обозначение светильников			
ID	Изображение	Тип светильника	Кол-во
C01		потолочный светильник	26
C02		влагозащитный светильник	8
C03		потолочный светильник	1
C04		люстра	2
C05		бра	4
C06		трековый свтеильник	2


Выключатели		
Условное обозначение	Наименование	Кол-во, шт
	Выключатель двухклавишный	4
	Выключатель одноклавишный проходной	6

Примечание:

1. Выключатели и переключатели разместить на высоте $900_{мм}$ от уровня чистового пола, если не указанно иное.

Дизайнер	Шинкевич Екатерина	Дизайн-проект квартиры по адресу:	План выключателей с указанием включения групп светильников	Стадия	Лист	Листов
				РП	10	28
телефон	+7 (931) 271-59-56	адрес	Масштаб 1:40	SHEM		

План размещения электрических розеток с привязкой размеров

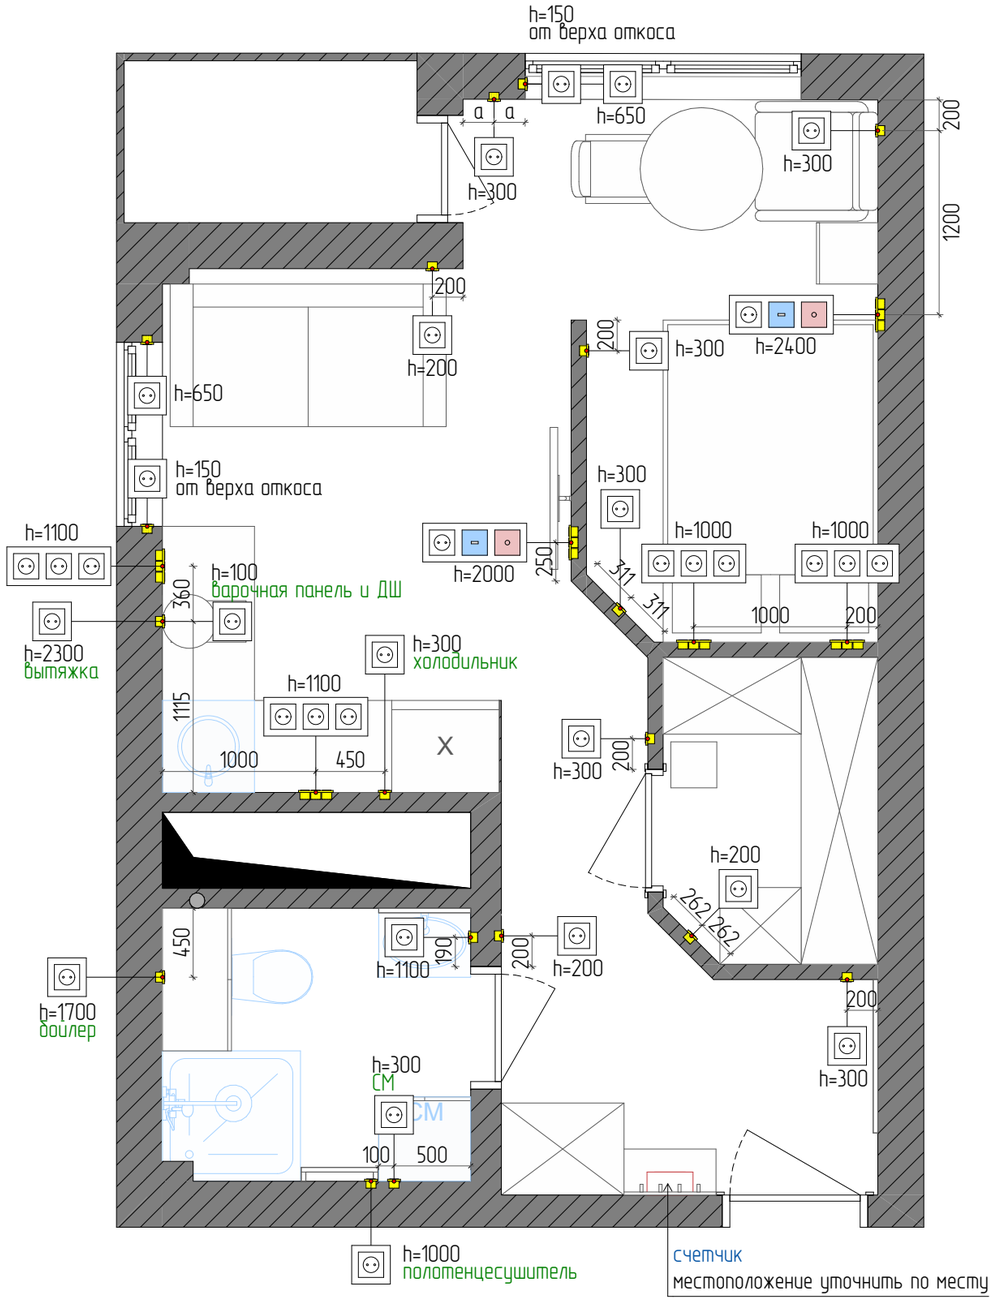

Условное обозначение	Наименование	Кол-во, шт
⊟	Интернет-розетка	2
⊙	Розетка бытовая	34
○	Розетка телевизионная	2


Рамки (общее количество)		
Тип рамки (блока)	Рамка ориентация	Кол-во
Рамка х1	Вертикальная	5
Рамка х1	Горизонтальная	19
Рамка х2	Горизонтальная	2
Рамка х3	Горизонтальная	7

Примечание:

1. В первую очередь, обращать внимание на выносные надписи.
2. Высота розеток 300$_{мм}$ от уровня чистового пола, если не указано иное.
3. Установку рядом стоящих розеток и выключателей произвести под общую рамку.

Дизайнер	Шинкевич Екатерина	Дизайн-проект квартиры по адресу:	План размещения электрических розеток с привязкой размеров	Стадия	Лист	Листов
				РП	11	28
телефон	+7 (931) 271-59-56	адрес	Масштаб 1:40	SHEM		

План потолков с указанием типа используемых материалов

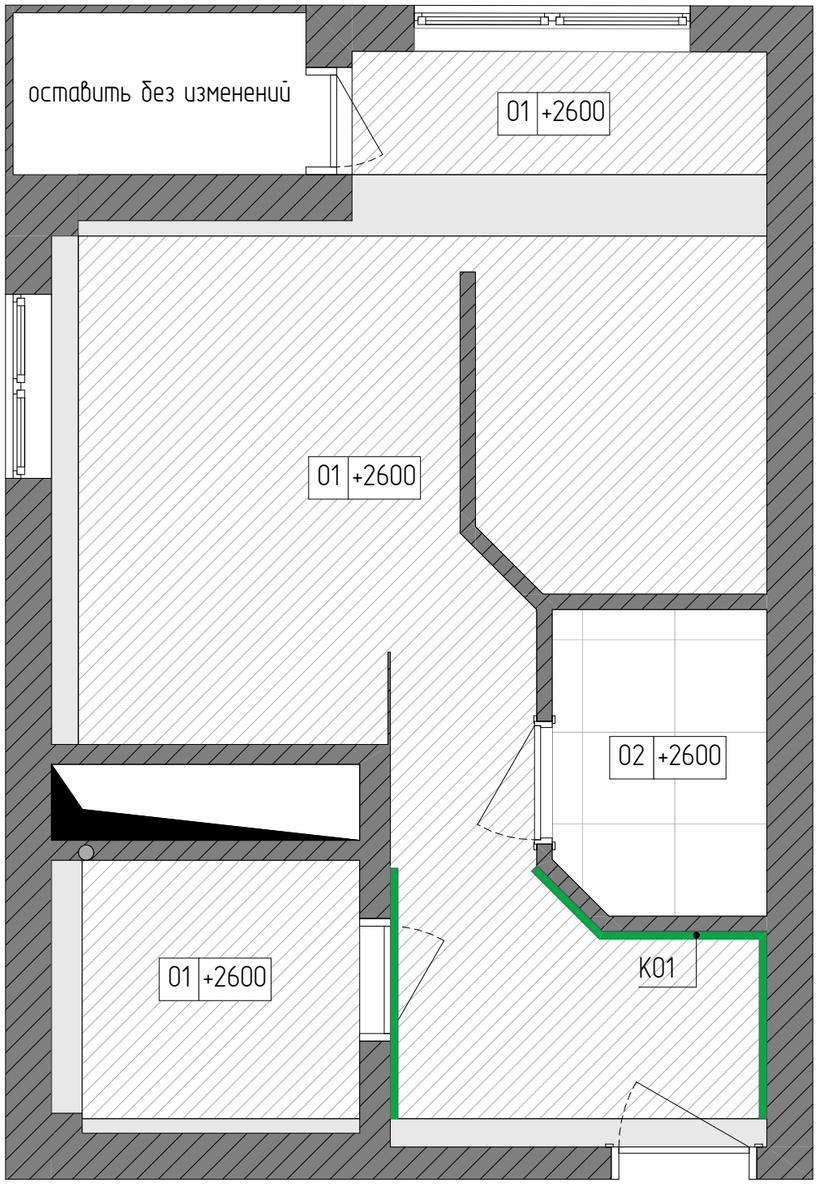

Условные обозначения:

02 – обозначение типа потолка

+2 700 – отметка высоты относительно чистового пола

Ведомость потолков			
ID	Условное обозначение	Наименование	Площадь, кв.м (без запаса)
01		Натяжной потолок	22,65
02		Потолок Армстронг	2,73


Спецификация карниза							
ID	Условное обозначение	Изображение	Наименование	Артикул	Производитель	Длина, мм	Примечание
K01			Карниз	569402703 (ozon.ru)	Де-Багет	4572	60/60

Примечание:

1. За отметку 0,000 принята высота чистового пола.
2. Натяжной потолок опустить на минимальную высоту от самой нижней точки чернового потолка в конкретном помещении.
3. Отметки высот указаны от чистового пола.
4. На развертках все высоты даны от чистового пола.

Дизайнер	Шинкевич Екатерина	Дизайн-проект квартиры по адресу:	План потолков с указанием типа используемых материалов	Стадия	Лист	Листов
				РП	12	28
телефон	+7 (931) 271-59-56	адрес	Масштаб 1:40	SHEM		

План полов с указанием типа напольных покрытий

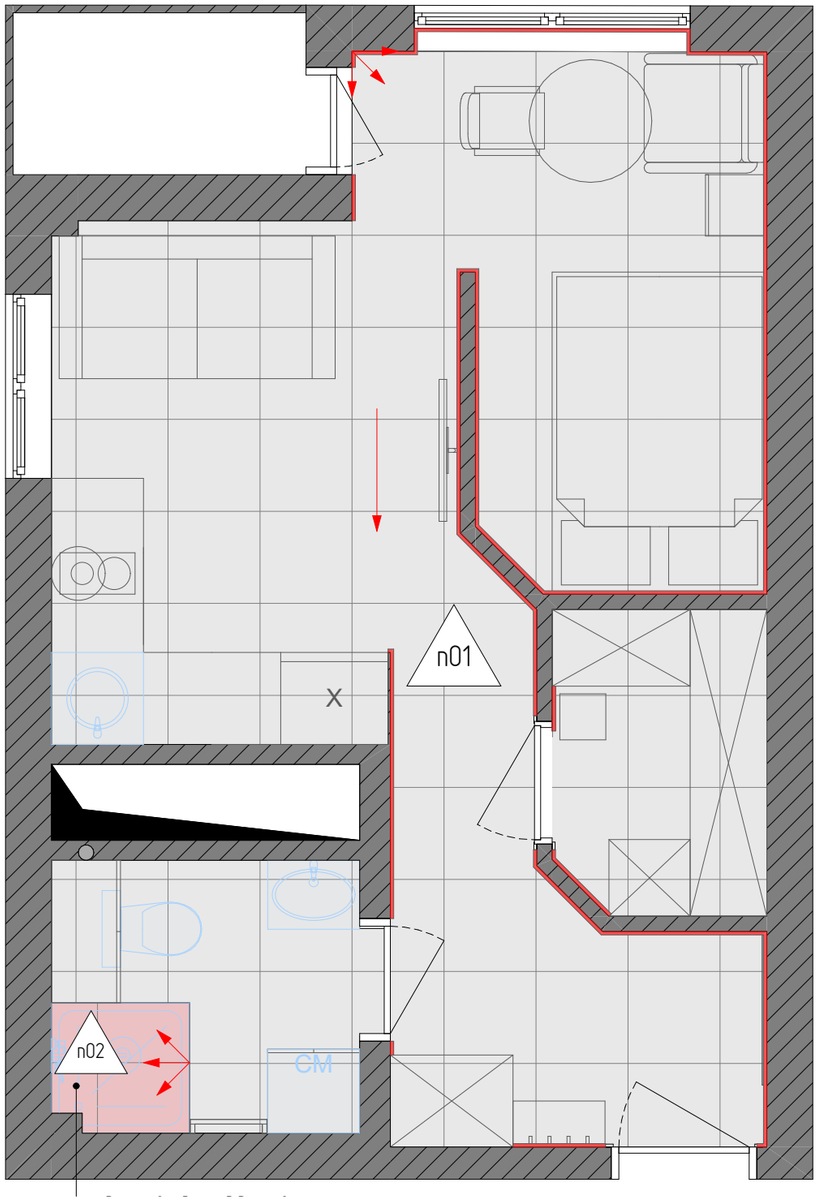

Условные обозначения:

– направление укладки плитки

02 – обозначение типа пола

Напольные покрытия					
ID	Условное обозначение	Наименование	Площадь, кв.м (без запаса)	Примечание	Изображение
п01		Плитка Травертин	27,65	60х60см	
п02		Керамогранит Cray dark shards	0,74	60х60см	


Спецификация плинтуса								
ID	Условное обозначение	Сечение	Изображение	Наименование	Артикул	Производитель	Длина, мм	Примечание
П01		15 мм / 80 мм		Плинтус напольный	555863188 (ozon.ru)		27484	80х15х2000мм

Примечание:

1. Количество материала дано без запаса на подрезку.
2. Привязку стыка напольных покрытий внутри дверных проемов уточнить у поставщика дверей.

Дизайнер	Шинкевич Екатерина	Дизайн-проект квартиры по адресу:	План полов с указанием типа напольных покрытий	Стадия	Лист	Листов
				РП	13	28
телефон	+7 (931) 271-59-56	адрес	Масштаб 1:40	SHEM		

План размещения санитарно-технического оборудования

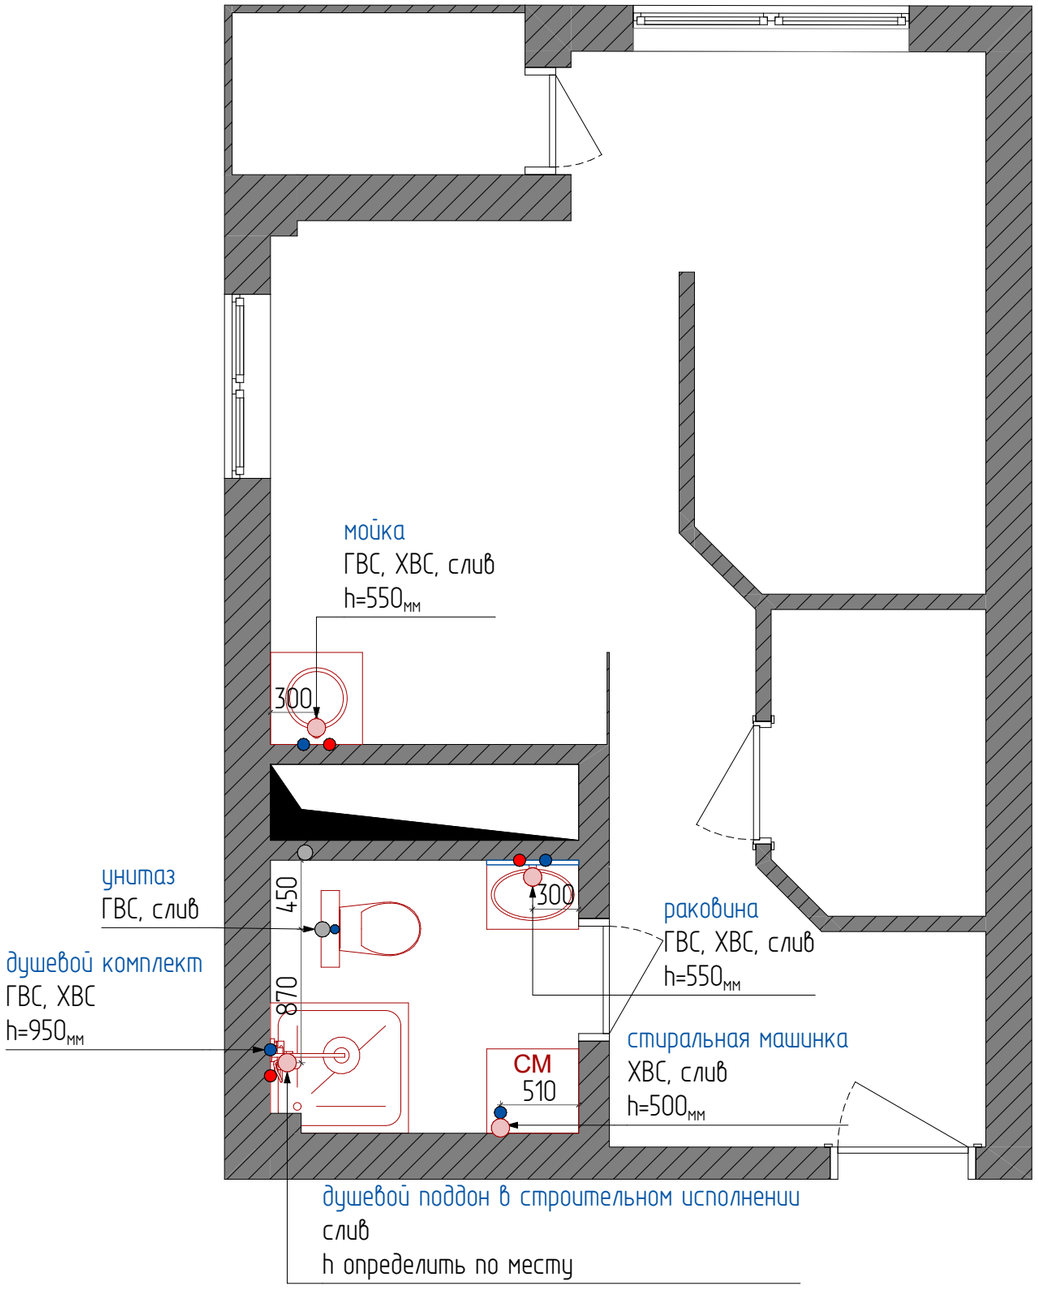

Условные обозначения:


- канализационная труба
- труба подачи горячего водоснабжения
- труба подачи холодного водоснабжения
- размещение стока раковин и сливов

Примечание:

1. Перед началом работ все размеры уточнить по месту.
2. Все размеры даны по конструкциям, без учета плитки и клея.
3. Организовать гидроизоляцию стен и пола в санузле.

Дизайнер	Шинкевич Екатерина	Дизайн-проект квартиры по адресу:	План размещения санитарно-технического оборудования	Стадия	Лист	Листов
				РП	14	28
телефон	+7 (931) 271-59-56	адрес	Масштаб 1:40	SHEM		

План расположения систем отопления и вентиляции

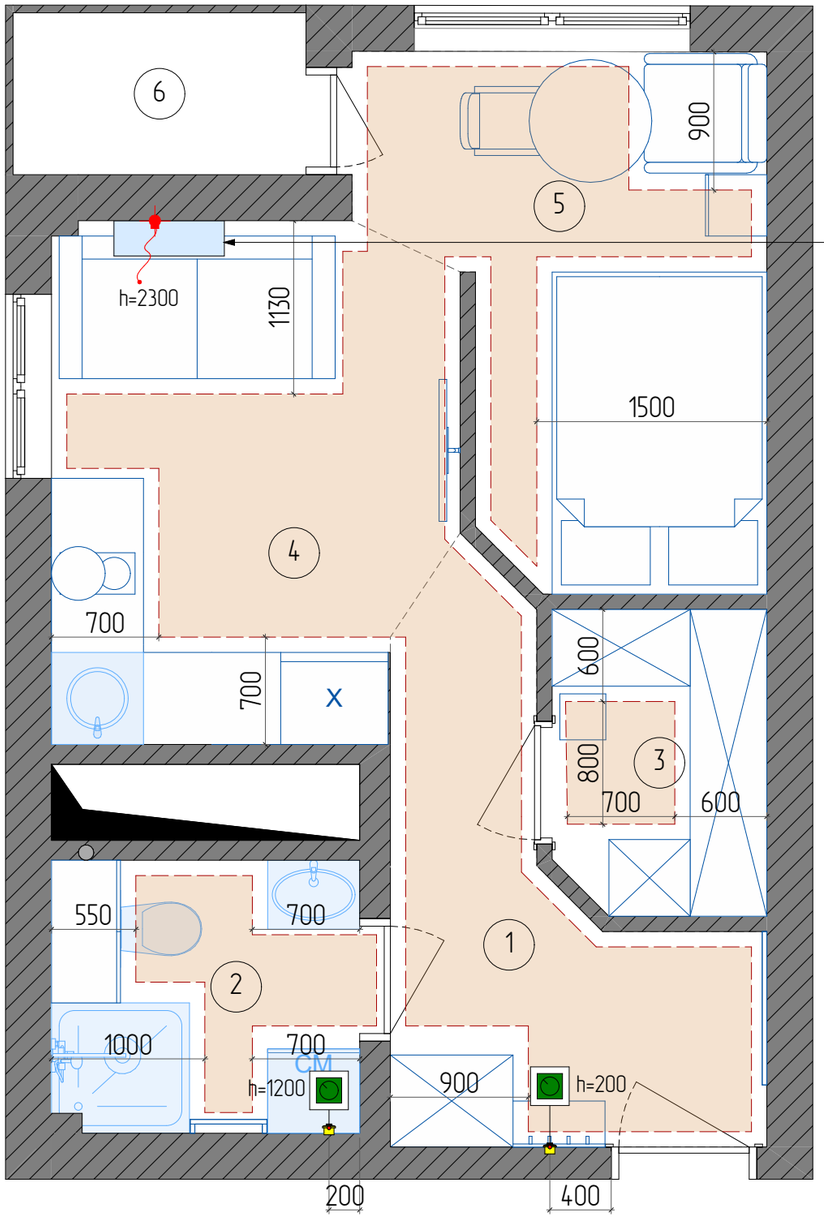

сплит-систему отцентровать относительно простенка, установить вплотную к потолочному плинтусу
$H_{верха\ сплита}$=2390$_{мм}$

Условные обозначения:

– сплит-система

Теплый пол		
Условное обозначение	Наименование	Площадь, кв.м
	Тёплый пол	12,71
		12,71 м²

Регулятор тёплого пола		
Условное обозначение	Наименование	Кол-во, шт
	Регулятор теплого пола	2


Экспликация помещений		
№	Название помещения	S, кв.м
1	Коридор	5,74
2	Санузел	3,49
3	Гардеробная	2,73
4	Кухня-гостиная	8,48
5	Спальня	7,73
6	Балкон	2,02
		30,19 м²

Примечание:

1. Сплит-систему отцентровать относительно отделки и установить вплотную к потолочному плинтусу.
2. Тёплый пол смонтировать с отступом от стен и мебели 100$_{мм}$.

Дизайнер	Шинкевич Екатерина	Дизайн-проект квартиры по адресу:	План расположения систем отопления и вентиляции	Стадия	Лист	Листов
				РП	15	28
телефон	+7 (931) 271-59-56	адрес	Масштаб 1:40	SHEM		


План отделочных материалов по стенам

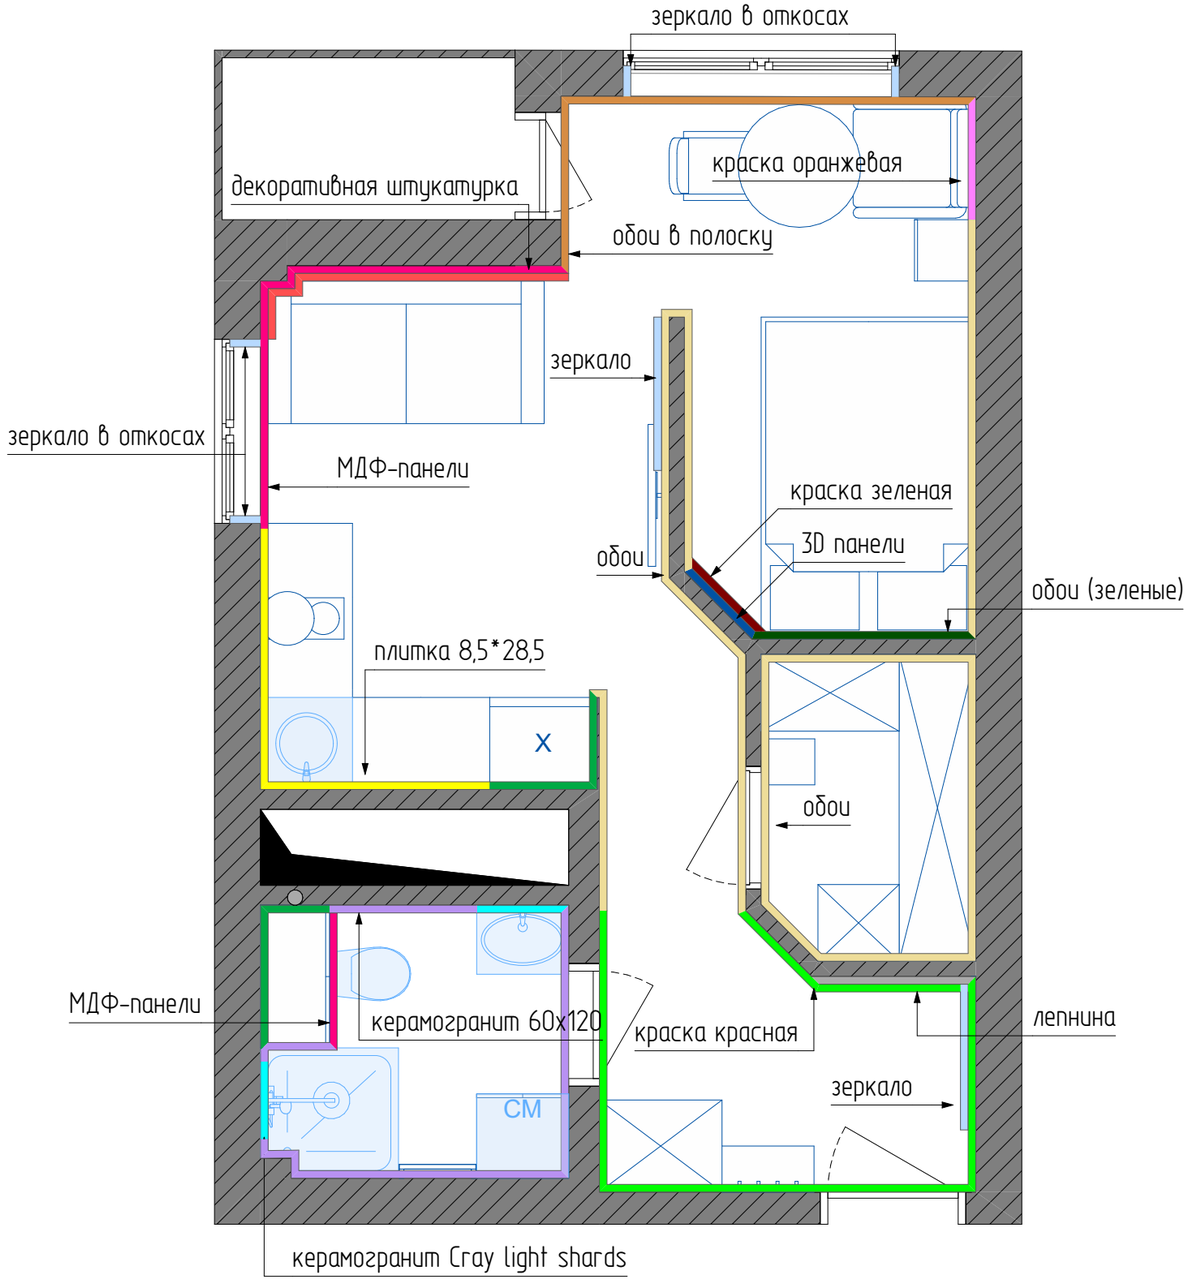



Условное обозначение	Наименование
	3D панели
	декоративная штукатурка
	зеркало
	керамогранит 60х120
	керамогранит Cray light shards
	краска белая
	краска зеленая
	краска красная
	краска оранжевая
	лепнина
	МДФ-панели
	обои
	обои (зеленые)
	обои в полоску
	плитка 8,5*28,5


Дизайнер	Шинкевич Екатерина	Дизайн-проект квартиры по адресу:	План отделочных материалов по стенам	Стадия	Лист	Листов
				РП	16	28
телефон	+7 (931) 271-59-56	адрес	Масштаб 1:40	SHEM		


Развертки по стенам. Коридор, кухня, спальня

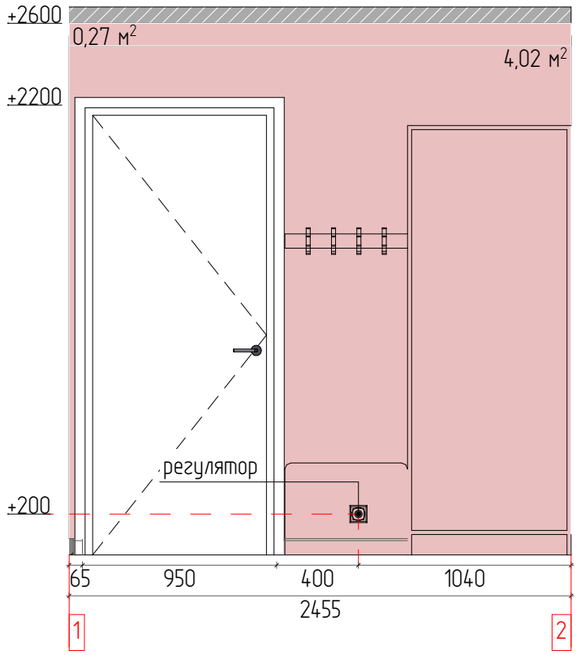


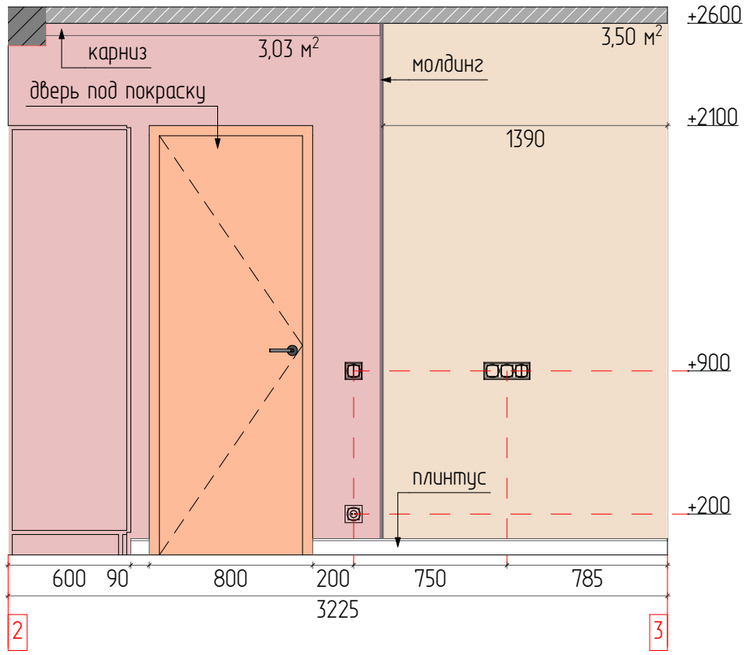


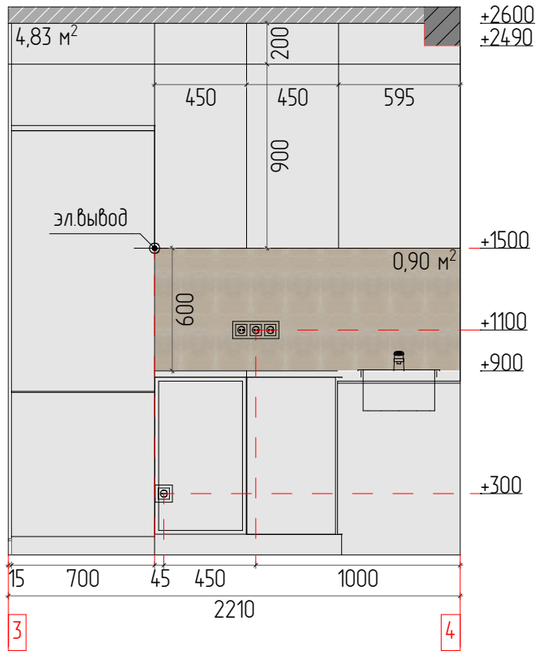

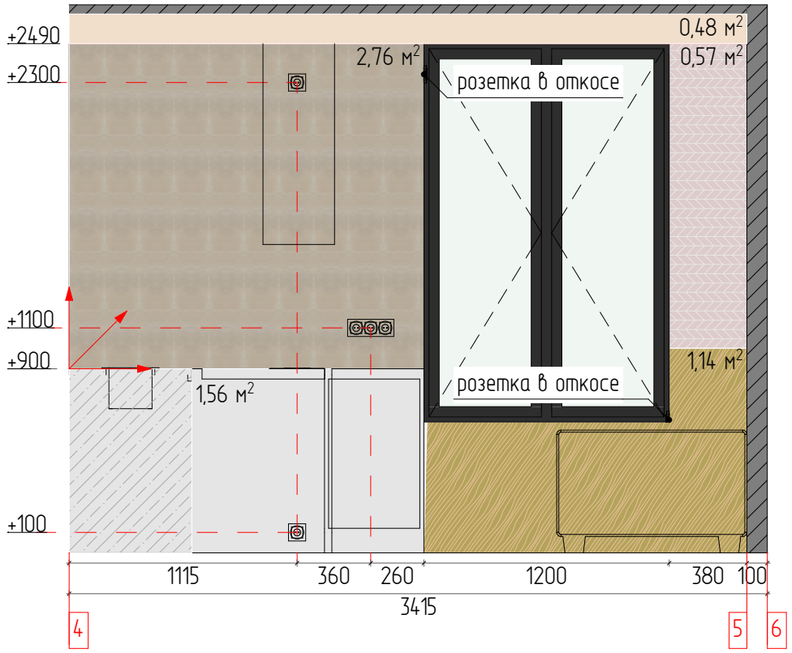

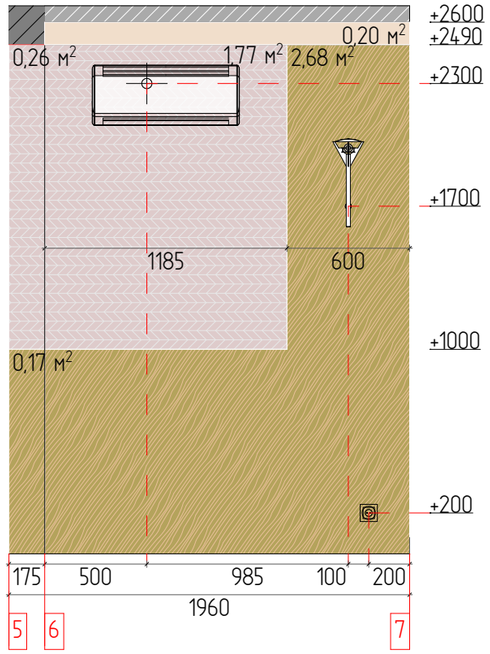

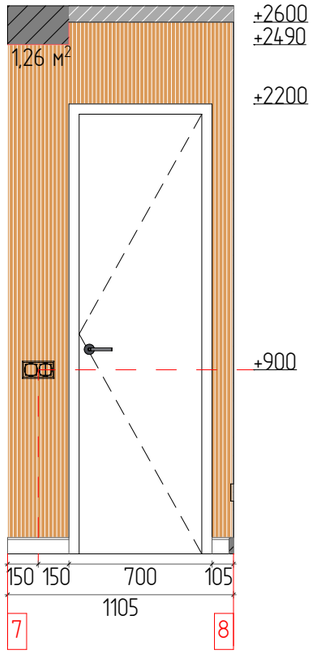

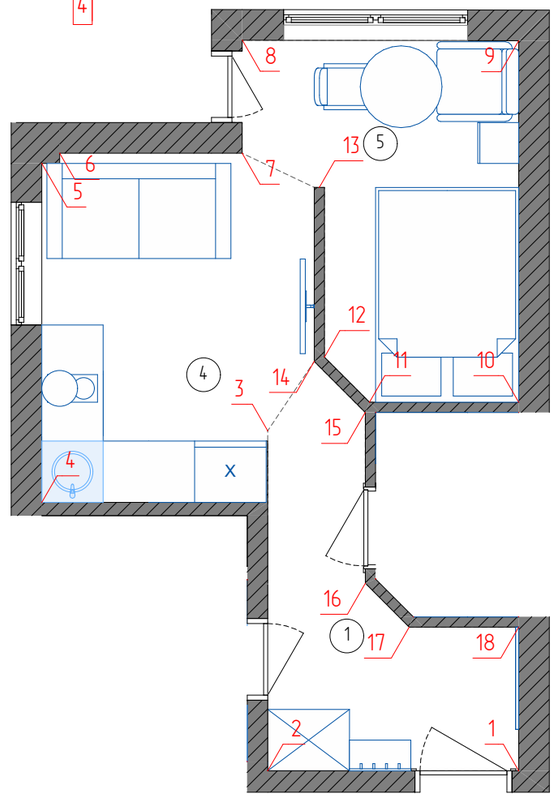


Примечание:


1. Количество материала для отделки стен дано без запаса.
2. Пересчитать все материалы перед заказом с менеджером бренда (используя данные проекта).


Дизайнер	Шинкевич Екатерина	Дизайн-проект квартиры по адресу:	Развертки по стенам. Коридор, кухня, спальня	Стадия	Лист	Листов
телефон	+7 (931) 271-59-56	адрес	Масштаб 1:60, 1:30	РП	17	28


SHEM


Развертки по стенам. Коридор, кухня, спальня

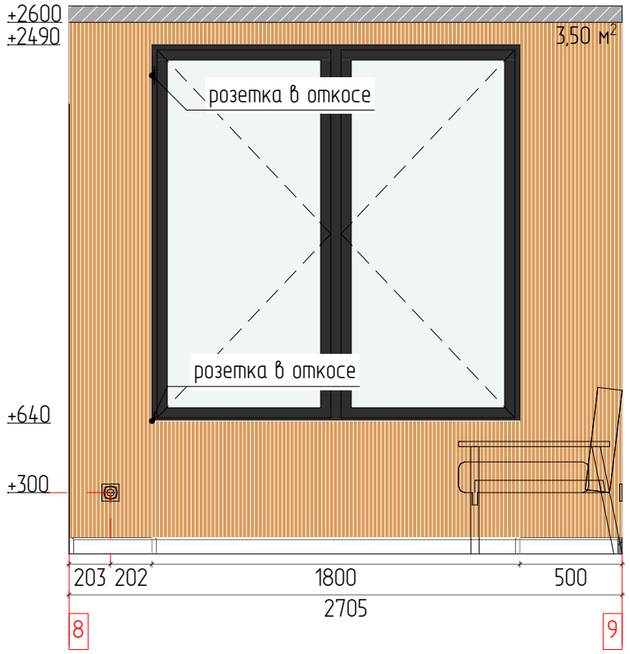

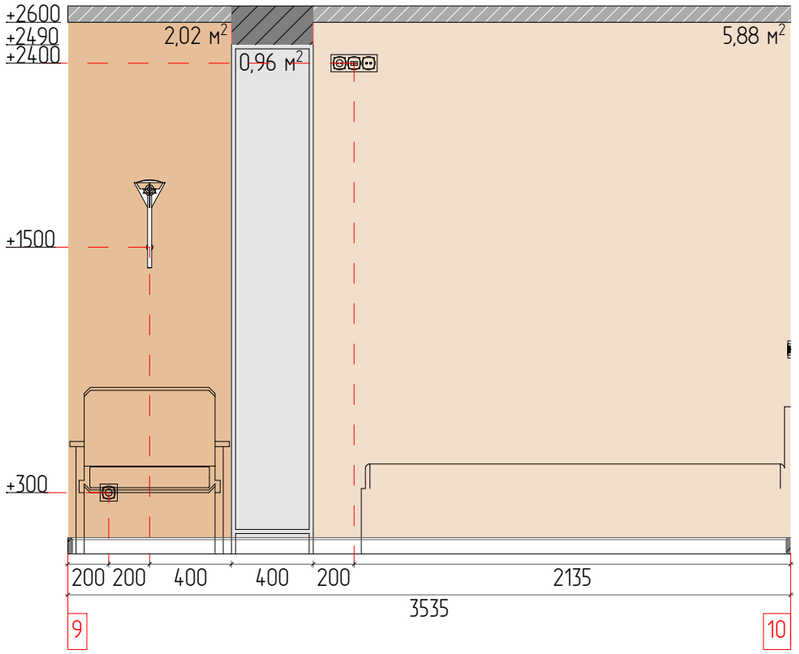

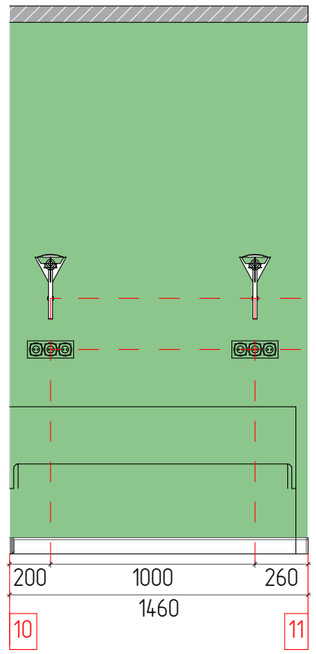

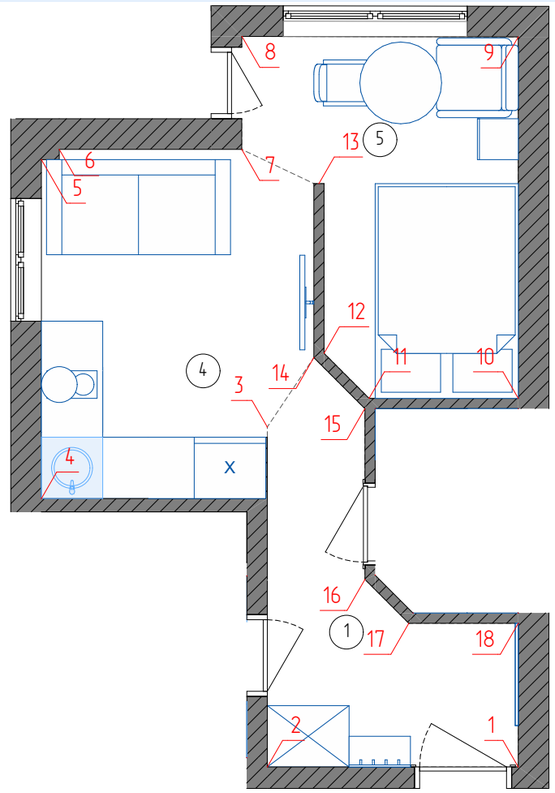

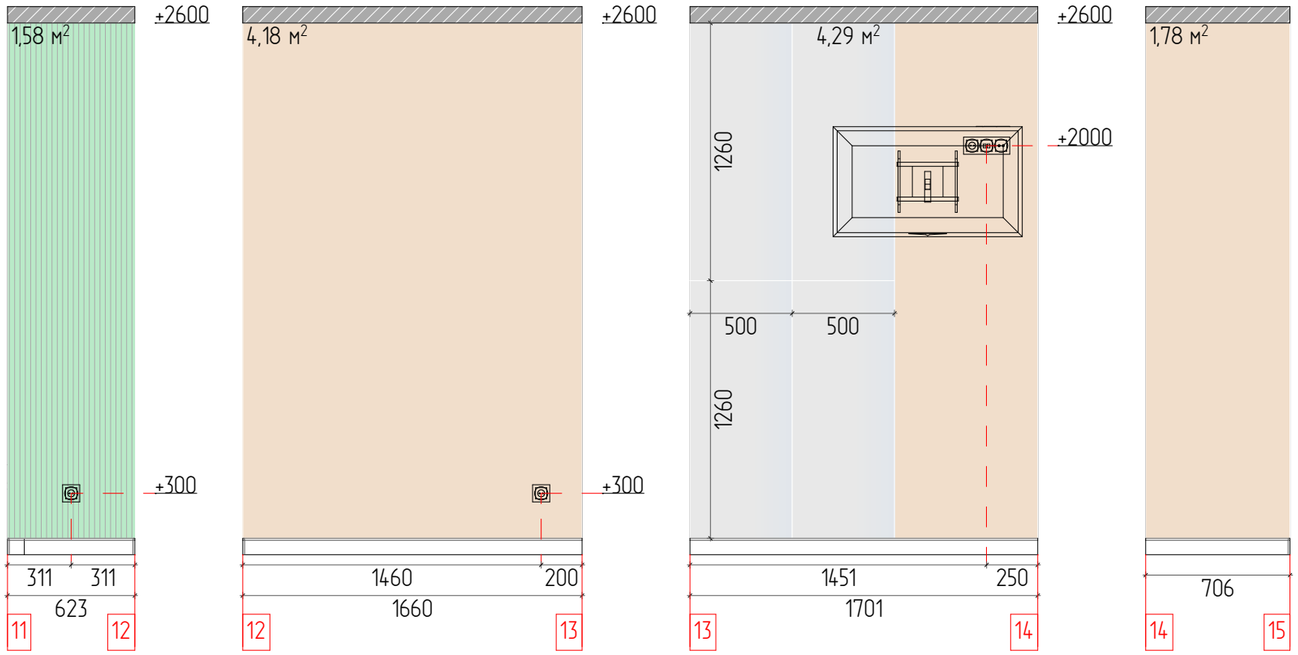

Расход материалов. Коридор, кухня, спальня


Наименование	Условное обозначение	Площадь, кв.м (без запаса)	Примечание
3D панели Decor Dizayn DD910		1,58	под покраску
Декоративная штукатурка		2,60	подбирается с дизайнером
Зеркала		1,56	1260х500мм
Керамическая плитка Керама Марацци Тракай бежевый		3,64	8.5*28.5, светлый глянцевый
Краска белая		7,41	за мебелью
Краска зелёная		1,58	под покраску
Краска красная		18,96	подбирается с дизайнером
Краска оранжевая		2,08	подбирается с дизайнером
МДФ-панель		3,99	
Обои		15,44	подбирается с дизайнером
Обои		2,45	
Обои (зелёные)		3,79	подбирается с дизайнером
Обои полосатые Andrea Rossi Spectrum Max 54365-3		5,01	артикул: 54365-3


Примечание:

1. Количество материала для отделки стен дано без запаса.
2. Пересчитать все материалы перед заказом с менеджером бренда (используя данные проекта).

Дизайнер	Шинкевич Екатерина	Дизайн-проект квартиры по адресу:	Развертки по стенам. Коридор, кухня, спальня	Стадия	Лист	Листов
				РП	18	28
телефон	+7 (931) 271-59-56	адрес	Масштаб 1:30, 1:60	SHEM		

Развертки по стенам. Коридор, кухня, спальня

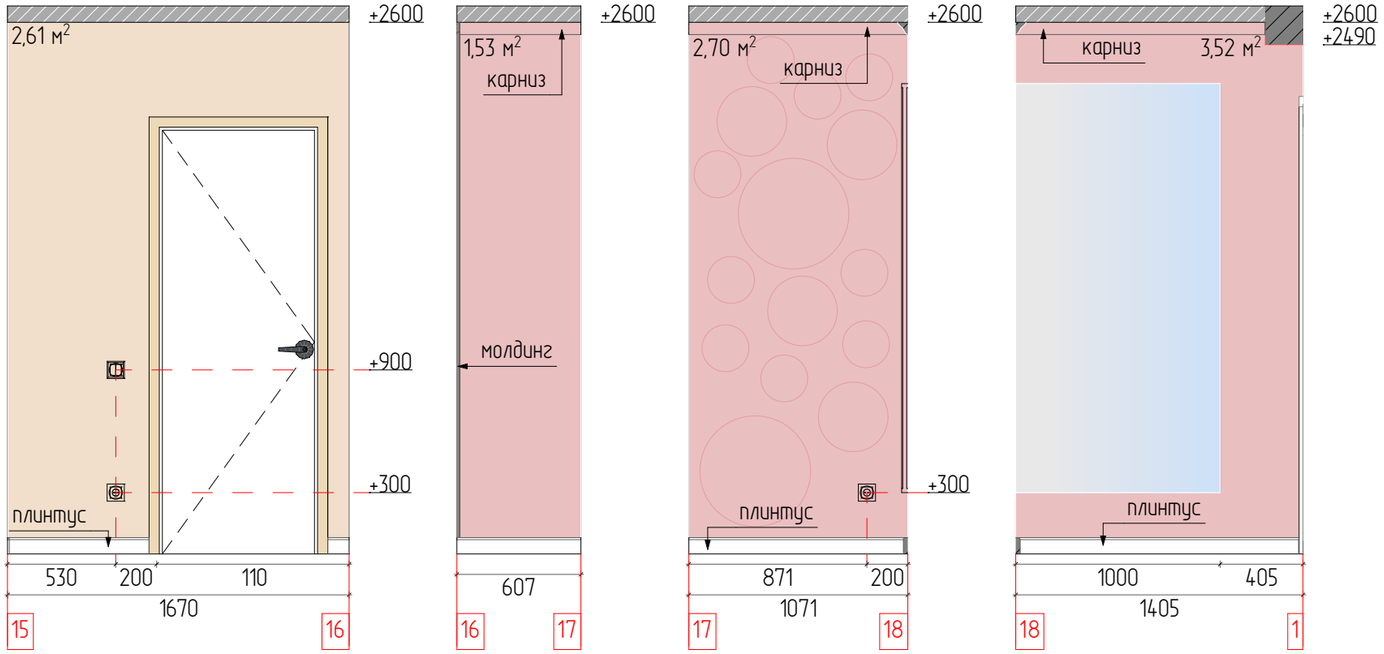

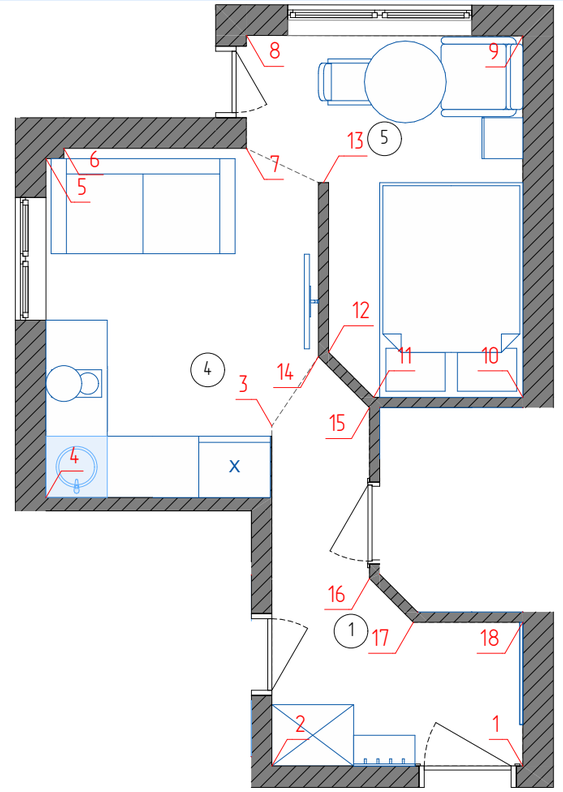

Расход материалов. Коридор, кухня, спальня


Наименование	Условное обозначение	Площадь, кв.м (без запаса)	Примечание
3D панели Decor Dizayn DD910		1,58	под покраску
Декоративная штукатурка		2,60	подбирается с дизайнером
Зеркала		1,56	1260х500мм
Керамическая плитка Керама Марацци Тракай бежевый		3,64	8.5*28.5, светлый глянцевый
Краска белая		7,41	за мебелью
Краска зелёная		1,58	под покраску
Краска красная		18,96	подбирается с дизайнером
Краска оранжевая		2,08	подбирается с дизайнером
МДФ-панель		3,99	
Обои		15,44	подбирается с дизайнером
Обои		2,45	
Обои (зелёные)		3,79	подбирается с дизайнером
Обои полосатые Andrea Rossi Spectrum Max 54365-3		5,01	артикул: 54365-3


Примечание:


1. Количество материала для отделки стен дано без запаса.
2. Пересчитать все материалы перед заказом с менеджером бренда (используя данные проекта).


Дизайнер	Шинкевич Екатерина	Дизайн-проект квартиры по адресу:	Развертки по стенам. Коридор, кухня, спальня	Стадия	Лист	Листов
				РП	19	28
телефон	+7 (931) 271-59-56	адрес	Масштаб 1:30, 1:60	SHEM		


Развертки по стенам. Санузел

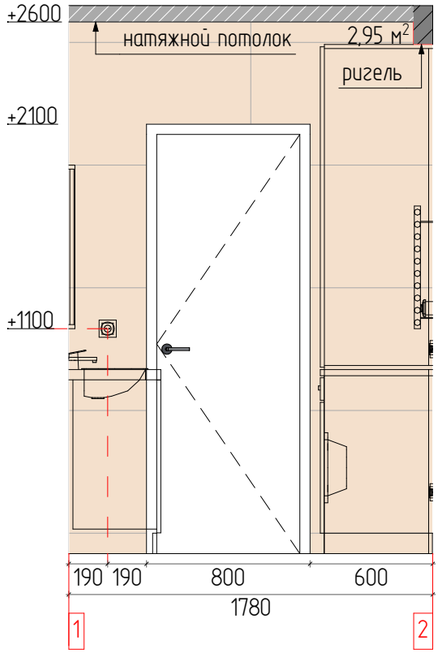

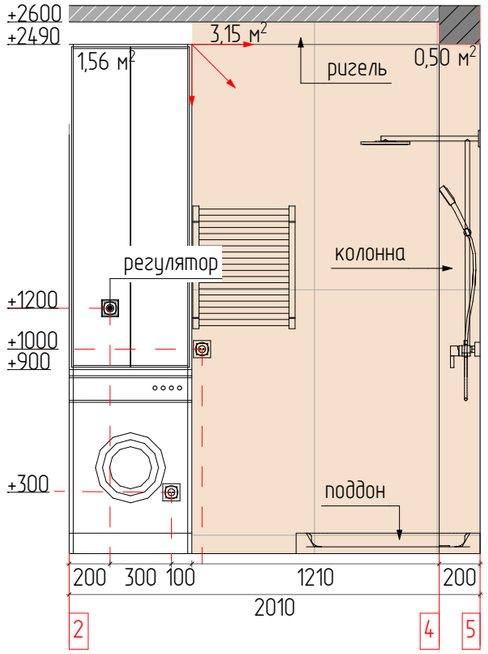

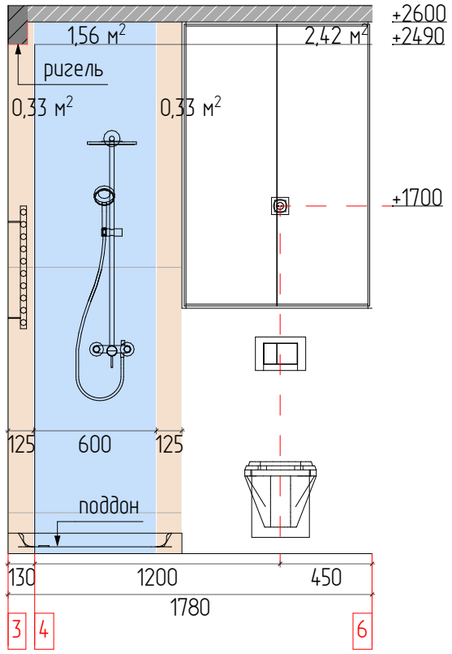

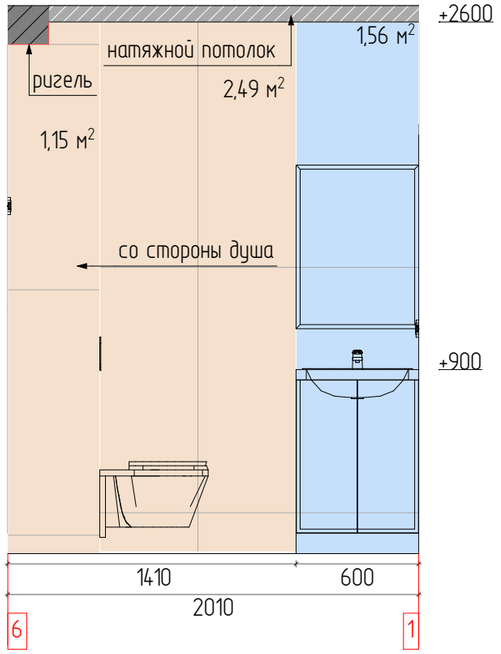

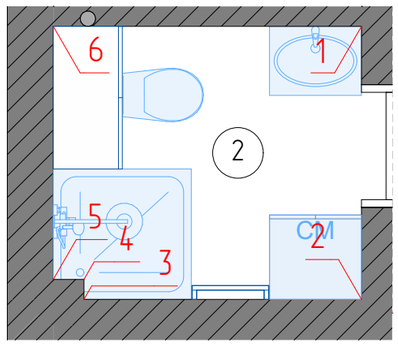


Расход материалов. Санузел			
Наименование	Условное обозначение	Площадь, кв.м (без запаса)	Примечание
Керамогранит		14,91	60х120см
Керамогранит Cray light shards		3,12	60х60см
Покраска		2,50	


Примечание:

1. Количество материала для отделки стен дано без запаса.
2. Пересчитать все материалы перед заказом с менеджером бренда (используя данные проекта).

Дизайнер	Шинкевич Екатерина	Дизайн-проект квартиры по адресу:	Развертки по стенам. Санузел	Стадия	Лист	Листов
				РП	20	28
телефон	+7 (931) 271-59-56	адрес	Масштаб 1:40, 1:30	SHEM		

Развертки по стенам. Гардеробная

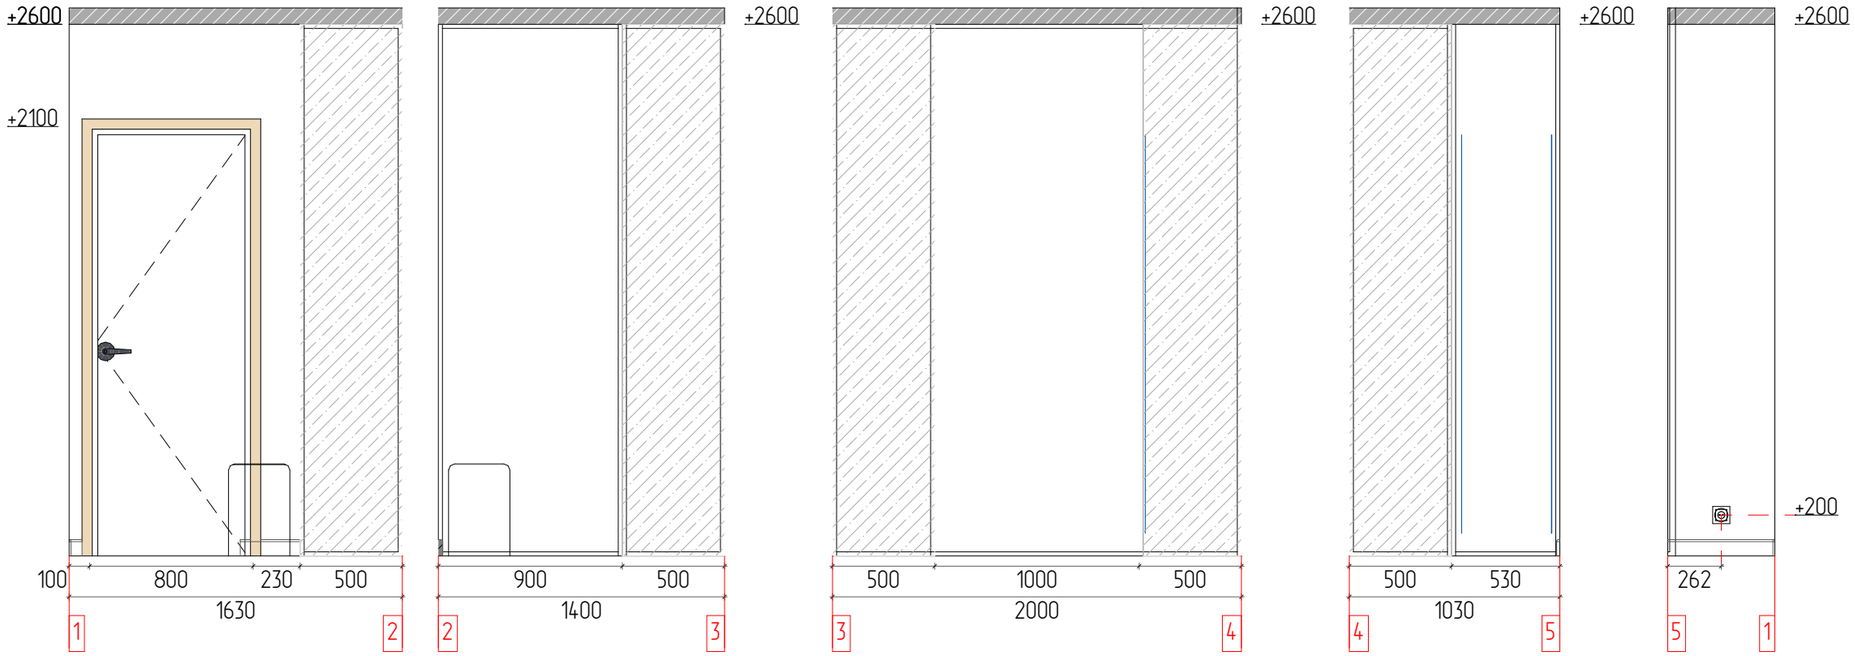

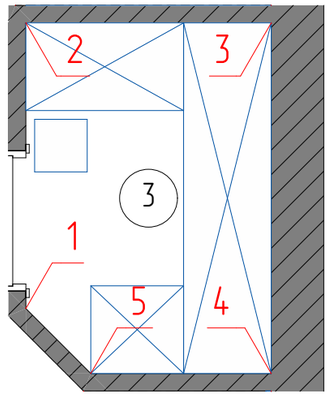


Расход материалов. Гардеробная			
Наименование	Условное обозначение	Площадь, кв.м (без запаса)	Примечание
Обои		15,65	

Примечание:

1. Количество материала для отделки стен дано без запаса.
2. Пересчитать все материалы перед заказом с менеджером бренда (используя данные проекта).

Дизайнер	Шинкевич Екатерина	Дизайн-проект квартиры по адресу:	Развертки по стенам. Гардеробная	Стадия	Лист	Листов
				РП	21	28
телефон	+7 (931) 271-59-56	адрес	Масштаб 1:35, 1:30	SHEM		

Ниша за диваном

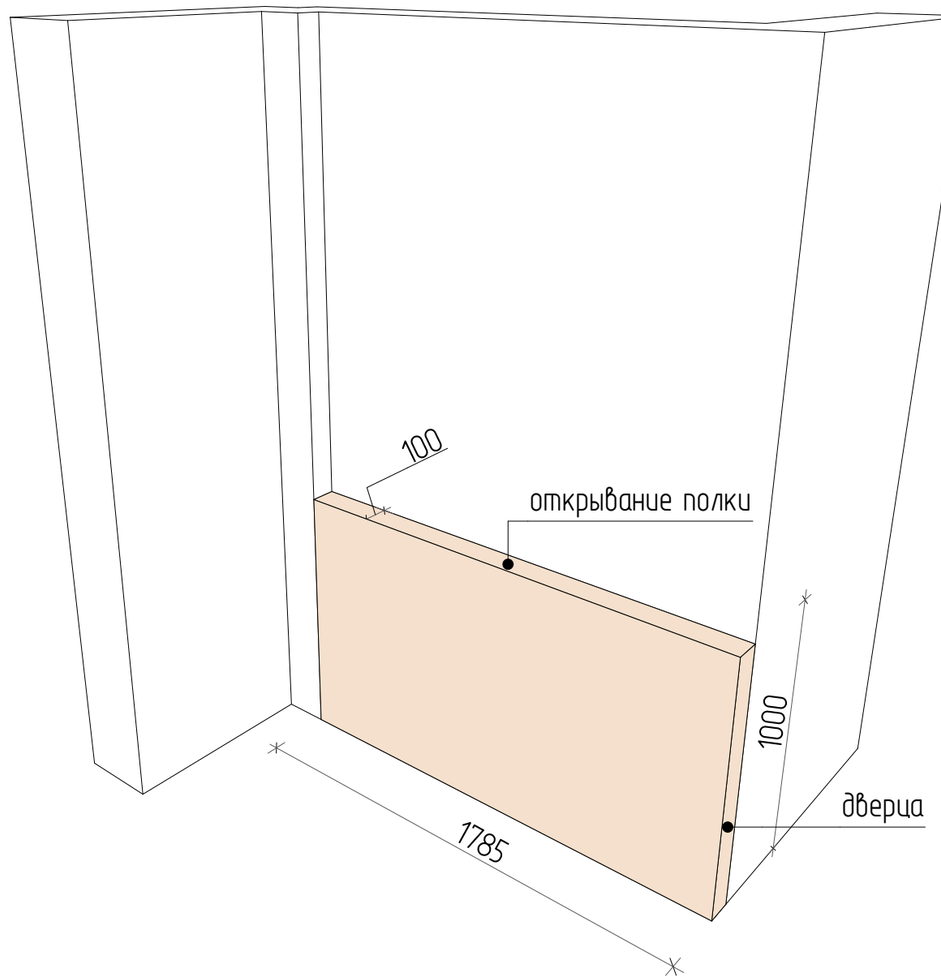

Примечание:

1. Точные размеры всех изделий по индивидуальным заказам уточняются по факту специалистом-исполнителем.
2. Мебельные ручки выбираются совместно с дизайнером.

Дизайнер	Шинкевич Екатерина	Дизайн-проект квартиры по адресу:	Ниша за диваном	Стадия: РП	Лист: 22 / Листов: 28
телефон	+7 (931) 271-59-56	адрес	Масштаб 1:177,25	SHEM	

Спецификация отделочных материалов стен		
Наименование	Площадь, кв.м (без запаса)	Примечание
3D панели Decor Dizayn DD910	1,58	под покраску
Декоративная штукатурка	2,60	подбирается с дизайнером
Зеркала	1,56	1260х500мм
Керамическая плитка Керама Марацци Тракай бежевый	3,64	8.5*28.5, светлый глянцевый
Керамогранит	14,91	60х120см
Керамогранит Cray light shards	3,12	60х60см
Краска белая	7,41	за мебелью
Краска зелёная	1,58	под покраску
Краска красная	18,96	подбирается с дизайнером
Краска оранжевая	2,08	подбирается с дизайнером
МДФ-панель	3,99	
Обои	15,44	подбирается с дизайнером
Обои	18,10	
Обои (зелёные)	3,79	подбирается с дизайнером
Обои полосатые Andrea Rossi Spectrum Max 54365-3	5,01	артикул: 54365-3
Покраска	2,50	

Спецификация карнизов/молдингов/плинтусов					
ID	Наименование	Артикул	Производитель	Длина, мм	Примечание
К01	Карниз	569402703 (ozon.ru)	Де-Багет	4572	60/60
М01	Молдинг	1142089436 (ozon.ru)		5040	20х10 мм
П01	Плинтус напольный	555863188 (ozon.ru)		27224	80х15х2000мм

Спецификация потолков и пола			
ID	Наименование	Площадь, кв.м (без запаса)	Примечание
01	Натяжной потолок	22,65	
02	Потолок Армстронг	2,73	
п01	Плитка Травертин	27,65	60х60см
п02	Керамогранит Cray dark shards	0,74	60х60см

Дизайнер	Шинкевич Екатерина	Дизайн-проект квартиры по адресу:	Спецификация отделочных материалов	Стадия	Лист	Листов
				РП	23	28
телефон	+7 (931) 271-59-56	адрес	Масштаб	SHEM		