
SHEM

ШИНКЕВИЧ ЕКАТЕРИНА

дизайнер интерьеров

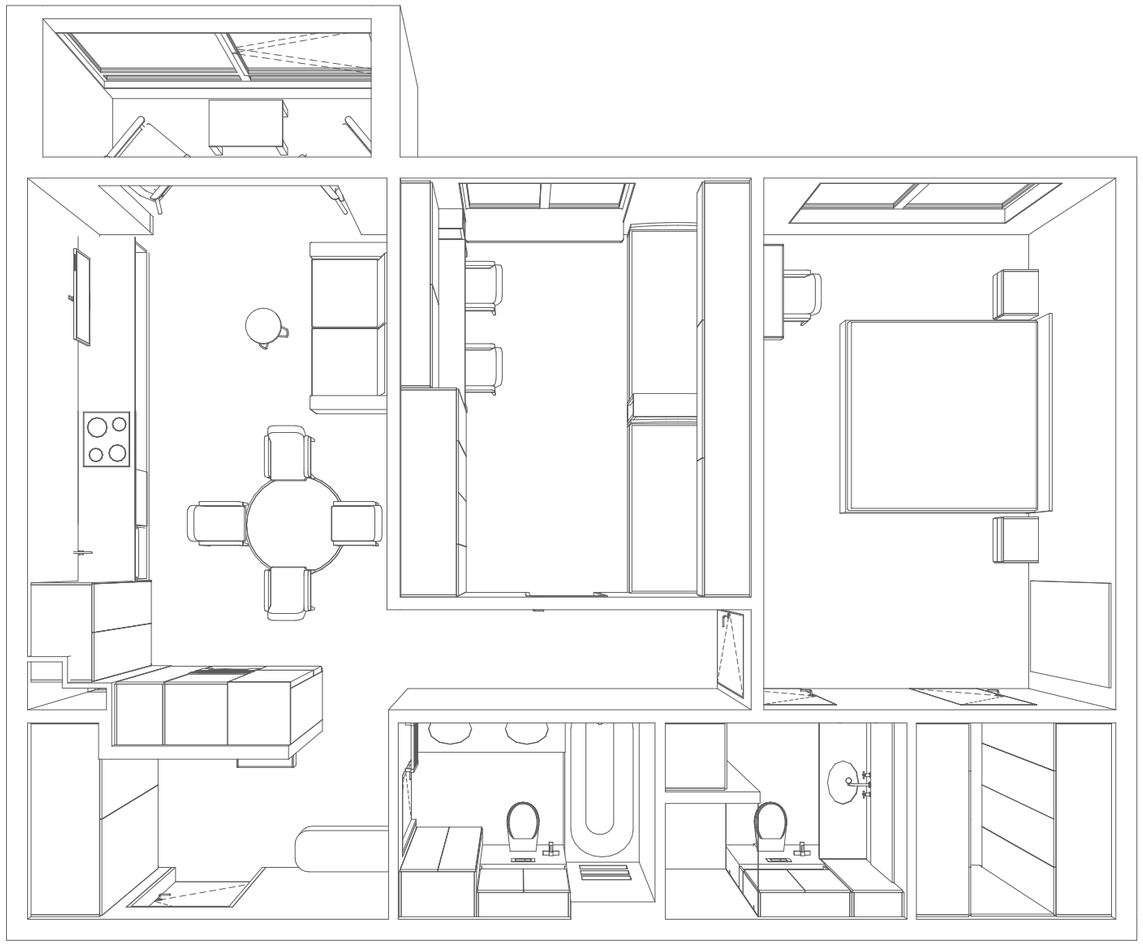

Дизайн-проект квартиры: рабочий проект

ОБЪЕКТ :	наименование
ЗАКАЗЧИК :	заказчик
МЕСТОРАСПОЛОЖЕНИЕ ОБЪЕКТА :	адрес
ТЕЛЕФОН ЗАКАЗЧИКА :	телефон

2025

Лист	Наименование	Примечание
01	Общие данные	
02	План обмеров	
03	План демонтажа	
04	План возводимых перегородок с маркировкой дверных проемов	
05	План после перепланировки	
06	План расстановки мебели	
07	План с мебельными размерами и описанием	
08	План размещения осветительных приборов, привязка выпусков освещения	
09	План выключателей с указанием включения групп светильников	
10	План размещения электрических розеток с привязкой размеров	

Лист	Наименование	Примечание
11	План потолков и гипсокартонных конструкций	
12	План полов с указанием типа напольных покрытий	
13	План размещения санитарно-технического оборудования	
14	План расположения систем отопления и вентиляции	
15	План отделочных материалов по стенам	
16	Развертки по стенам. Прихожая	
17	Развертки по стенам. Кухня-столовая	
18	Развертки по стенам. Кухня-столовая	
19	Развертки по стенам. Коридор	
20	Развертки по стенам. Ванная	

Лист	Наименование	Примечание
21	Развертки по стенам. Детская	
22	Развертки по стенам. Спальня	
23	Развертки по стенам. Душевая	
24	Развертки по стенам. Гардеробная	
25	Спецификация дверей с указанием размеров дверных проемов	
26	Спецификация мебели	
27	Спецификация осветительного оборудования	
28	Спецификация отделочных материалов	

ПОЯСНИТЕЛЬНАЯ ЗАПИСКА

К дизайн-проекту интерьера квартиры, расположенной по адресу: адрес
Проект выполнен на основании обмеров. Квартира имеет общую площадь: 73,34 м^2

Благоустройство квартиры: централизованная система отопления, система очистки воды, электроснабжение, центральная канализация, бойлер.
Наружные стены - кирпич. Внутренние стены - ПГП.

Проект квартиры полностью удовлетворяет пожеланиям Заказчика.

Необходимо произвести следующие работы:

1. Возвести новые конструкции согласно РП-04;
2. Устроить потолки согласно РП-11;
3. Выполнить электропроводку согласно РП-08, РП-09, РП-10;
4. Полы устроить согласно РП-12;
5. Произвести отделку согласно РП-15, РП-16 - РП-60.

дизайнер	Шинкевич Екатерина	Дизайн-проект квартиры по адресу: адрес	Масштаб	Стадия	Лист	Листов
				РП	01	28
телефон	+7 (931) 271-59-56			SHEM		

План обмеров

Условные обозначения:

(2) – номер помещения

– существующие конструкции



Экспликация помещений на этапе обмеров		
№	Название помещения	Площадь, кв.м
1	Прихожая	6,40
2	Санузел (общий)	4,55
3	Кухня-столовая	16,95
4	Коридор	3,42
5	Детская	12,10
6	Спальня	18,00
7	Санузел при спальне	4,29
8	Гардеробная	3,53
9	Балкон	4,10
		73,34 м²

Примечание:


1. Все размеры указаны в милиметрах.
2. Обмерный план выполнен на основании обмеров. Погрешность измерений не превышает 30мм.
3. Высота потолка 2715мм.

дизайнер	Шинкевич Екатерина	Дизайн-проект квартиры по адресу: адрес	Масштаб 1:50	Стадия	Лист	Листов
				РП	02	28
телефон	+7 (931) 271-59-56			SHEM		

План демонтажа

Условные обозначения:

- демонтируемые конструкции
- существующие конструкции

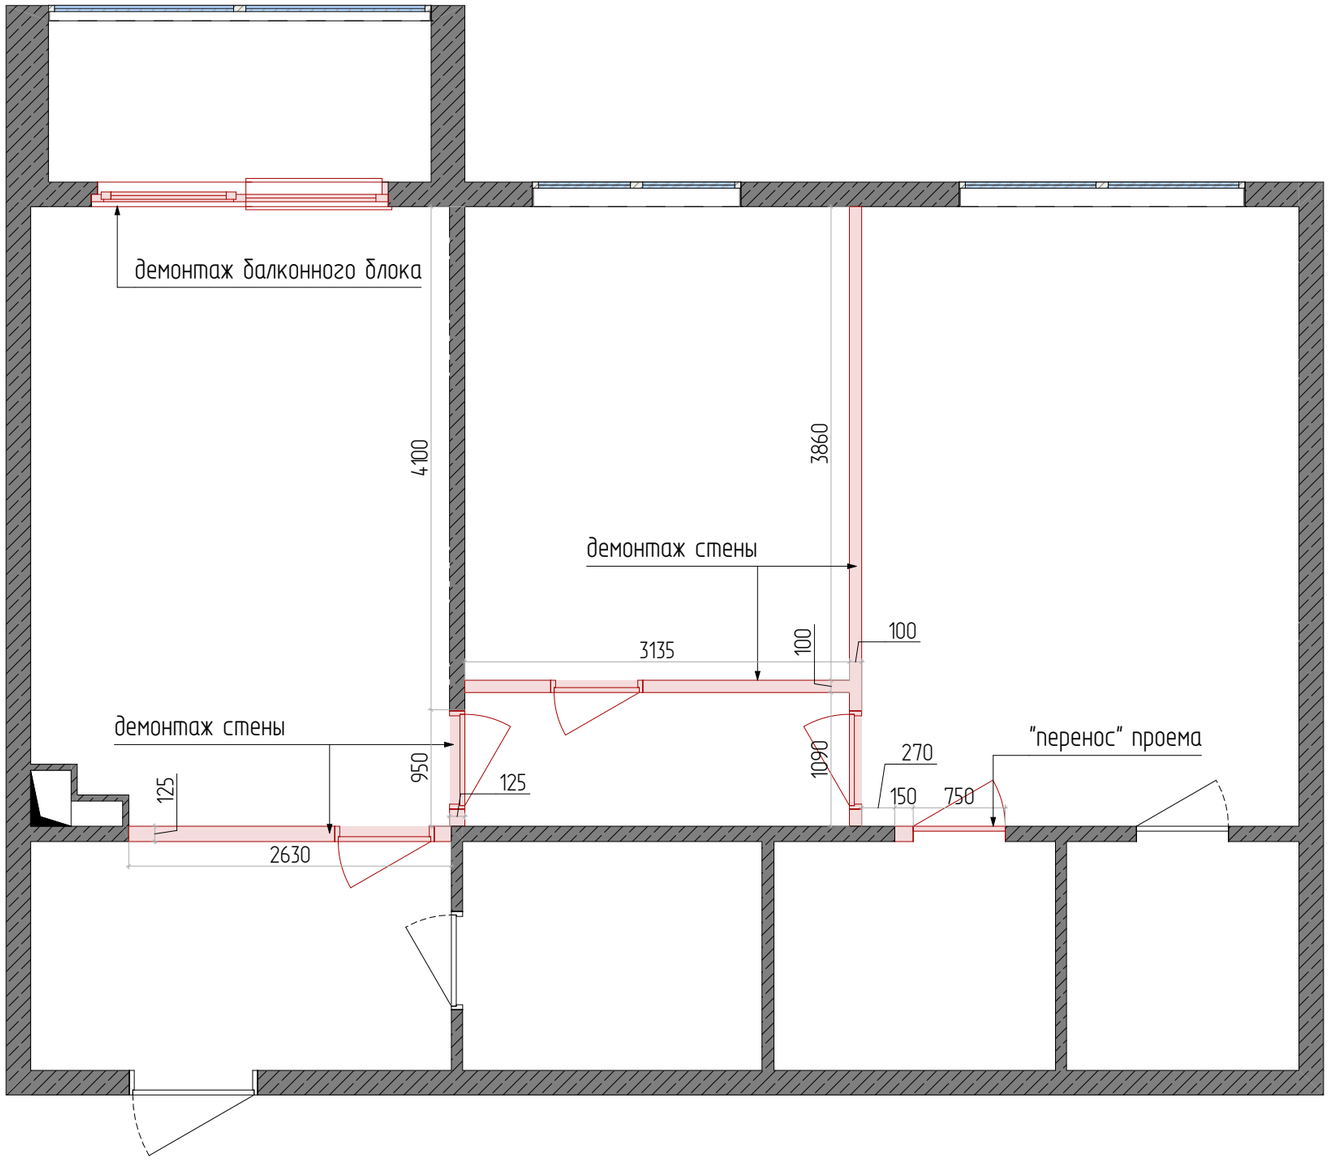

Примечание:


1. Все размеры указаны в милиметрах.
2. Произвести демонтаж отмеченых конструкций.
3. План демонтажа смотреть совместно с планом монтажа.


дизайнер	Шинкевич Екатерина	Дизайн-проект квартиры по адресу: адрес	Масштаб 1:50	Стадия	Лист	Листов
				РП	03	28
телефон	+7 (931) 271-59-56			SHEM		

План возводимых перегородок с маркировкой дверных проемов

Условные обозначения:

- существующие конструкции
- новые конструкции

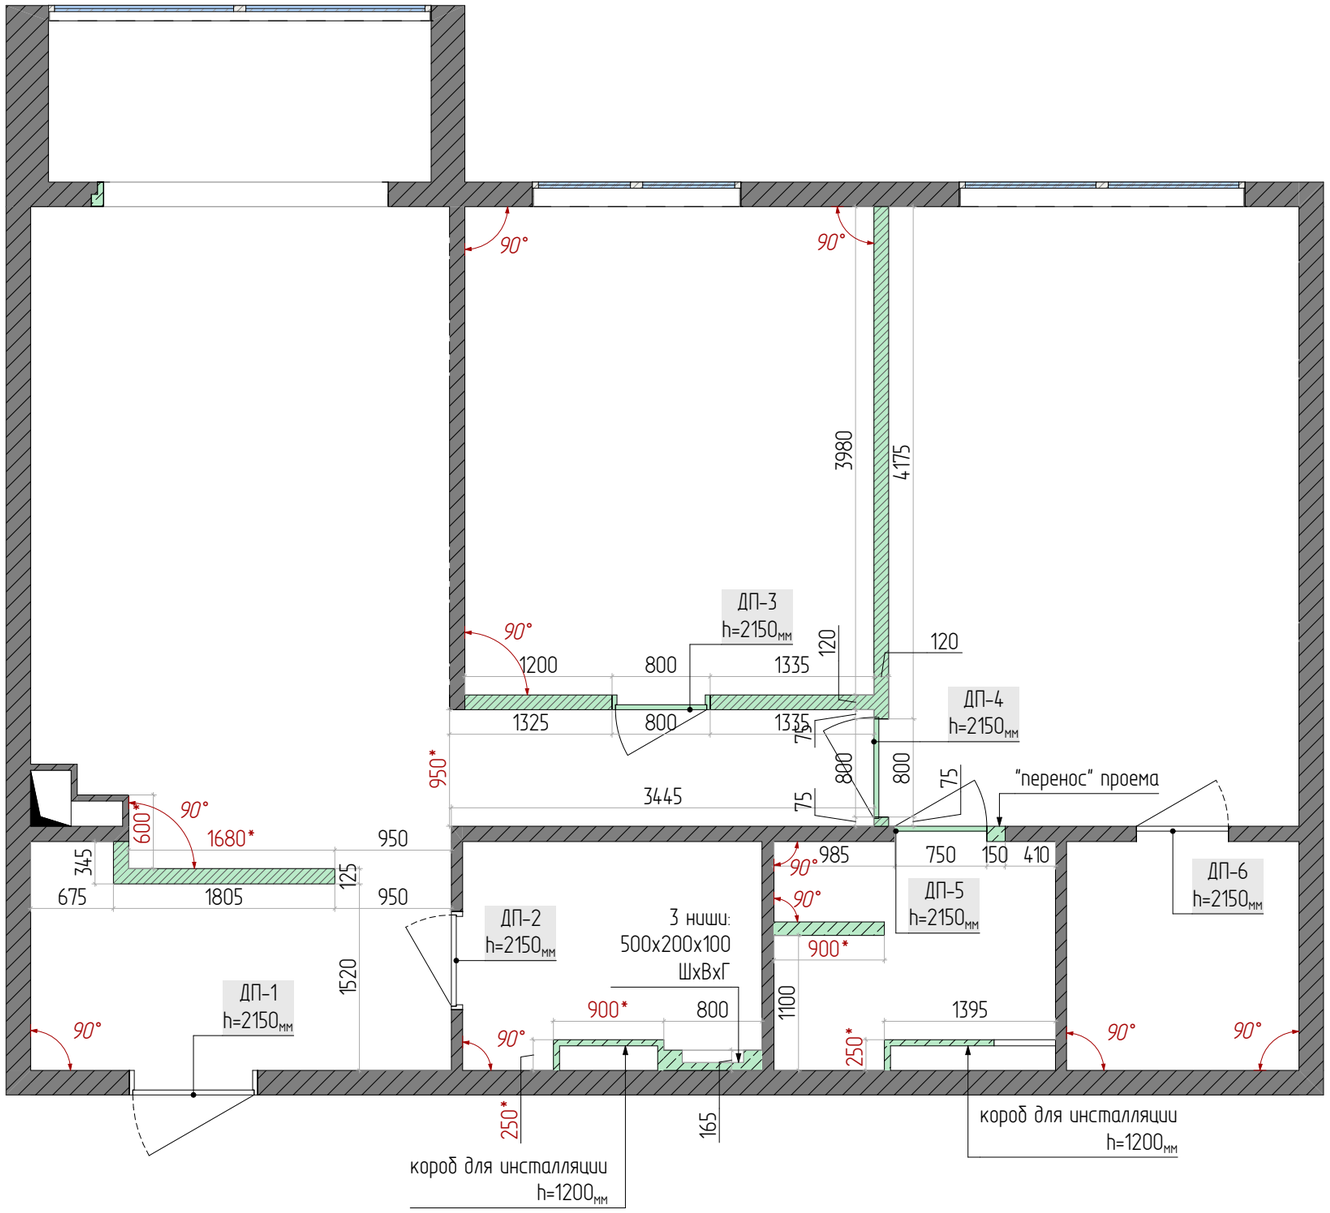

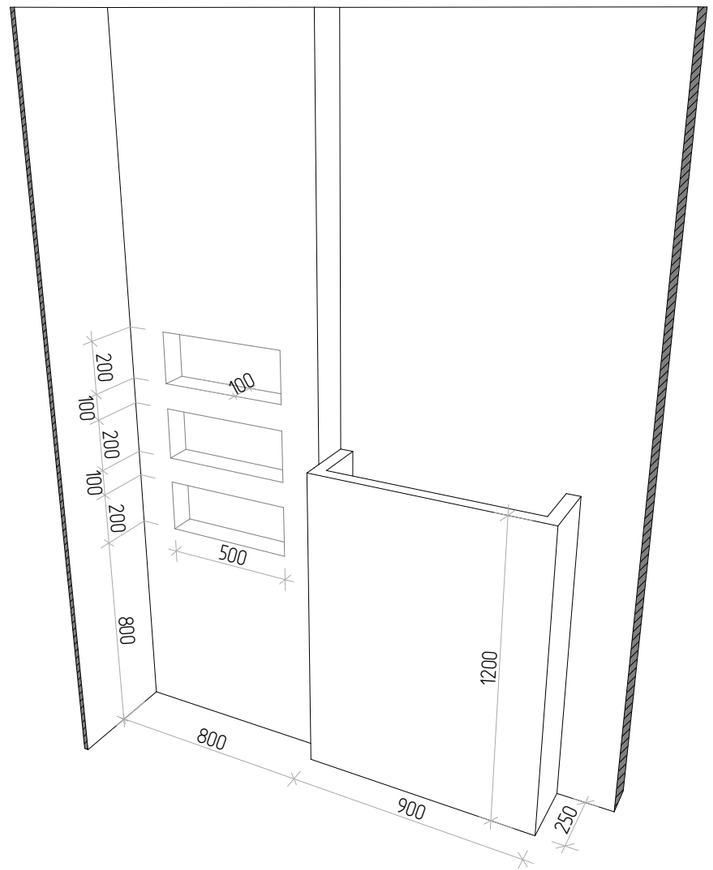

Вид 1

Устройство ниш и короба для инсталляции в ванной

Примечание:

1. В первую очередь обращать внимание на выносные надписи.
2. Возвести конструкции.
3. Все критичные размеры отмечены красным на чертеже.
4. Высота всех проемов указана от уровня чистового пола.
5. Стены выровнять под 90 градусов (для точного примыкания ко встроенной мебели).

дизайнер	Шинкевич Екатерина	Дизайн-проект квартиры по адресу: адрес	Масштаб 1:50, 1:200,15	Стадия	Лист	Листов
				РП	04	28
телефон	+7 (931) 271-59-56			SHEM		

План после перепланировки




Экспликация помещений		
№	Название помещения	S, кв.м
1	Прихожая	5,57
2	Санузел (общий)	4,55
3	Кухня-столовая	17,86
4	Коридор	3,28
5	Детская	13,27
6	Спальня	16,89
7	Санузел при спальне	4,18
8	Гардеробная	3,53
9	Балкон	4,10
		73,23 м²

Примечание:

1. Все размеры являются проектируемыми и требуют уточнения на этапе чистовой отделки.
2. В проекте не учтены отклонения на кривизну стен и перекрытий.

дизайнер	Шинкевич Екатерина	Дизайн-проект квартиры по адресу: адрес	Масштаб 1:50	Стадия	Лист	Листов
				РП	05	28
телефон	+7 (931) 271-59-56			SHEM		

План расстановки мебели

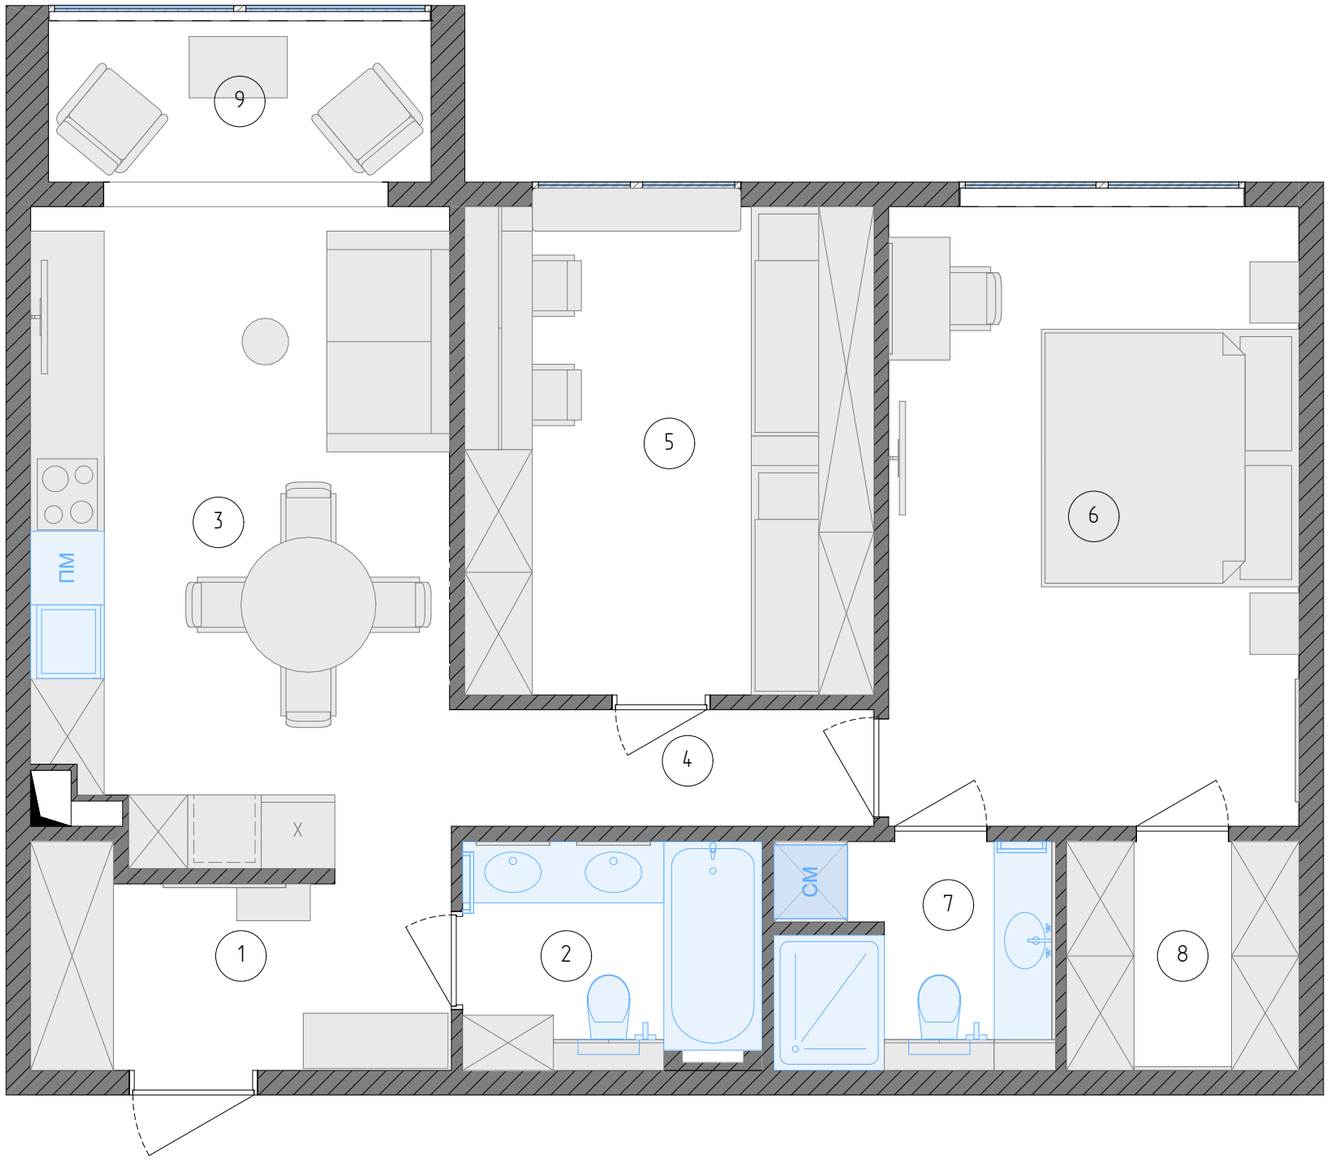

Экспликация помещений		
№	Название помещения	S, кв.м
1	Прихожая	5,57
2	Санузел (общий)	4,55
3	Кухня-столовая	17,86
4	Коридор	3,28
5	Детская	13,27
6	Спальня	16,89
7	Санузел при спальне	4,18
8	Гардеробная	3,53
9	Балкон	4,10
		73,23 м²

дизайнер	Шинкевич Екатерина	Дизайн-проект квартиры по адресу: адрес	Масштаб 1:50	Стадия	Лист	Листов
				РП	06	28
телефон	+7 (931) 271-59-56			SHEM		

План с мебельными размерами и описанием



Экспликация помещений		
№	Название помещения	S, кв.м
1	Прихожая	5,57
2	Санузел (общий)	4,55
3	Кухня-столовая	17,86
4	Коридор	3,28
5	Детская	13,27
6	Спальня	16,89
7	Санузел при спальне	4,18
8	Гардеробная	3,53
9	Балкон	4,10
		73,23 м²

Примечание:


1. Красным цветом выделены расстояния между предметами.
2. Все размеры являются проектируемыми.
3. Перед заказом встраиваемой мебели или иного оборудования требуется предварительный замер фирмой производителем.

дизайнер	Шинкевич Екатерина	Дизайн-проект квартиры по адресу: адрес	Масштаб 1:50	Стадия	Лист	Листов
телефон	+7 (931) 271-59-56			РП	07	28
				SHEM		

План размещения осветительных приборов, привязка выпусков освещения

Условные обозначения:

– электровывод

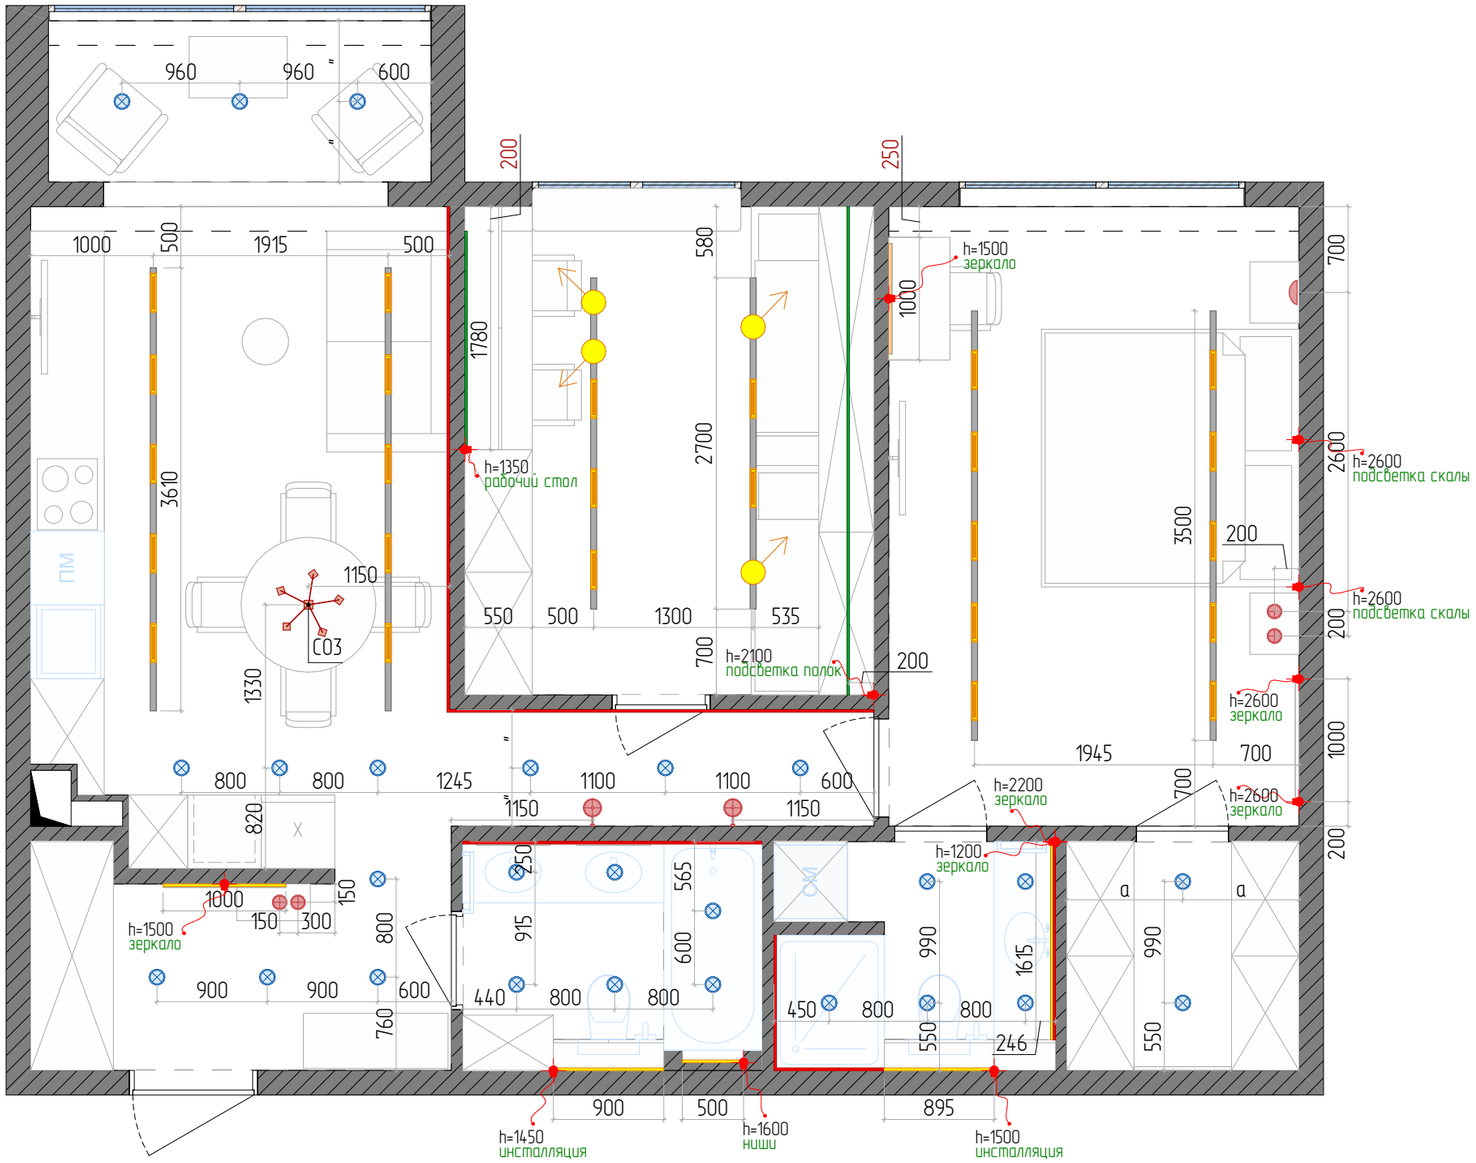

Спецификация трека			
ID	Условное обозначение	Наименование	Длина, мм
Тр01		Трек	19620

LED лента			
ID	Условное обозначение	Наименование	Длина, мм
С01		подсветка зеркала	3615
С02		"парящий" потолок	13635
С03		подсветка ниш	2295
С04		подсветка рабочей зоны	1780
С05		подсветка полок	3980
С06		вертикальная подсветка	9800
			35105 мм

Условное обозначение светильников			
ID	Изображение	Тип светильника	Кол-во
С01		настенный светильник	4
С02		подвесной светильник	4
С03		люстра	1
			9


Примечание:

1. В санузле установить влагозащитные светильники.
2. В первую очередь обращать внимание на выносные надписи.
3. Все размеры даны по осям осветительных приборов.
4. Расположение светодиодных лент смотреть в развертках.

дизайнер	Шинкевич Екатерина	Дизайн-проект квартиры по адресу: адрес	Масштаб 1:50	Стадия	Лист	Листов
				РП	08	28
телефон	+7 (931) 271-59-56			SHEM		

План выключателей с указанием включения групп светильников

Условное обозначение светильников			
ID	Изображение	Тип светильника	Кол-во
C01		настенный светильник	4
C02		подвесной светильник	4
C03		люстра	1
			9

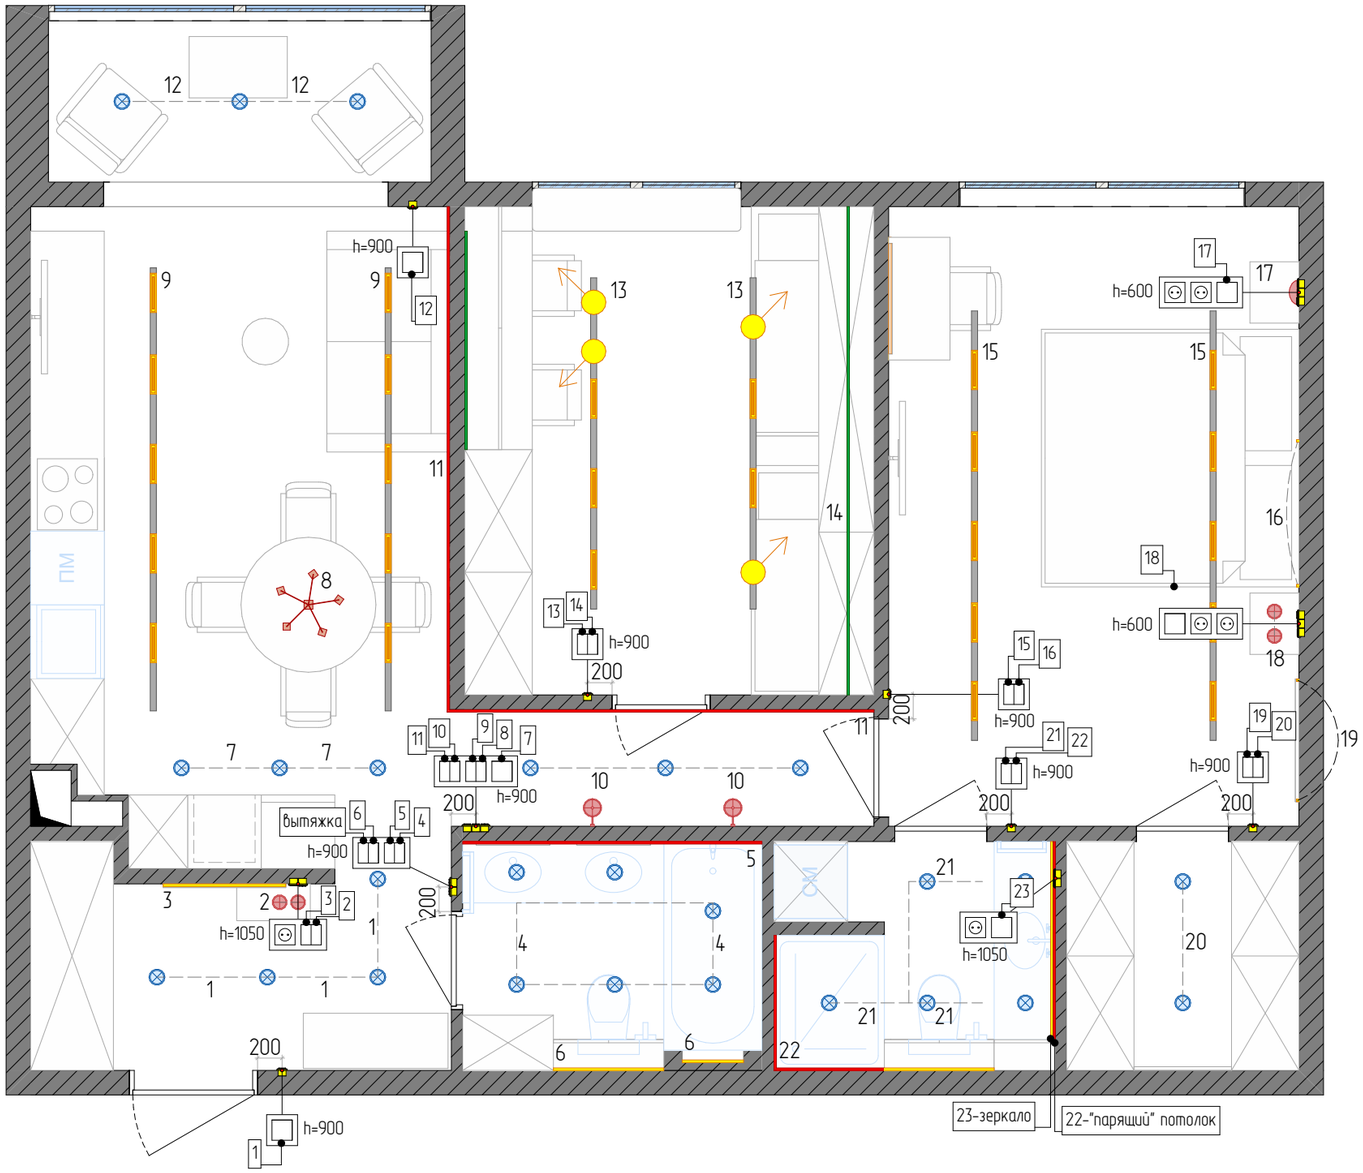

Примечание:


1. Выключатели и переключатели разместить на высоте 900$_{мм}$ от уровня чистового пола, если не указанно иное.

дизайнер	Шинкевич Екатерина	Дизайн-проект квартиры по адресу: адрес	Масштаб 1:50	Стадия	Лист	Листов
				РП	09	28
телефон	+7 (931) 271-59-56			SHEM		

План размещения электрических розеток с привязкой размеров

Условные обозначения:

- электровывод
- электровывод для сплит-системы

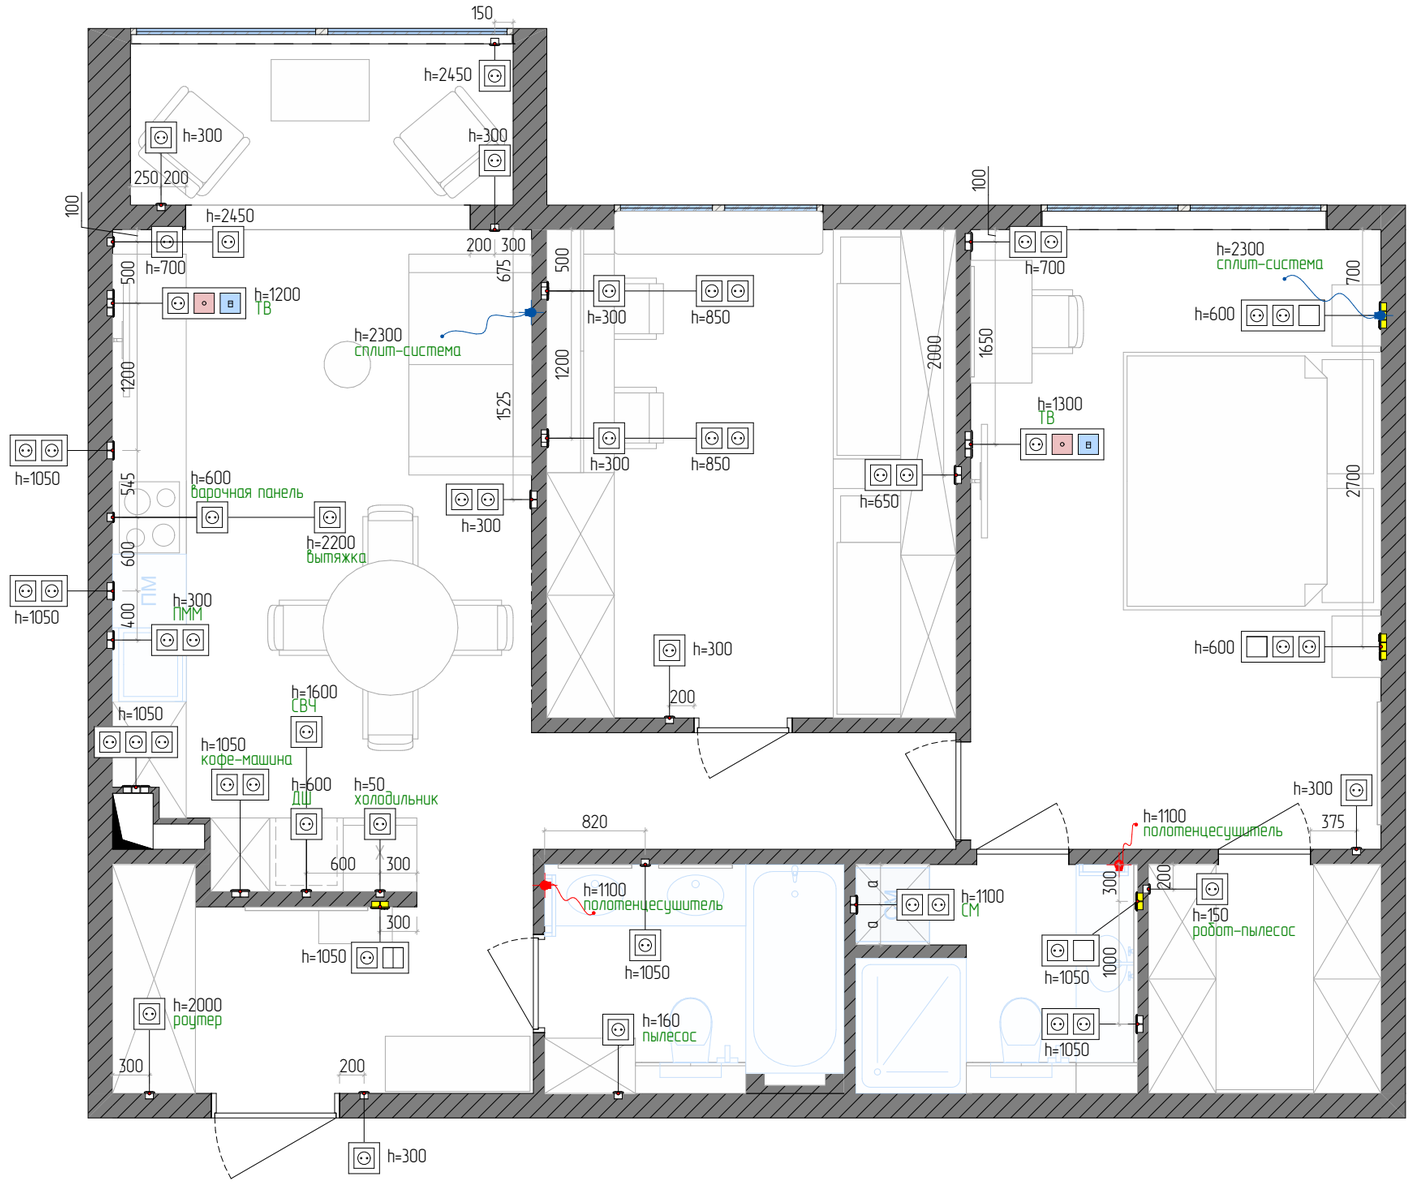

Рамки (общее количество)		
Тип рамки (блока)	Рамка ориентация	Кол-во
Рамка x1	Горизонтальная	25
Рамка x2	Горизонтальная	14
Рамка x3	Горизонтальная	6

Примечание:

1. Высота розеток 300мм от уровня чистового пола, если не указано иное.
2. Установку рядом стоящих розеток и выключателей произвести под общую рамку.
3. В первую очередь, обращать внимание на выносные надписи.

дизайнер	Шинкевич Екатерина	Дизайн-проект квартиры по адресу: адрес	Масштаб 1:50	Стадия	Лист	Листов
				РП	10	28
телефон	+7 (931) 271-59-56			SHEM		

План потолков и гипсокартонных конструкций

Условные обозначения:

02 – обозначение типа потолка

+2 900 – отметка высоты относительно чисто



Ведомость потолков			
ID	Условное обозначение	Наименование	Площадь, кв.м (без запаса)
01		Натяжной потолок	70,45
02		Штукатурка и покраска	2,06

Примечание:

1. За отметку 0,000 принята высота чистового пола.
2. Подвесной потолок опустить на минимальную высоту (80мм), от самой нижней точки чернового потолка в конкретном помещении.
3. Отметки высот указаны от чистового пола.
4. На развертках все высоты даны от чистового пола.

дизайнер	Шинкевич Екатерина	Дизайн-проект квартиры по адресу: адрес	Масштаб 1:50	Стадия	Лист	Листов
				РП	11	28
телефон	+7 (931) 271-59-56			SHEM		

План полов с указанием типа напольных покрытий

Условные обозначения:

- направление укладки плитки

П02 - обозначение типа пола



Напольные покрытия					
ID	Условное обозначение	Наименование	Площадь, кв.м (без запаса)	Примечание	Изображение
П01		Кварцвинил	65,33	укладка "ёлочкой"	
П02		К-340	4,23	120х60	
П03		Керамогранит Laurent_GT	3,88	120х60	

Спецификация плинтуса						
ID	Условное обозначение	Сечение	Изображение	Наименование	Длина, мм	Примечание
П01				Плинтус	42920	

Примечание:


1. Количество материала дано без запаса на подрезку.
2. Привязку стыка напольных покрытий внутри дверных проемов уточнить у поставщика дверей.
3. Душевой поддон в строительном исполненнии с уклоном в сторону сливного лотка. Расположение и уклон определить на месте.

дизайнер	Шинкевич Екатерина	Дизайн-проект квартиры по адресу: адрес	Масштаб 1:50	Стадия	Лист	Листов
телефон	+7 (931) 271-59-56			РП	12	28
				SHEM		

План размещения санитарно-технического оборудования

Условные обозначения:

- – канализационная труба
- – труба подачи горячего водоснабжения
- – труба подачи холодного водоснабжения
- – размещение стока раковин и сливов

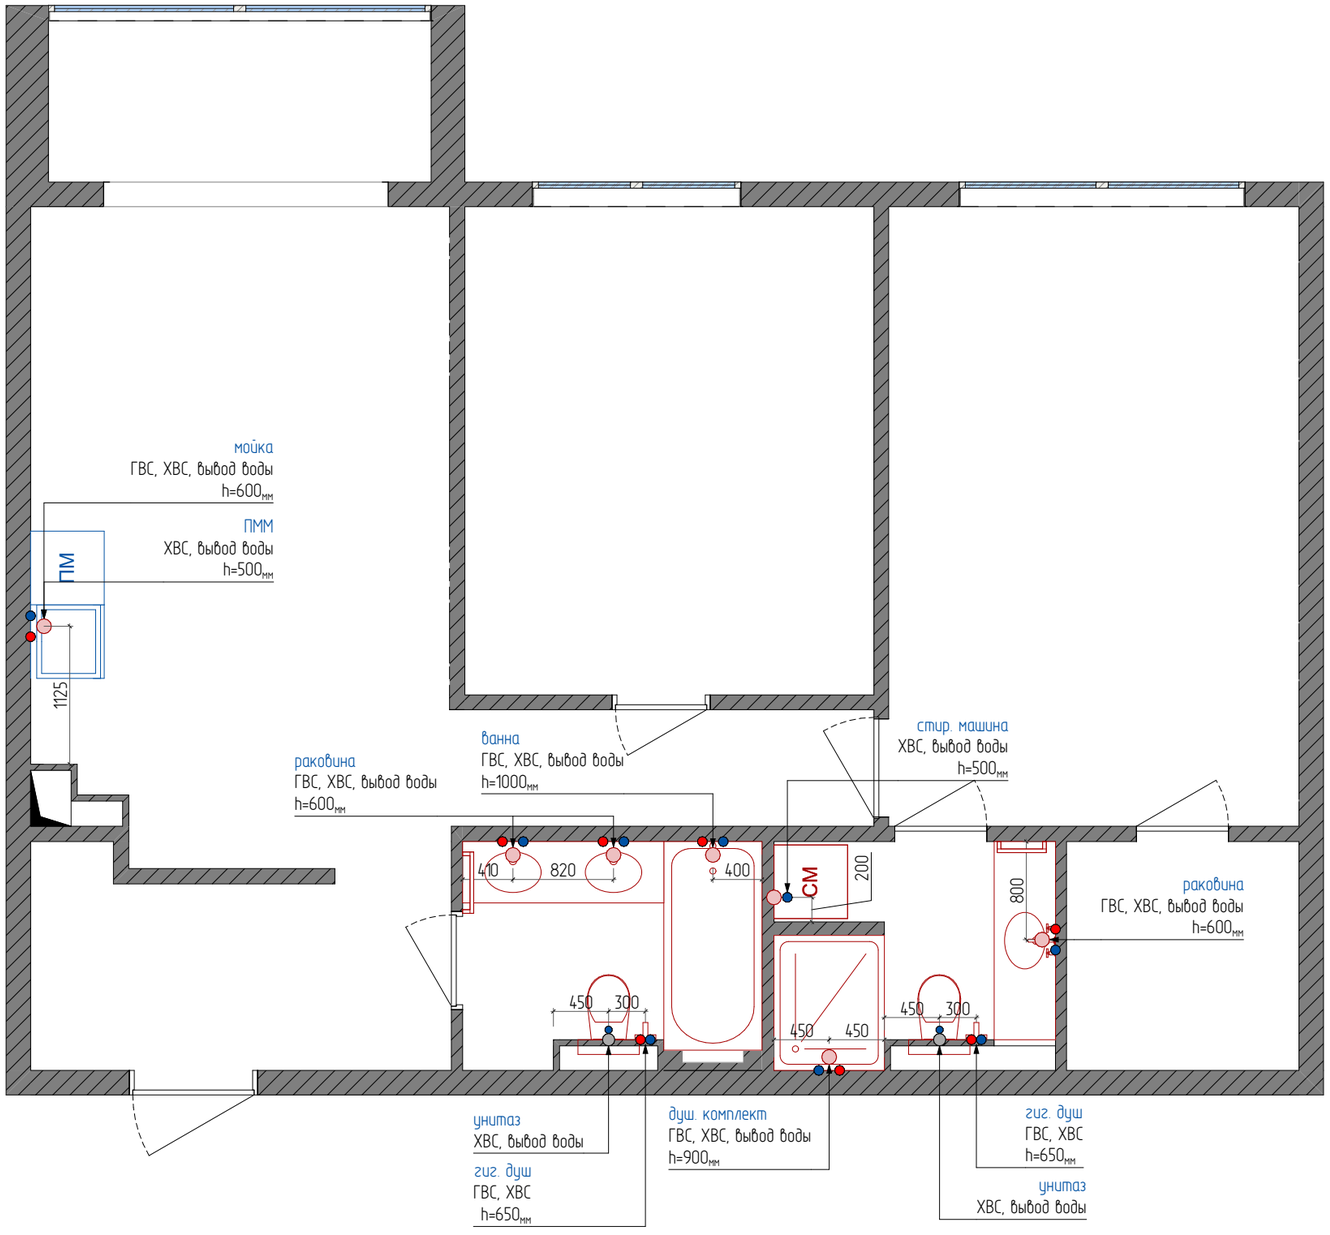

Примечание:

1. Перед началом работ все размеры уточнить по месту специалистом.
2. Все размеры даны по конструкциям, без учета плитки и клея.
3. Организовать гидроизоляцию стен и пола в ванных комнатах.


дизайнер	Шинкевич Екатерина	Дизайн-проект квартиры по адресу: адрес	Масштаб 1:50	Стадия	Лист	Листов
				РП	13	28
телефон	+7 (931) 271-59-56			SHEM		

План расположения систем отопления и вентиляции

Условные обозначения:

– радиаторы отопления


– сплит-система

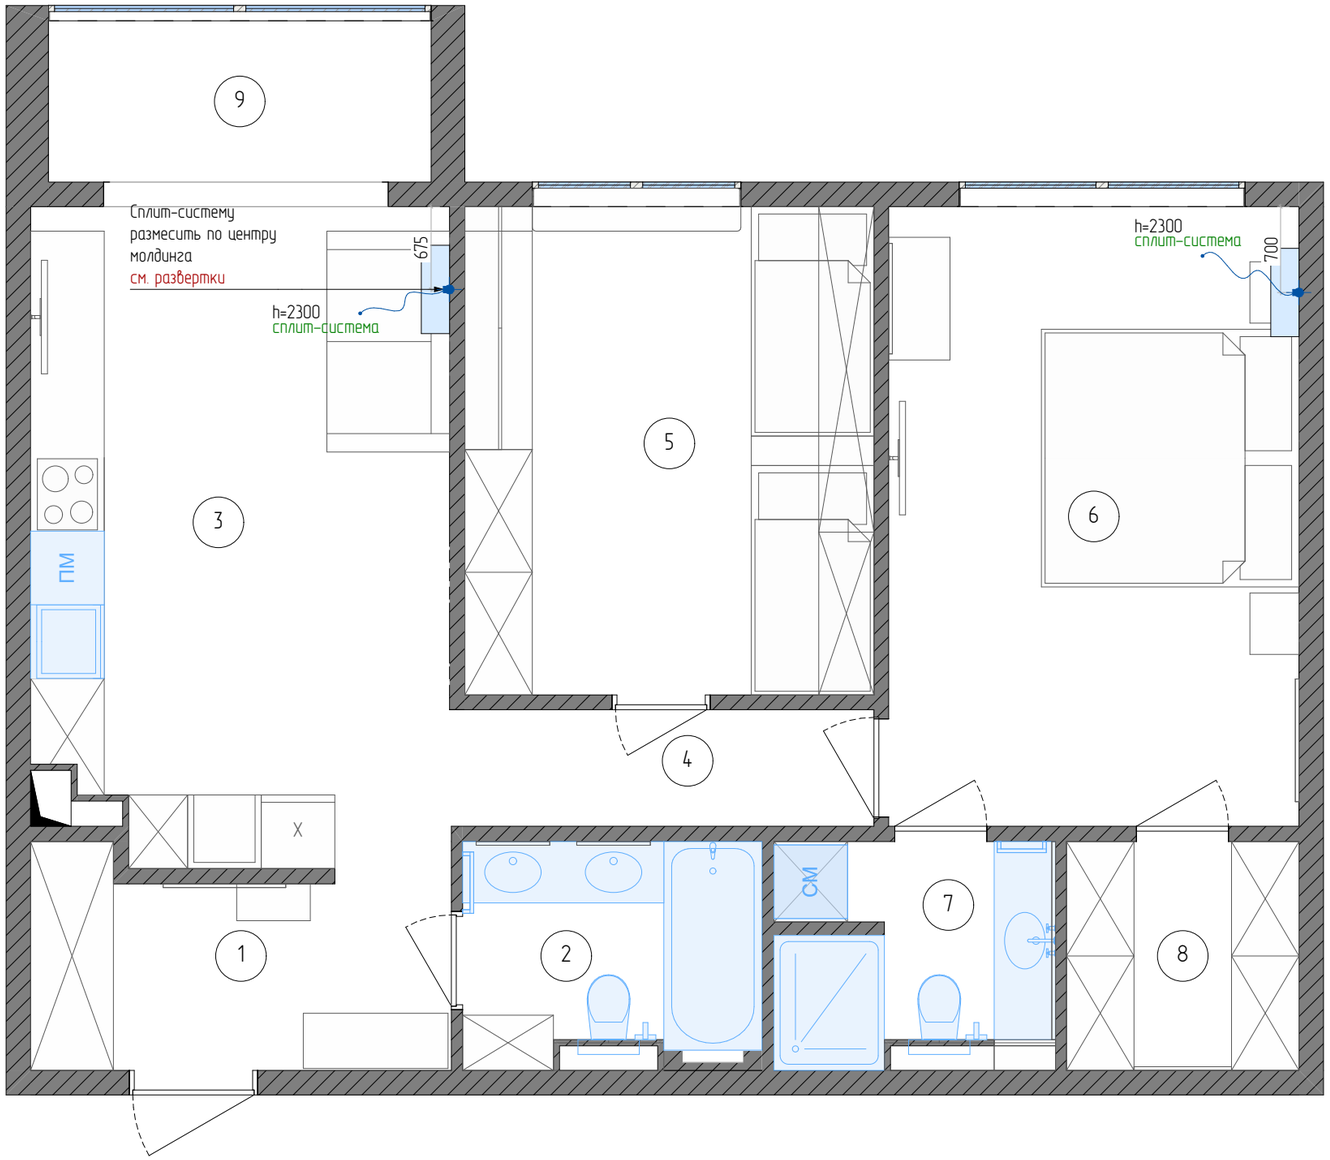

Экспликация помещений		
№	Название помещения	S, кв.м
1	Прихожая	5,57
2	Санузел (общий)	4,55
3	Кухня-столовая	17,86
4	Коридор	3,28
5	Детская	13,27
6	Спальня	16,89
7	Санузел при спальне	4,18
8	Гардеробная	3,53
9	Балкон	4,10
		73,23 м²

дизайнер	Шинкевич Екатерина	Дизайн-проект квартиры по адресу: адрес	Масштаб 1:50	Стадия	Лист	Листов
				РП	14	28
телефон	+7 (931) 271-59-56			SHEM		


План отделочных материалов по стенам

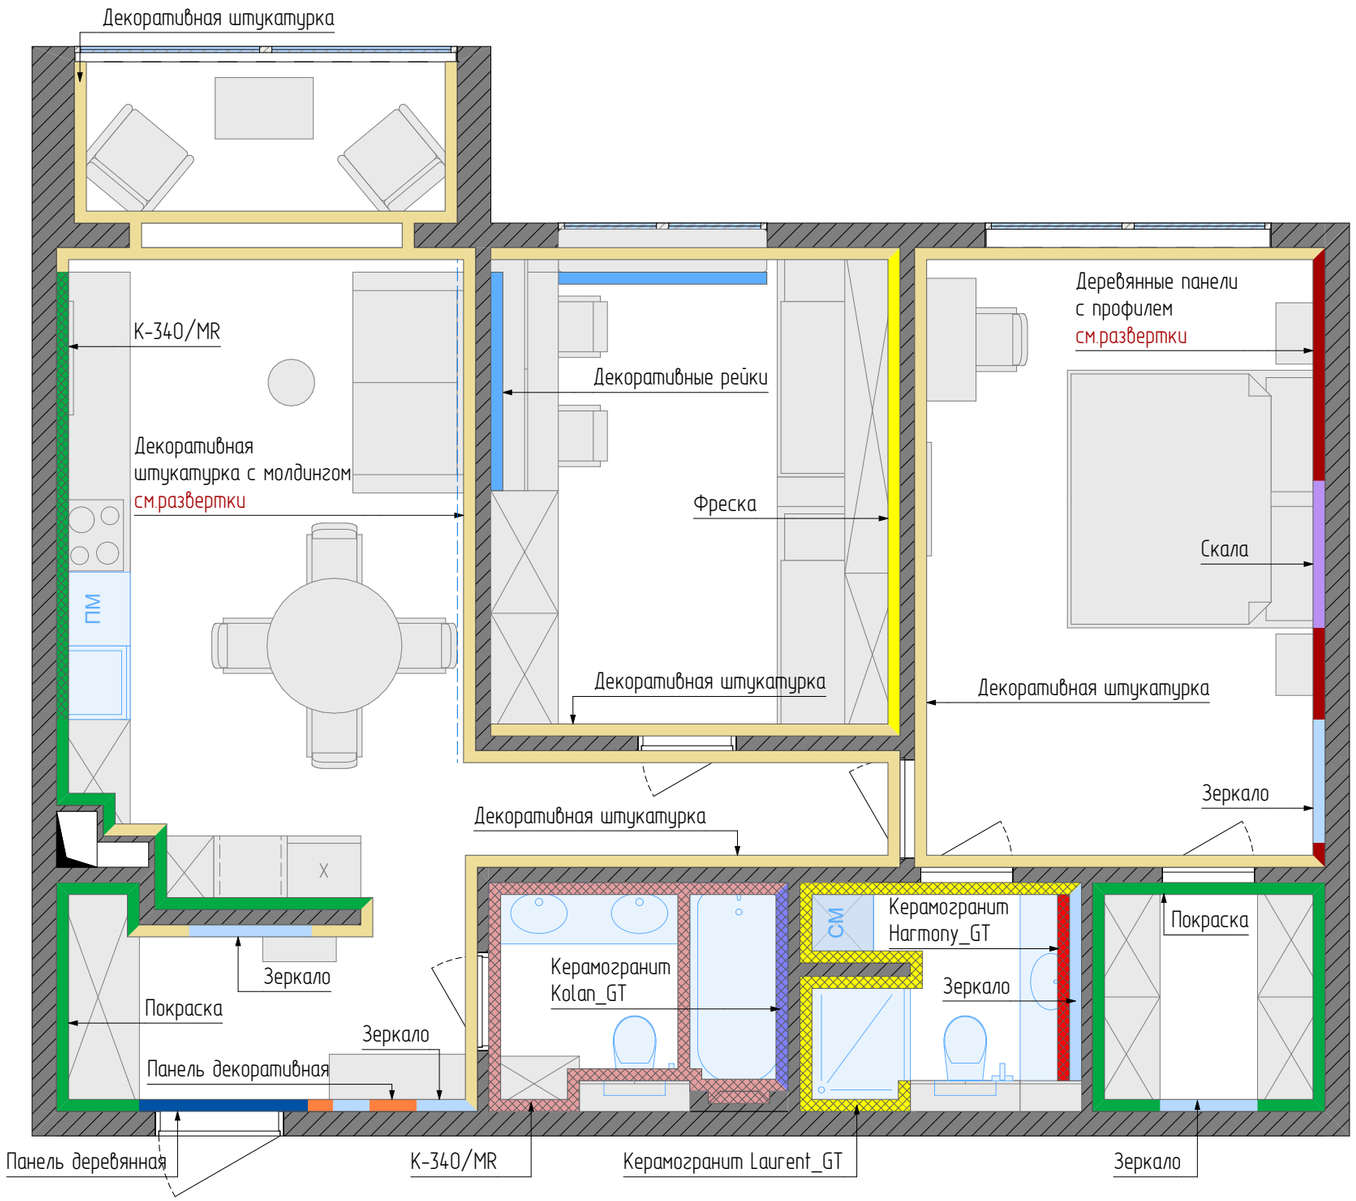



Условное обозначение	Наименование
	К-340/MR
	Декоративные рейки
	Покраска
	Декоративная штукатурка
	Керамогранит Laurent_GT
	Фреска
	Зеркало
	Керамогранит Harmony_GT
	Деревянные панели
	Скала
	Панель декоративная
	Панель деревянная
	Керамогранит Kolan_GT


дизайнер	Шинкевич Екатерина	Дизайн-проект квартиры по адресу: адрес	Масштаб 1:50	Стадия	Лист	Листов
				РП	15	28
телефон	+7 (931) 271-59-56			SHEM		


Развертки по стенам. Прихожая

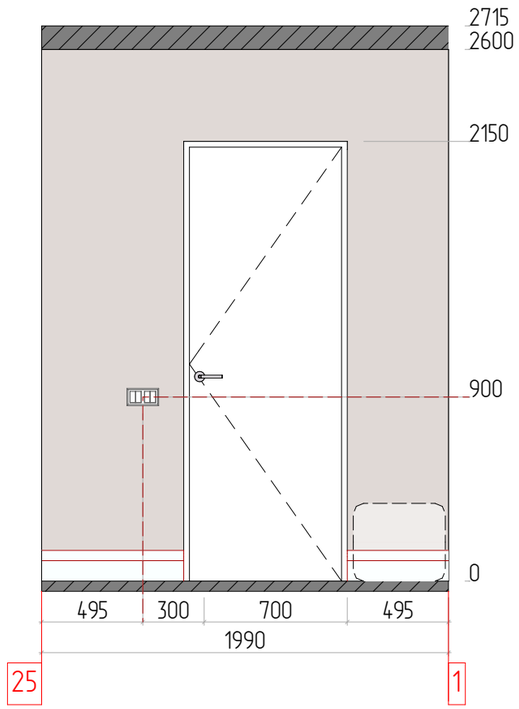

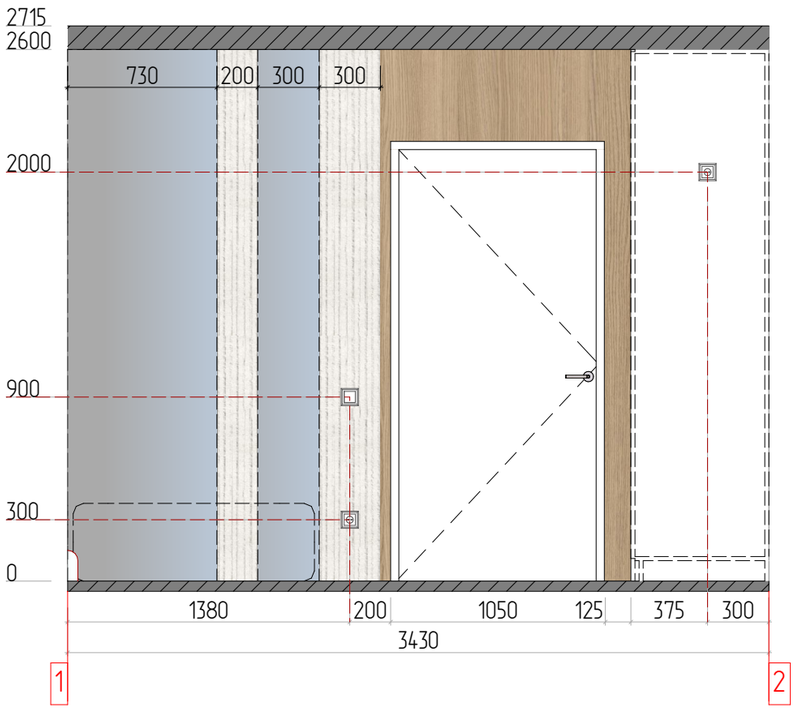

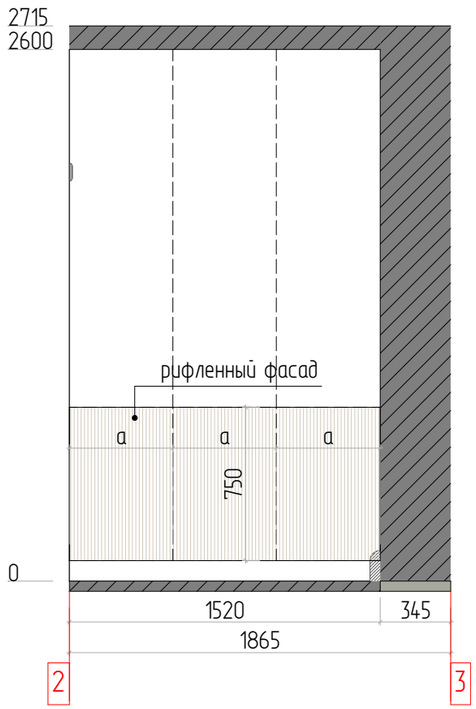

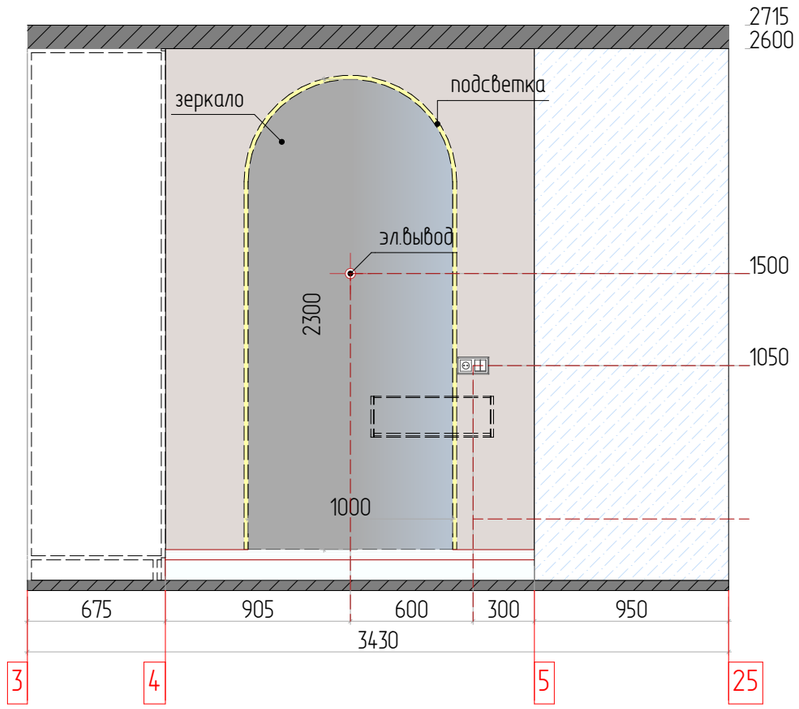

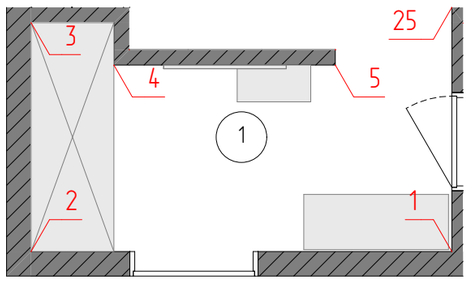

Расход материалов. Прихожая


Наименование	Условное обозначение	Площадь, кв.м (без запаса)	Примечание
Декоративная штукатурка		8,14	
Краска техническая		7,45	
Панели декоративные		1,30	
Панели деревянные		1,15	


Примечание:


1. Количество материала для отделки стен дано без запаса.
2. Пересчитать все материалы перед заказом с менеджером бренда (используя данные проекта).
3. Согласовать все размеры при заказе мебели.


дизайнер	Шинкевич Екатерина	Дизайн-проект квартиры по адресу: адрес	Масштаб 1:30, 1:1	Стадия	Лист	Листов
				РП	16	28
телефон	+7 (931) 271-59-56			SHEM		

Развертки по стенам. Кухня-столовая

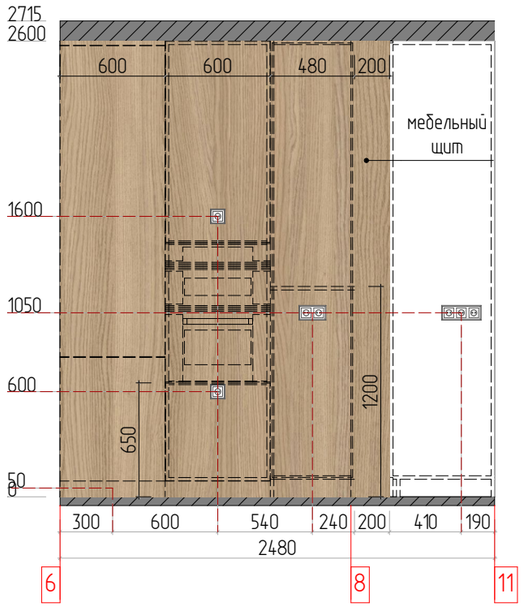

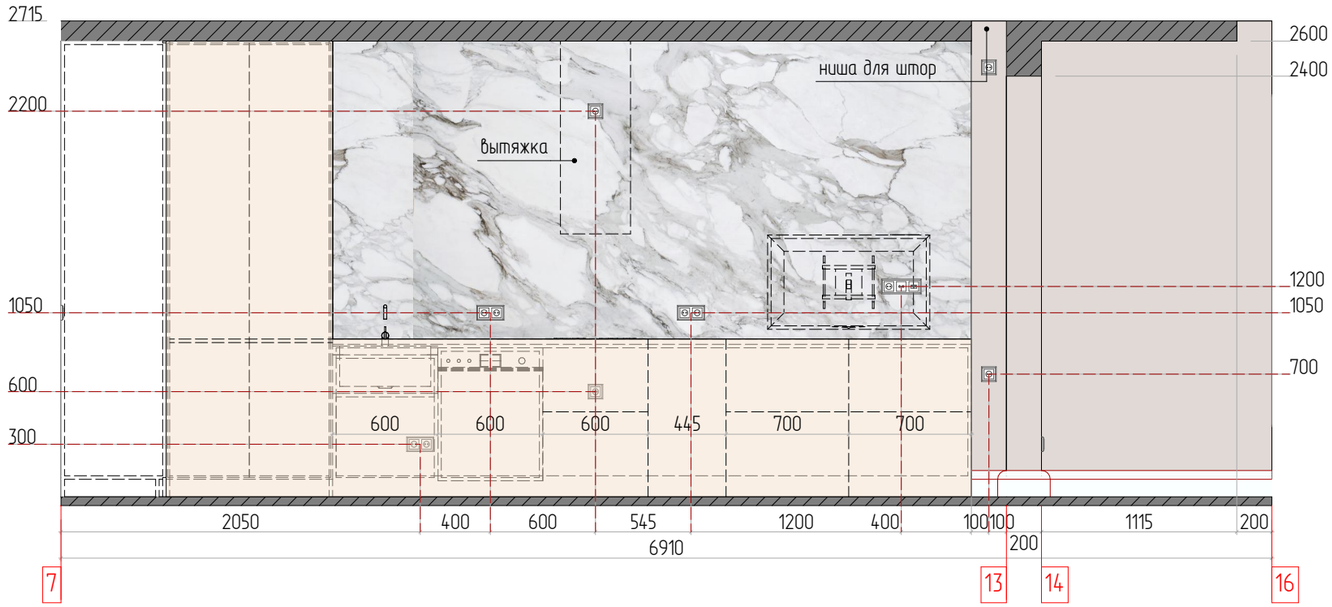

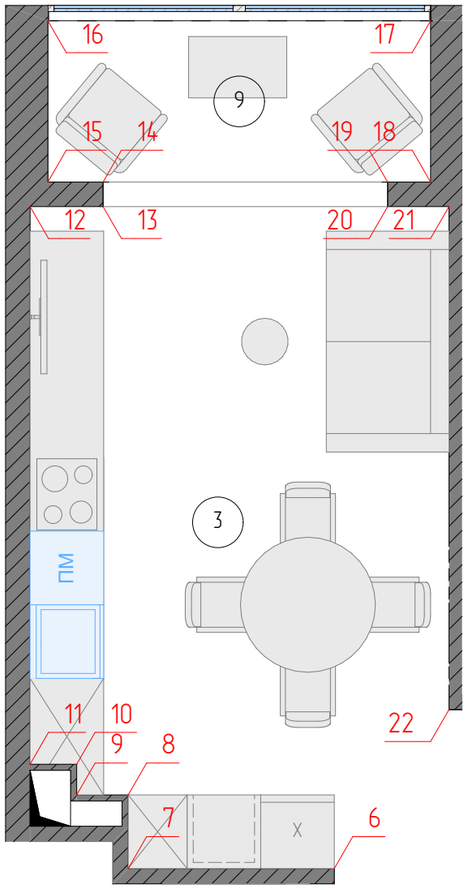

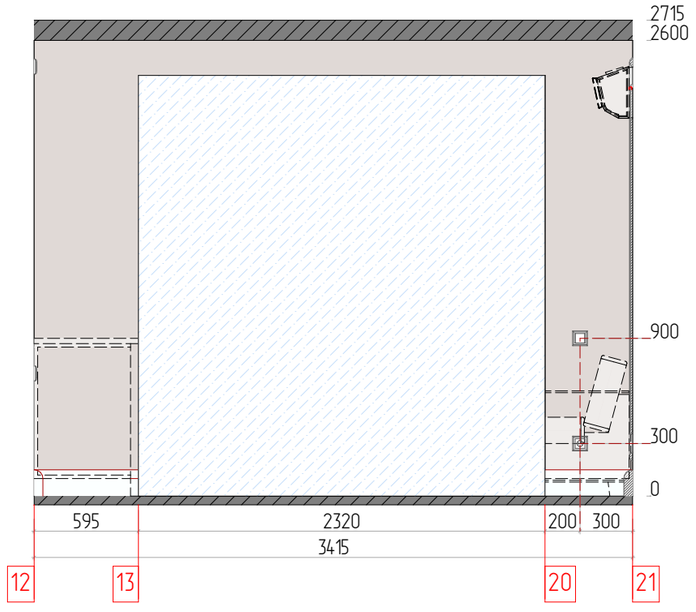


Расход материалов. Кухня-столовая			
Наименование	Условное обозначение	Площадь, кв.м (без запаса)	Примечание
Декоративная штукатурка		24,91	
Краска техническая		13,76	
Фартук		6,20	


Примечание:


1. Количество материала для отделки стен дано без запаса.
2. Пересчитать все материалы перед заказом с менеджером бренда (используя данные проекта).
3. Согласовать все размеры при заказе мебели.

дизайнер	Шинкевич Екатерина	Дизайн-проект квартиры по адресу: адрес	Масштаб 1:35, 1:1	Стадия	Лист	Листов
				РП	17	28
телефон	+7 (931) 271-59-56			SHEM		

Развертки по стенам. Кухня-столовая

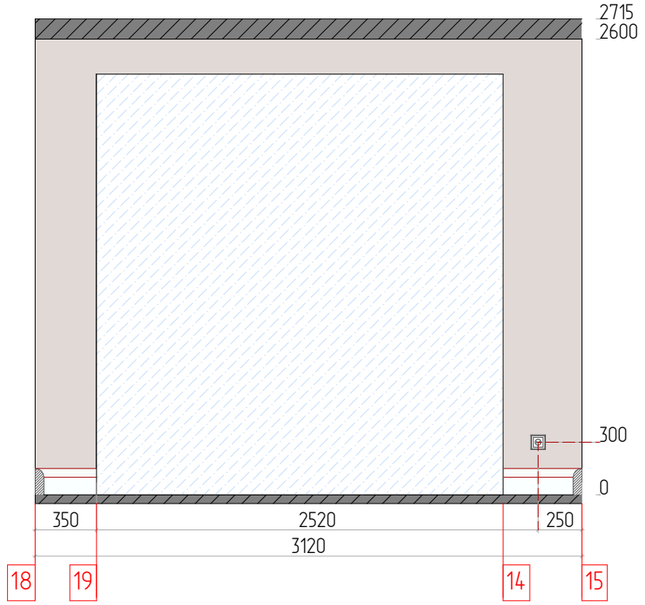

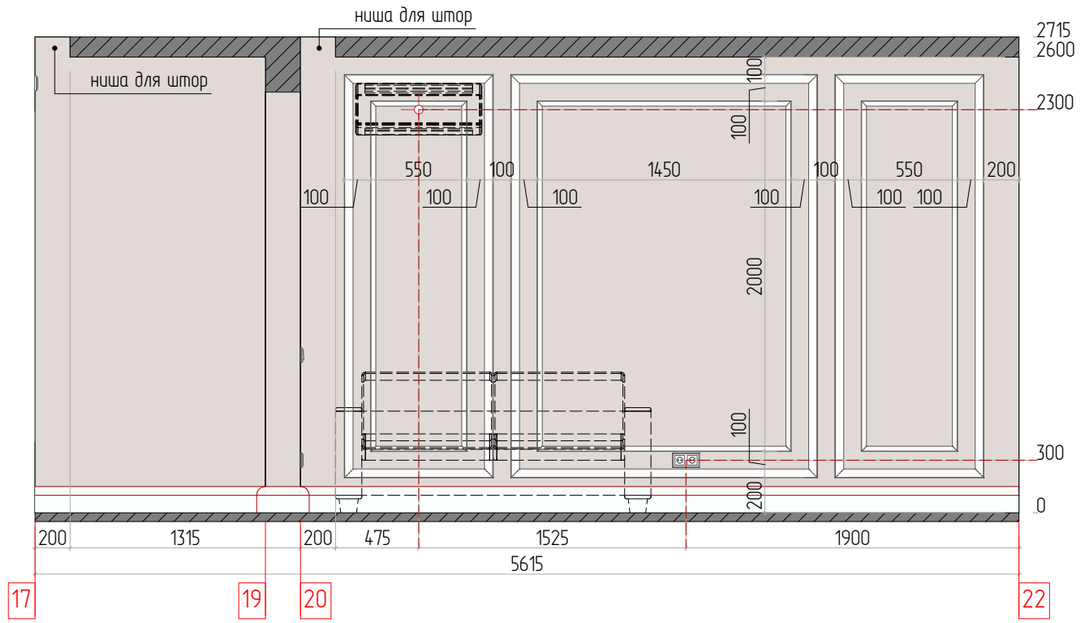

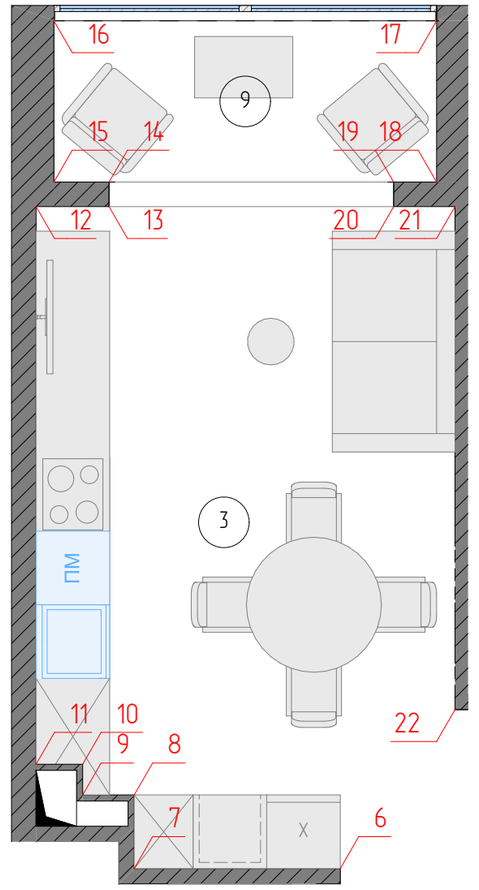


Расход материалов. Кухня-столовая			
Наименование	Условное обозначение	Площадь, кв.м (без запаса)	Примечание
Декоративная штукатурка		24,91	
Краска техническая		13,76	
Фартук		6,20	


Примечание:


1. Количество материала для отделки стен дано без запаса.
2. Пересчитать все материалы перед заказом с менеджером бренда (используя данные проекта).
3. Согласовать все размеры при заказе мебели.


дизайнер	Шинкевич Екатерина	Дизайн-проект квартиры по адресу: адрес	Масштаб 1:35, 1:1	Стадия	Лист	Листов
				РП	18	28
телефон	+7 (931) 271-59-56			SHEM		

Развертки по стенам. Коридор

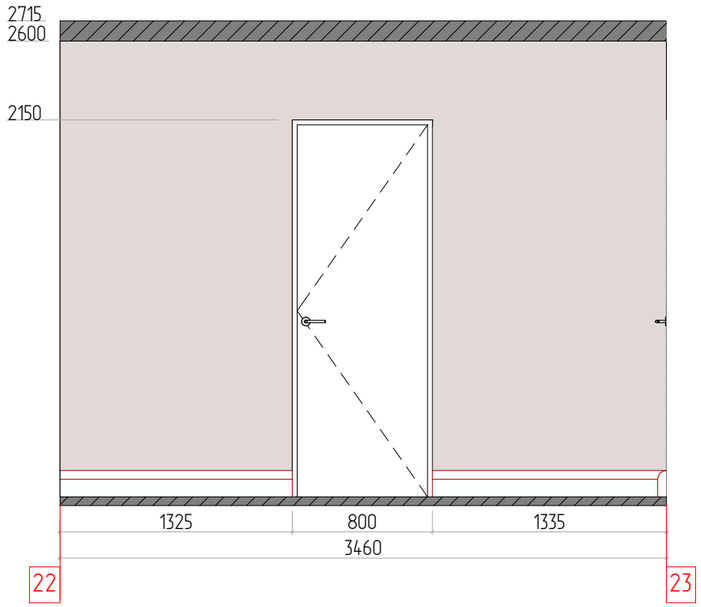

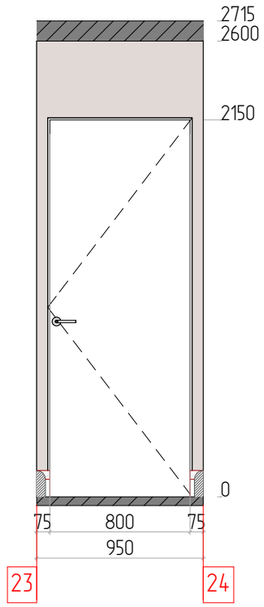

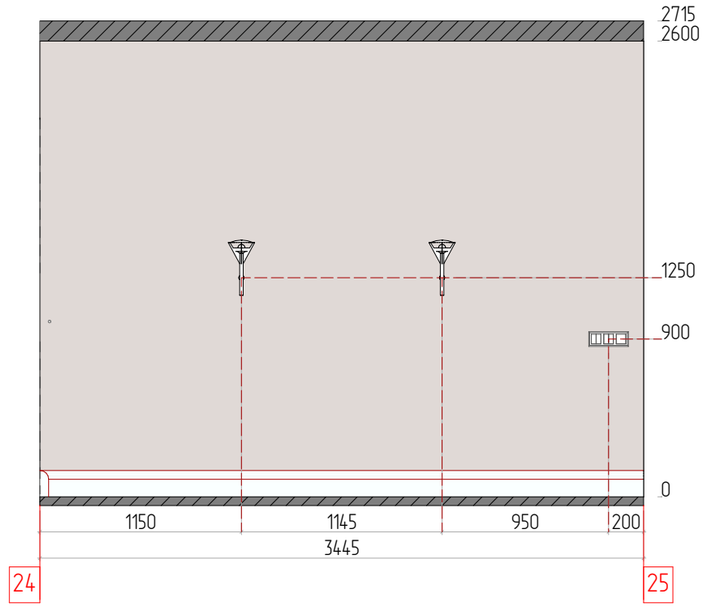

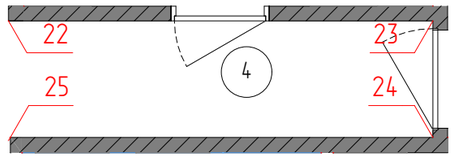


Расход материалов. Коридор			
Наименование	Условное обозначение	Площадь, кв.м (без запаса)	Примечание
Декоративная штукатурка		16,93	


Примечание:


1. Количество материала для отделки стен дано без запаса.
2. Пересчитать все материалы перед заказом с менеджером бренда (используя данные проекта).
3. Согласовать все размеры при заказе мебели.


дизайнер	Шинкевич Екатерина	Дизайн-проект квартиры по адресу: адрес	Масштаб 1:35	Стадия	Лист	Листов
				РП	19	28
телефон	+7 (931) 271-59-56			SHEM		

Развертки по стенам. Ванная

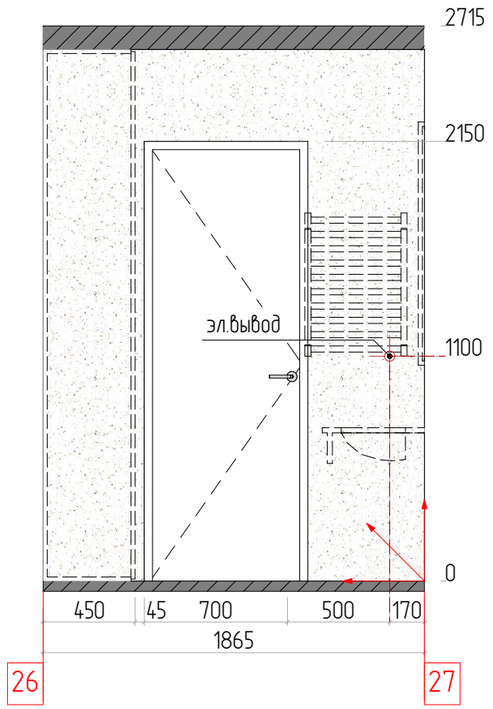


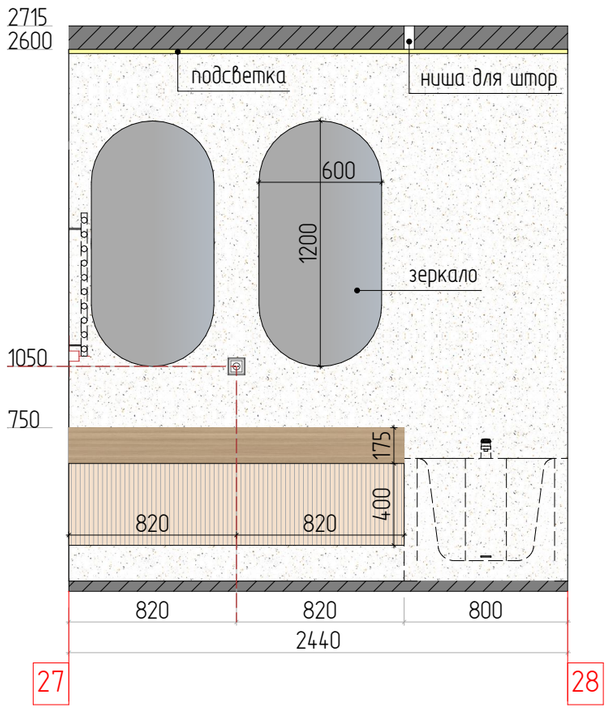


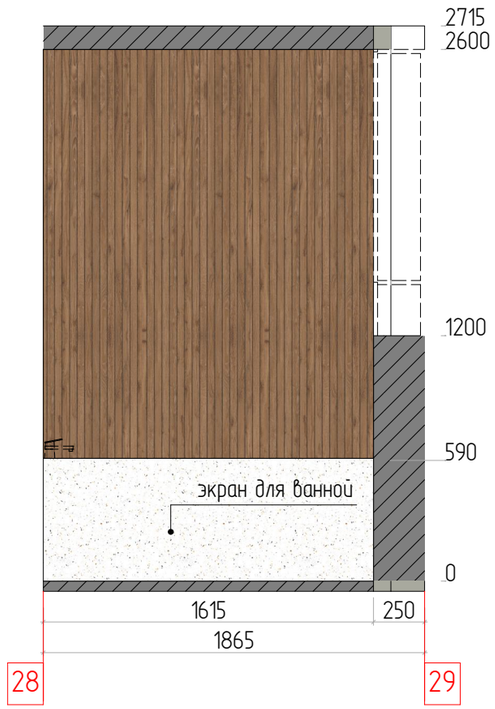

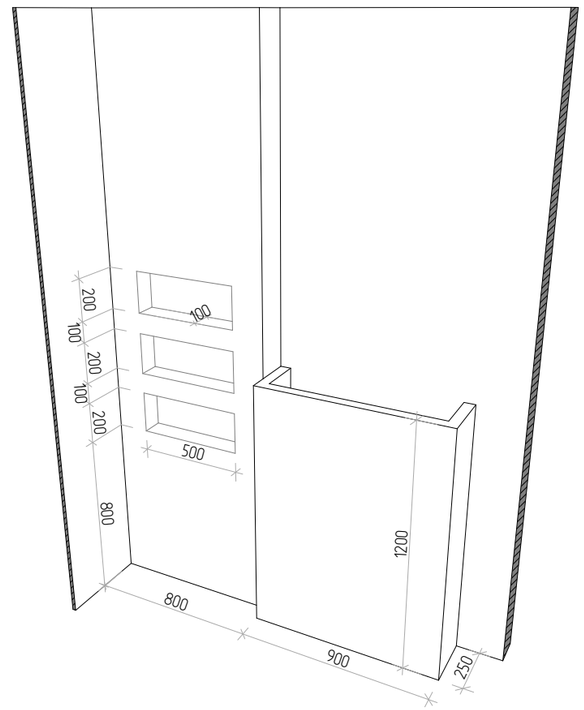

Устройство ниш и инсталляции в ванной

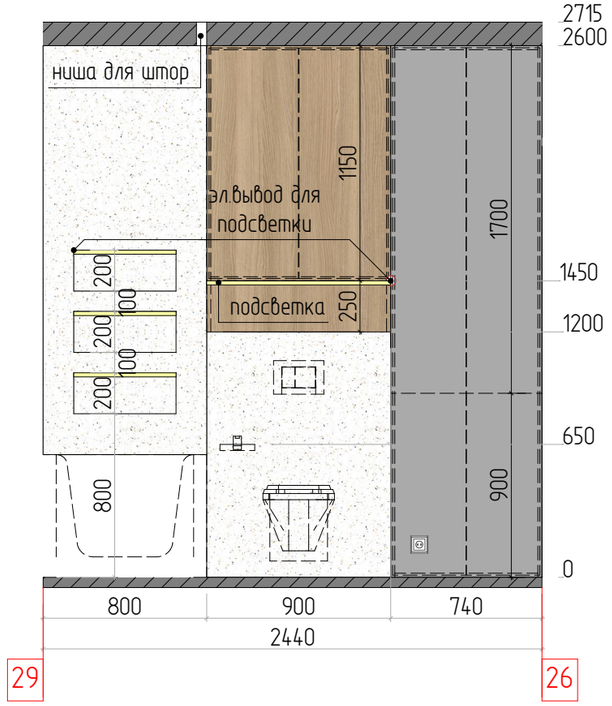

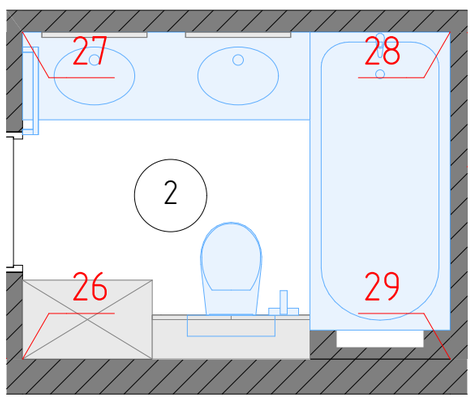


Расход материалов. Ванная			
Наименование	Условное обозначение	Площадь, кв.м (без запаса)	Примечание
K-340/MR		15,55	60x120
Керамогранит Kolan_GT		3,23	Беж. 60x120


Примечание:


1. Количество материала для отделки стен дано без запаса.
2. Пересчитать все материалы перед заказом с менеджером бренда (используя данные проекта).
3. Согласовать все размеры при заказе мебели.


дизайнер	Шинкевич Екатерина	Дизайн-проект квартиры по адресу: адрес	Масштаб 1:30	Стадия	Лист	Листов
				РП	20	28
телефон	+7 (931) 271-59-56			SHEM		


Развертки по стенам. Детская

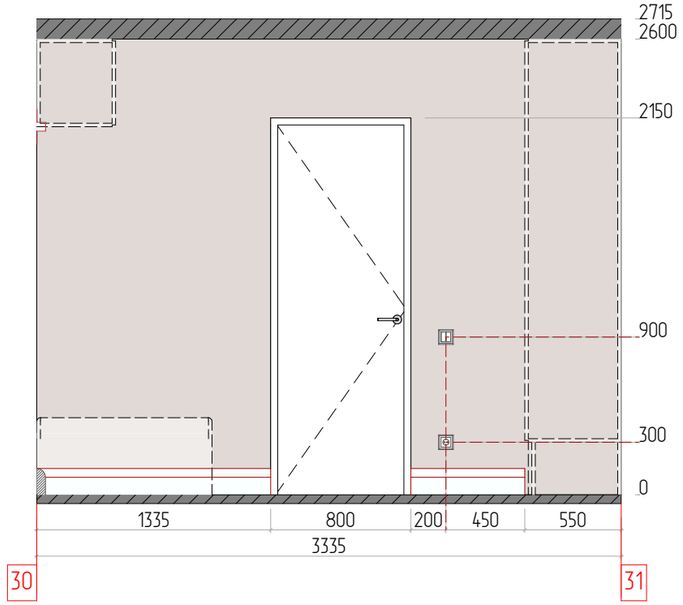

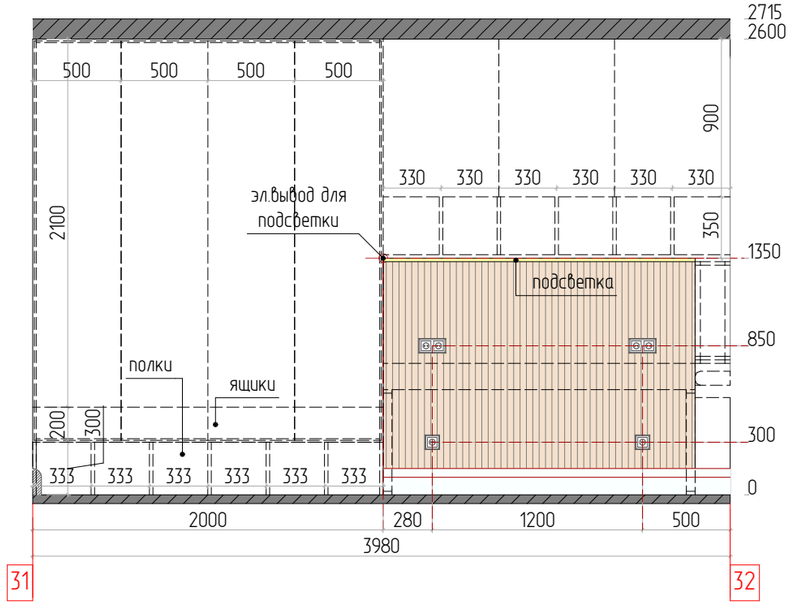

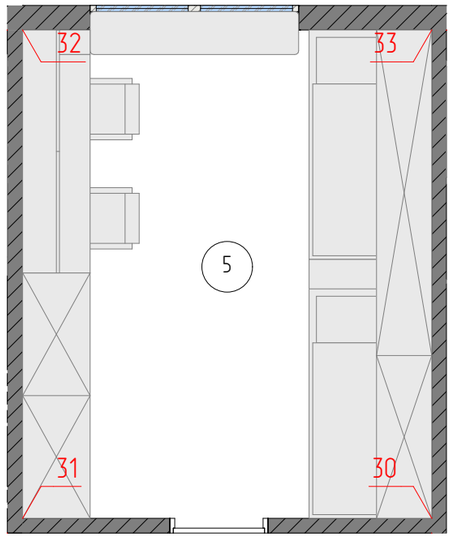

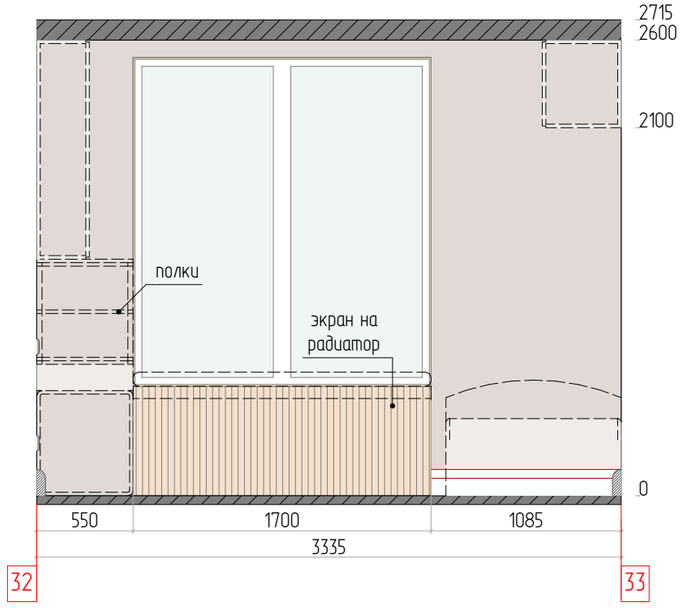

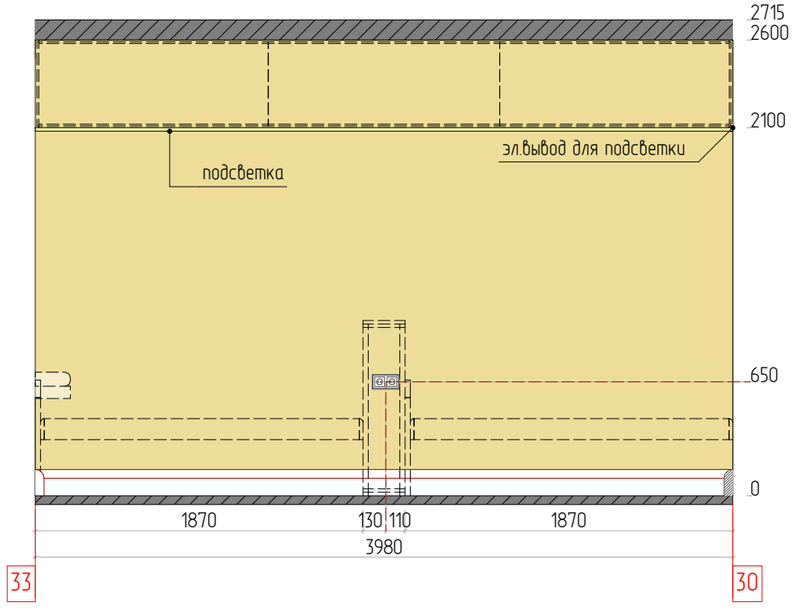


Расход материалов. Детская			
Наименование	Условное обозначение	Площадь, кв.м (без запаса)	Примечание
Декоративная штукатурка		12,43	детская
Деревянные рейки		2,40	
Фреска		10,35	


Примечание:


1. Количество материала для отделки стен дано без запаса.
2. Пересчитать все материалы перед заказом с менеджером бренда (используя данные проекта).
3. Согласовать все размеры при заказе мебели.


дизайнер	Шинкевич Екатерина	Дизайн-проект квартиры по адресу: адрес	Масштаб 1:35	Стадия	Лист	Листов
				РП	21	28
телефон	+7 (931) 271-59-56			SHEM		


Развертки по стенам. Спальня

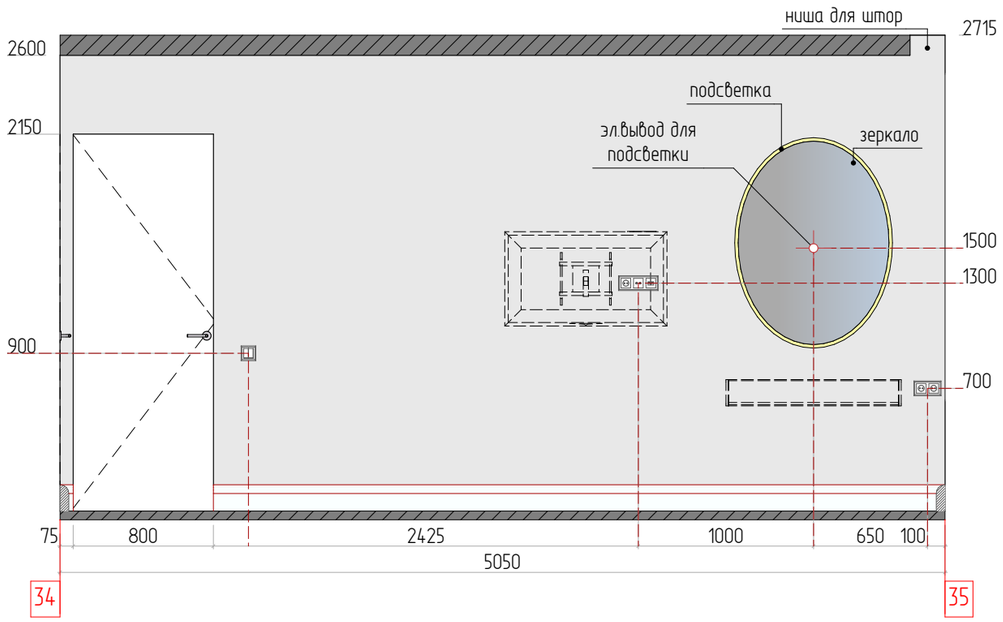

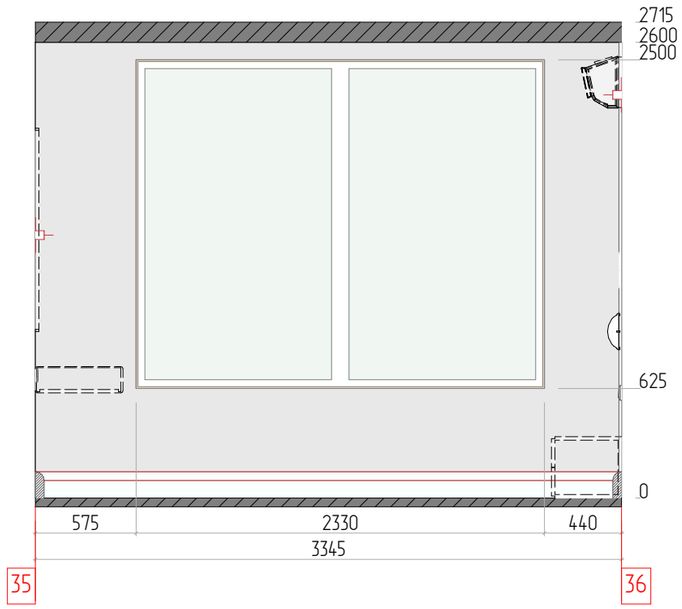

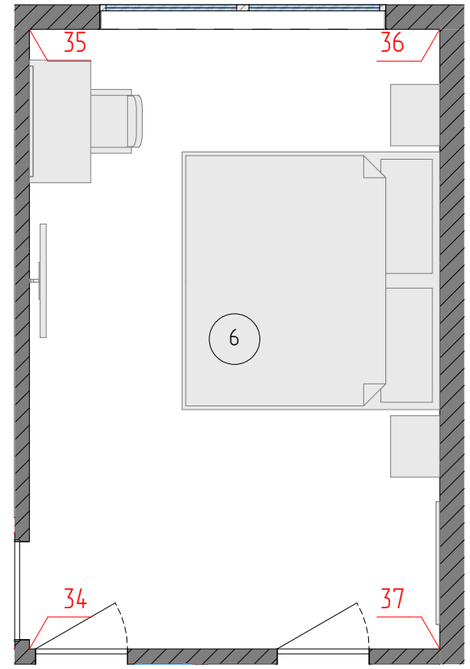

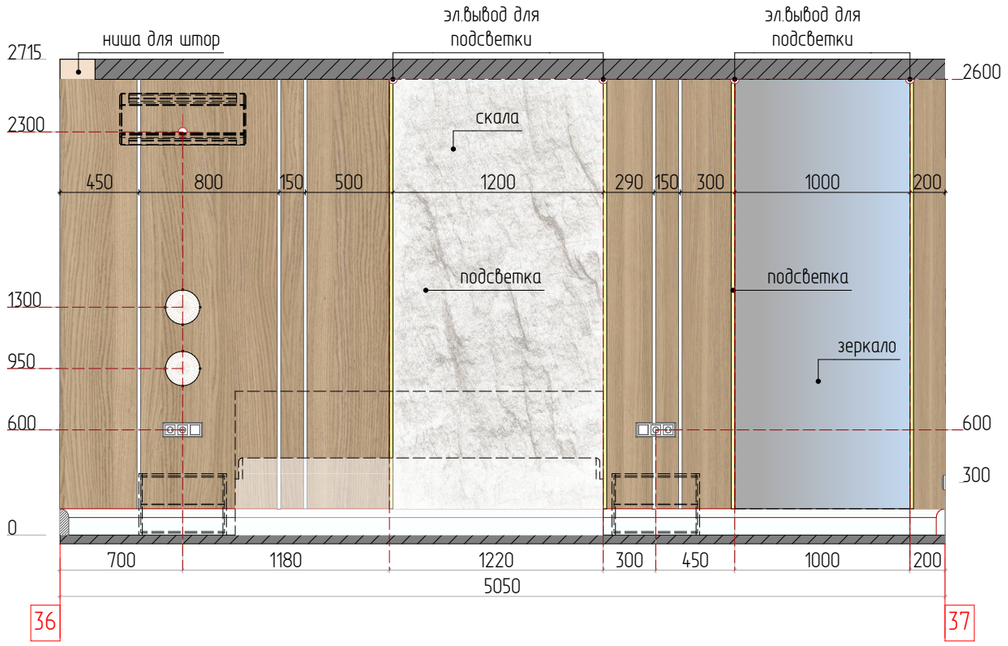

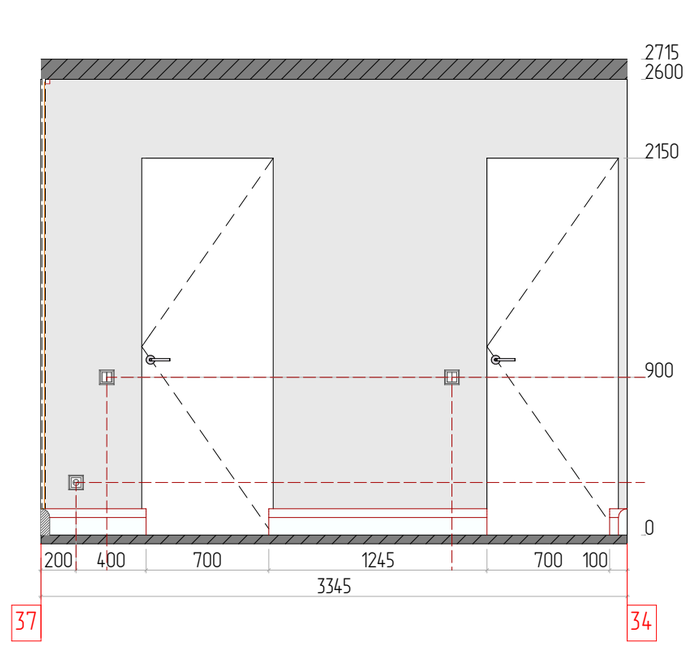


Расход материалов. Спальня			
Наименование	Условное обозначение	Площадь, кв.м (без запаса)	Примечание
Декоративная штукатурка		21,45	
Деревянные панели		10,03	
Скала		3,12	


Примечание:


1. Количество материала для отделки стен дано без запаса.
2. Пересчитать все материалы перед заказом с менеджером бренда (используя данные проекта).
3. Согласовать все размеры при заказе мебели.


дизайнер	Шинкевич Екатерина	Дизайн-проект квартиры по адресу: адрес	Масштаб 1:55, 1:35	Стадия	Лист	Листов
				РП	22	28
телефон	+7 (931) 271-59-56			SHEM		

Развертки по стенам. Душевая

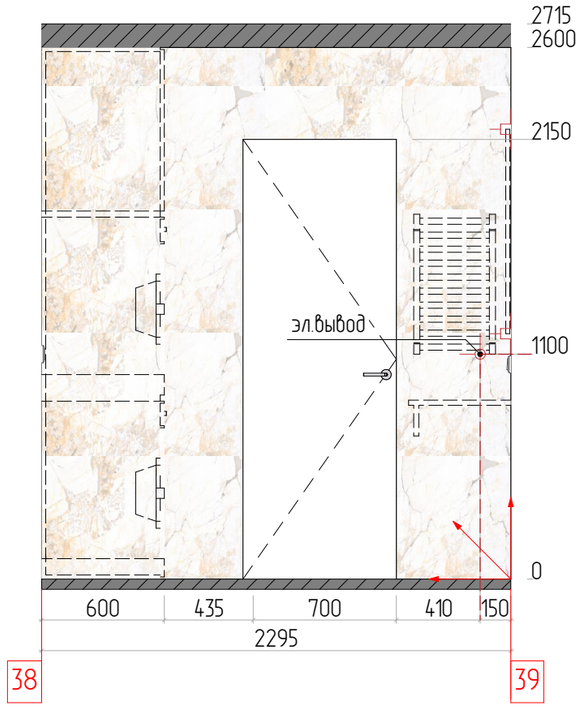

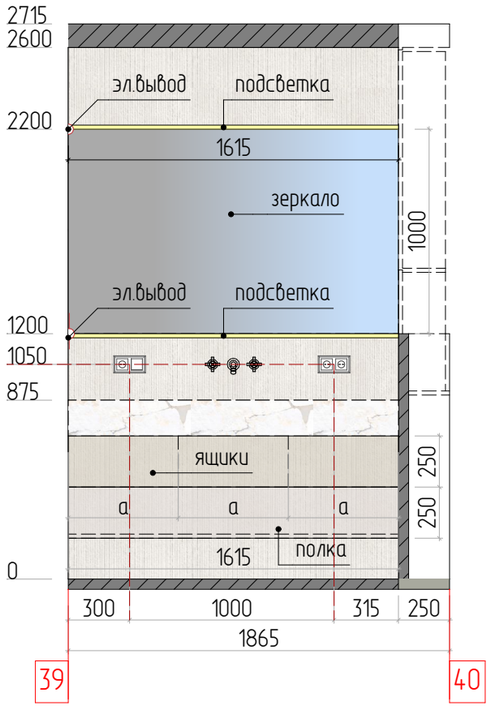


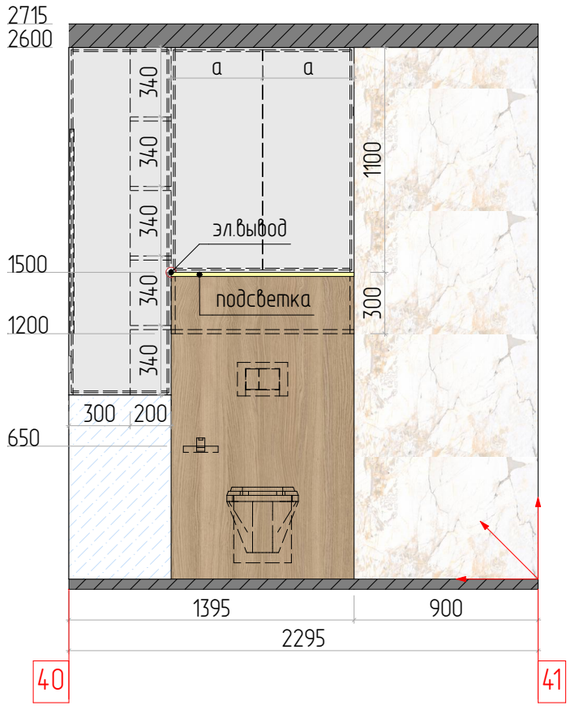

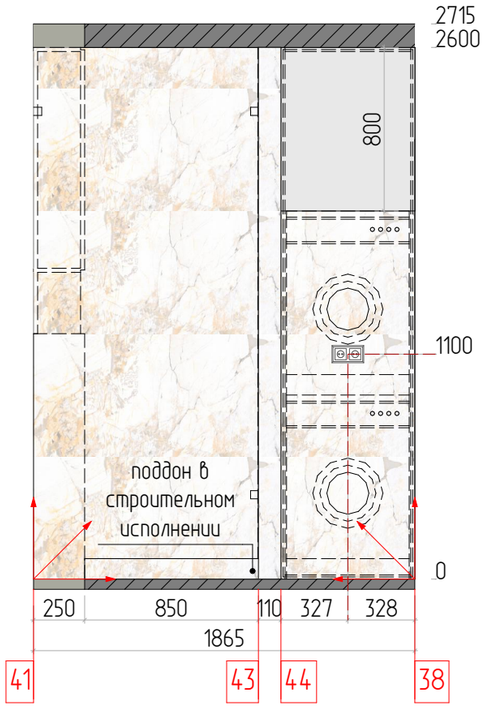





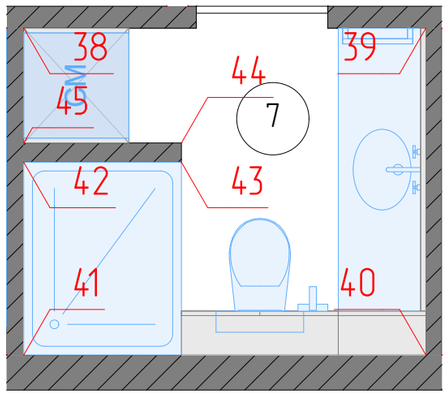


Расход материалов. Душевая			
Наименование	Условное обозначение	Площадь, кв.м (без запаса)	Примечание
Керамогранит Harmony_GT		4,20	Светло-беж. 60х120
Керамогранит Laurent_GT		16,22	Белый 60х120


Примечание:


1. Количество материала для отделки стен дано без запаса.
2. Пересчитать все материалы перед заказом с менеджером бренда (используя данные проекта).
3. Согласовать все размеры при заказе мебели.


дизайнер	Шинкевич Екатерина	Дизайн-проект квартиры по адресу: адрес	Масштаб 1:30	Стадия	Лист	Листов
				РП	23	28
телефон	+7 (931) 271-59-56			SHEM		


Развертки по стенам. Гардеробная

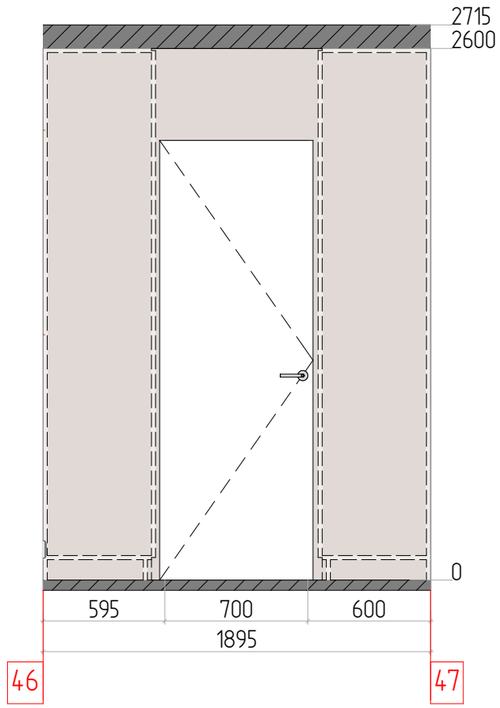

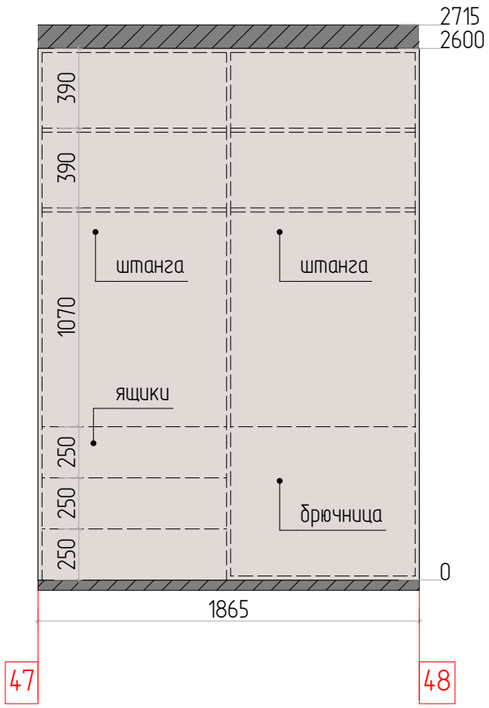

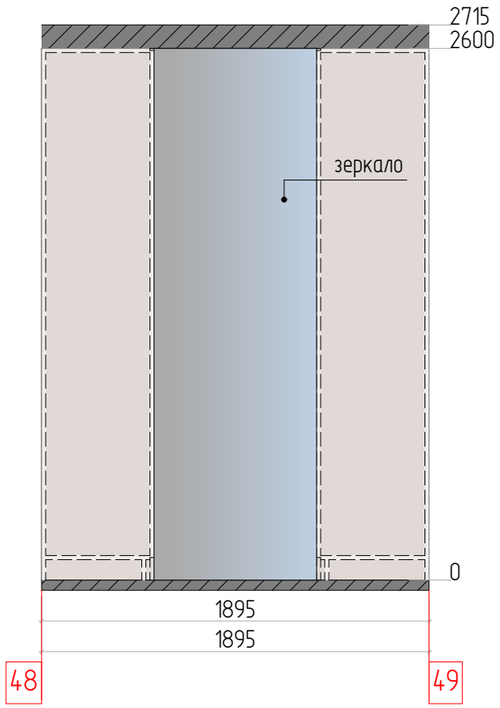

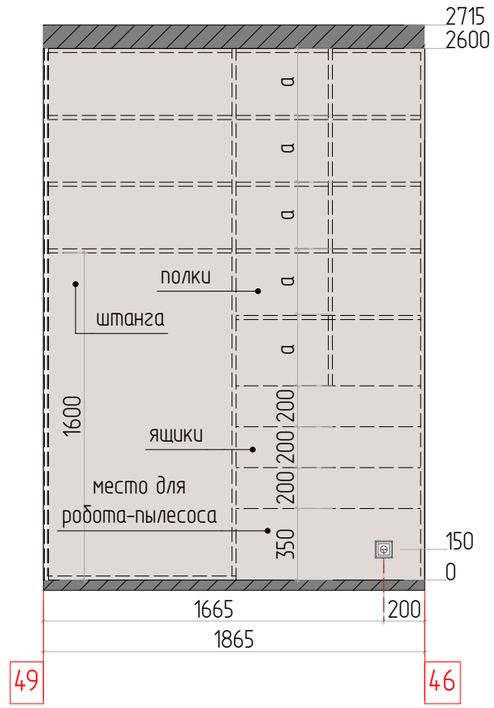

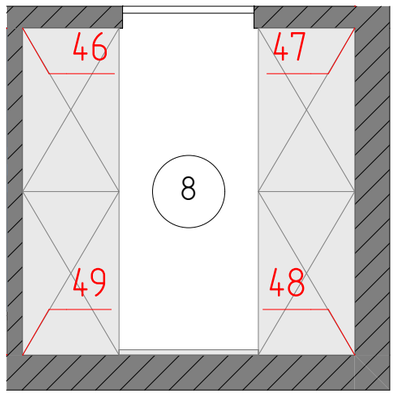


Расход материалов. Гардеробная			
Наименование	Условное обозначение	Площадь, кв.м (без запаса)	Примечание
Покраска		18,05	

Примечание:

1. Количество материала для отделки стен дано без запаса.
2. Пересчитать все материалы перед заказом с менеджером бренда (используя данные проекта).
3. Согласовать все размеры при заказе мебели.

дизайнер	Шинкевич Екатерина	Дизайн-проект квартиры по адресу: адрес	Масштаб 1:30	Стадия	Лист	Листов
				РП	24	28
телефон	+7 (931) 271-59-56			SHEM		

Спецификация дверей с указанием размеров дверных проемов

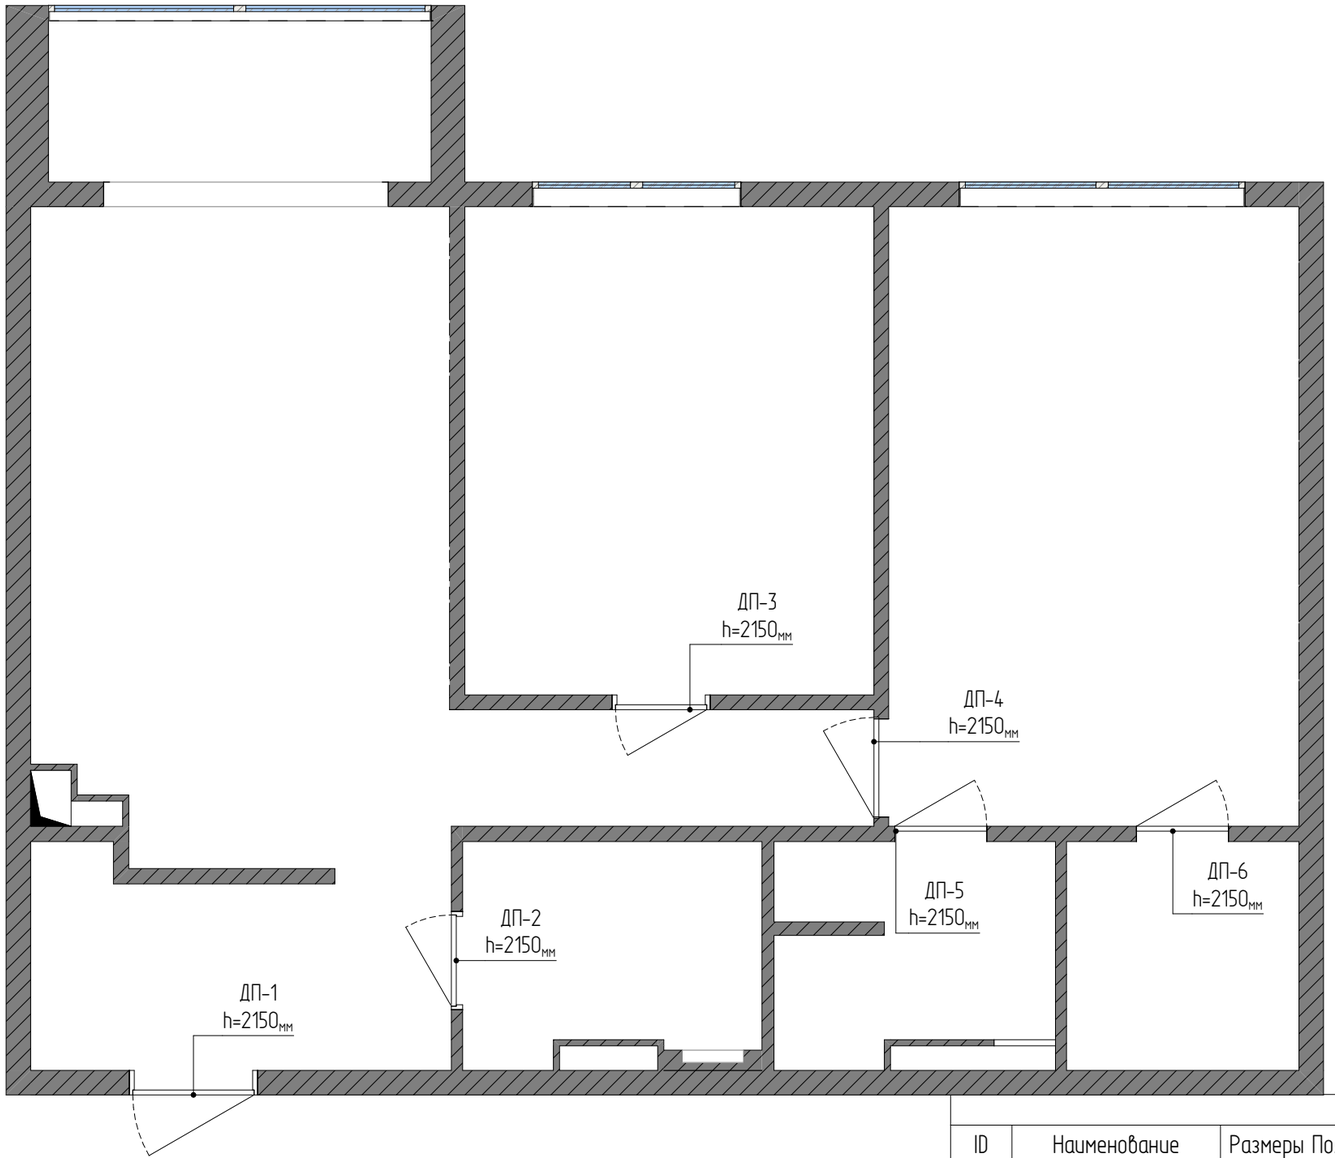

Специцикация дверей



ID	Наименование	Размеры Полотна	Размеры проёма	Открывание	Толщина стены, мм	Расположение	Количество	Примечание
ДП-1	Входная дверь	989×2122	1045×2150	П	200	входная группа	1	
ДП-2	Межкомнатная дверь	744×2122	800×2150	П	92	ванная	1	скрытая дверь
ДП-3	Межкомнатная дверь	744×2122	800×2150	П	120	детская	1	скрытая дверь
ДП-4	Межкомнатная дверь	824×2162	800×2150	П	120	спальня	1	скрытая дверь
ДП-5	Межкомнатная дверь	750×2150	750×2150	П	125	душевая	1	скрытая дверь
ДП-6	Межкомнатная дверь	750×2150	750×2150	П	125	гардеробная	1	скрытая дверь

Примечание:

1. Высота дверного проема указанна от чистового пола.
2. Накладка на входную дверь, идентичная с межкомнатными дверями.


дизайнер	Шинкевич Екатерина	Дизайн-проект квартиры по адресу: адрес	Масштаб 1:50	Стадия	Лист	Листов
				РП	25	28
телефон	+7 (931) 271-59-56			SHEM		

Спецификация мебели







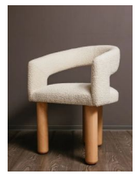
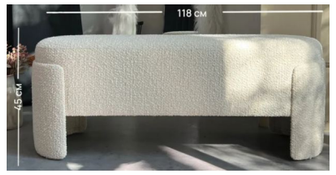
№	Тип мебели	Артикул	Производитель	Наименование	QR-код	Изображение	Кол-во	Наименование помещения	Примечание
	журнальный столик	1587479378	Etta Design	Сигма Лофт			1	лоджия	Цвет: Рыжий дуб
	кресло	876546088	Alpina-Market	PECOLA			1	спальня	Цвет: молочный, Buckle Cream + тон натуральное дерево
	пуф	1313763443	Mebel Made	White Polly maxi			1	прихожая	Цвет: BUCKLE white
	кресло	1223886326	Stool Group	Ричи			2	лоджия	
	стол	дуб	Deephouse	Стокгольм			1	кухня-столовая	
	стул	1746778806	Дружный дешевый-D4	стул			2	кухня-столовая	Цвет: светло-коричневый
	журнальный столик	1573185237	Steel dekor	столик			1	кухня-столовая	Цвет: черный

дизайнер	Шинкевич Екатерина	Дизайн-проект квартиры по адресу: адрес	Масштаб	Стадия: РП; Лист: 26; Листов: 28
телефон	+7 (931) 271-59-56			SHEM

Спецификация осветительного оборудования

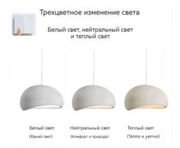ID	Тип светильника	Артикул	Производитель	Наименование	QR-код	Изображение	Количество	Расположение	Примечание
C01	настенный светильник	5678	DESIGN STORE	Odeon Light			2	коридор	цвет чёрный
C01	настенный светильник	1555983306	DESIGN STORE	Odeon Light			2	спальня	
C02	подвесной светильник	s158961-205	Freya	Moth FR5392PL-01W			1	спальня	цвет белые
C02	подвесной светильник	s158962-737	Freya	Moth FR5392PL-01W1			1	спальня	цвет белые
C02	подвесной светильник	1223985348	TRAVERTINO	Odeon Light			2	прихожая	
C03	люстра	1611630349	RONGCHENLighting	подвесной светильник			1	кухня-гостиная	Цвет: белый, серый

дизайнер	Шинкевич Екатерина	Дизайн-проект квартиры по адресу: адрес	Масштаб	Стадия	Лист	Листов
				РП	27	28
телефон	+7 (931) 271-59-56			SHEM		

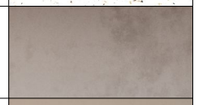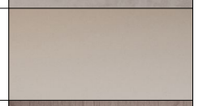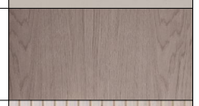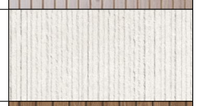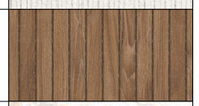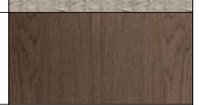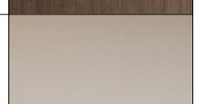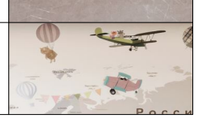Спецификация отделочных материалов стен			
Наименование	Площадь, кв.м (без запаса)	Примечание	Изображение
К-340/MR	15,55	60х120	
Декоративная штукатурка	12,43	детская	
Декоративная штукатурка	71,43		
Деревянные панели	10,03		
Деревянные рейки	2,40		
Керамогранит Harmony_GT	4,20	Светло-беж. 60х120	
Керамогранит Kolan_GT	3,23	Беж. 60х120	
Керамогранит Laurent_GT	16,22	Белый 60х120	
Краска техническая	21,21		
Панели декоративные	1,30		
Панели деревянные	1,15		
Покраска	18,05		
Скала	3,12		
Фартук	6,20		
Фреска	10,35		

Спецификация потолков и полов			
ID	Наименование	Площадь, кв.м (без запаса)	Примечание
01	Натяжной потолок	70,45	
02	Штукатурка и покраска	2,06	
п01	Кварцвинил	65,33	укладка "ёлочкой"
п02	К-340	4,23	120х60
п03	Керамогранит Laurent_GT	3,88	120х60

LED лента			
ID	Условное обозначение	Наименование	Длина, мм
С01		подсветка зеркала	3615
С02		"парящий" потолок	13635
С03		подсветка ниш	2295
С04		подсветка рабочей зоны	1780
С05		подсветка полок	3980
С06		вертикальная подсветка	9800
			35105 мм

Спецификация карнизов/молдингов/плинтусов			
ID	Наименование	Длина, мм	Примечание
М01	Молдинг	20700	широкий
М02	Молдинг	17100	узкий
М03	Теневой профиль	12256	
П01	Плинтус	42920	

дизайнер	Шинкевич Екатерина	Дизайн-проект квартиры по адресу: адрес	Масштаб	Стадия	Лист	Листов
				РП	28	28
телефон	+7 (931) 271-59-56			SHEM		