
SHEM

ШИНКЕВИЧ ЕКАТЕРИНА

дизайнер интерьеров

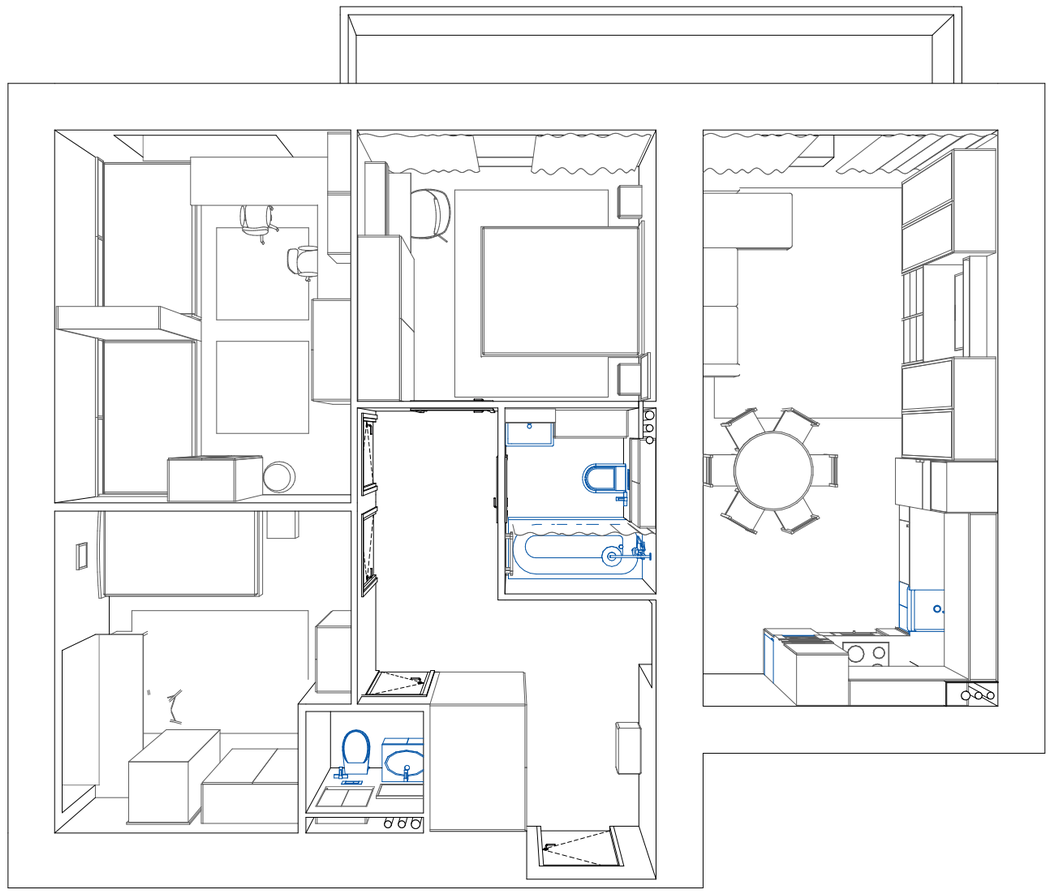

Дизайн-проект квартиры: рабочий проект

ОБЪЕКТ :	наименование
ЗАКАЗЧИК :	заказчик
МЕСТОРАСПОЛОЖЕНИЕ ОБЪЕКТА :	адрес
ТЕЛЕФОН ЗАКАЗЧИКА :	телефон

2024

Общие данные

Лист	Наименование	Примечание
01	Общие данные	
02	План обмеров	
03	План возводимых перегородок с маркировкой дверных проемов	
04	Спецификация дверей с указанием размеров дверных проемов	
05	План после перепланировки	
06	План расстановки мебели	
07	План с мебельными размерами и описанием	
08	План размещения осветительных приборов, привязка выпусков освещения	
09	План выключателей с указанием включения групп светильников	
10	План размещения электрических розеток с привязкой размеров	
11	План полов с указанием типа напольных покрытий	
12	План потолков с указанием типа используемых материалов	
13	План расположения систем отопления и вентиляции	
14	План размещения санитарно-технического оборудования	

Лист	Наименование	Примечание
15	План отделочных материалов по стенам	
16	Развертки по стенам. Прихожая	
17	Развертки по стенам. Прихожая	
18	Развертки по стенам. Санузел	
19	Развертки по стенам. Детская мальчики	
20	Развертки по стенам. Детская девочки	
21	Развертки по стенам. Спальня	
22	Развертки по стенам. Ванная	
23	Развертки по стенам. Кухня-гостиная	
24	Развертки по стенам. Кухня-гостиная	
25	Коллаж. Спальня	
26	Коллаж. Санузел	
27	Коллаж. Кухня	
28	Коллаж. Кухня-гостиная	

Лист	Наименование	Примечание
29	Коллаж. Ванная	
30	Мебель на заказ	
31	Мебель на заказ	
32	Мебель на заказ	
33	Мебель на заказ	
34	Мебель на заказ	
35	Спецификация осветительного оборудования	
36	Спецификация мебели	
37	Спецификация мебели	
38	Спецификация мебели	
39	Спецификация мебели	
40	Спецификация сантехнического оборудования	
41	Спецификация отделочных материалов	

ПОЯСНИТЕЛЬНАЯ ЗАПИСКА

К дизайн-проекту интерьера квартиры, расположенной по адресу: адрес
Проект выполнен на основании обмеров. Квартира имеет общую площадь: 85,97м^2

Благоустройство квартиры: централизованная система отопления, система очистки воды, электроснабжение, центральная канализация, бойлер.
Наружные стены – кирпич. Внутренние стены – кирпич.

Необходимо произвести следующие работы:
1. Возвести новые конструкции согласно РП-03;
1. Устроить потолки согласно РП-12;
2. Выполнить электропроводку согласно РП-08, РП-09, РП-10;
3. Полы устроить согласно РП-11;
4. Произвести отделку согласно РП-15, РП-16-РП-24.

Проект квартиры полностью удовлетворяет пожеланиям Заказчика.

Дизайнер	Екатерина Шинкевич	Дизайн-проект квартиры по адресу:	Общие данные	Стадия	Лист	Листов
				РП	01	26
Телефон	+7 (931) 271-59-56	адрес	Масштаб	SHEM		

План обмеров




Экспликация помещений на этапе обмеров		
№	Название помещения	Площадь, кв.м
1	Коридор	12,27
2	Санузел	1,88
3	Комната 1	11,68
4	Комната 2	14,55
5	Комната 3	10,69
6	Ванная	3,70
7	Кухня-гостиная	22,39
8	Лоджия	8,82
		85,98 м²

Примечание:

1. Все размеры укзаны в мм.
2. Обмерный план выполнен на основании обмеров. Погрешность составляет не более 30мм.
3. Зоны коммуникаций обрамерены по выступающим частям и показаны условно.


Дизайнер	Екатерина Шинкевич	Дизайн-проект квартиры по адресу:	План обмеров	Стадия	Лист	Листов
				РП	02	26
Телефон	+7 (931) 271-59-56	адрес	Масштаб 1:50	SHEM		

План возводимых перегородок с маркировкой дверных проемов

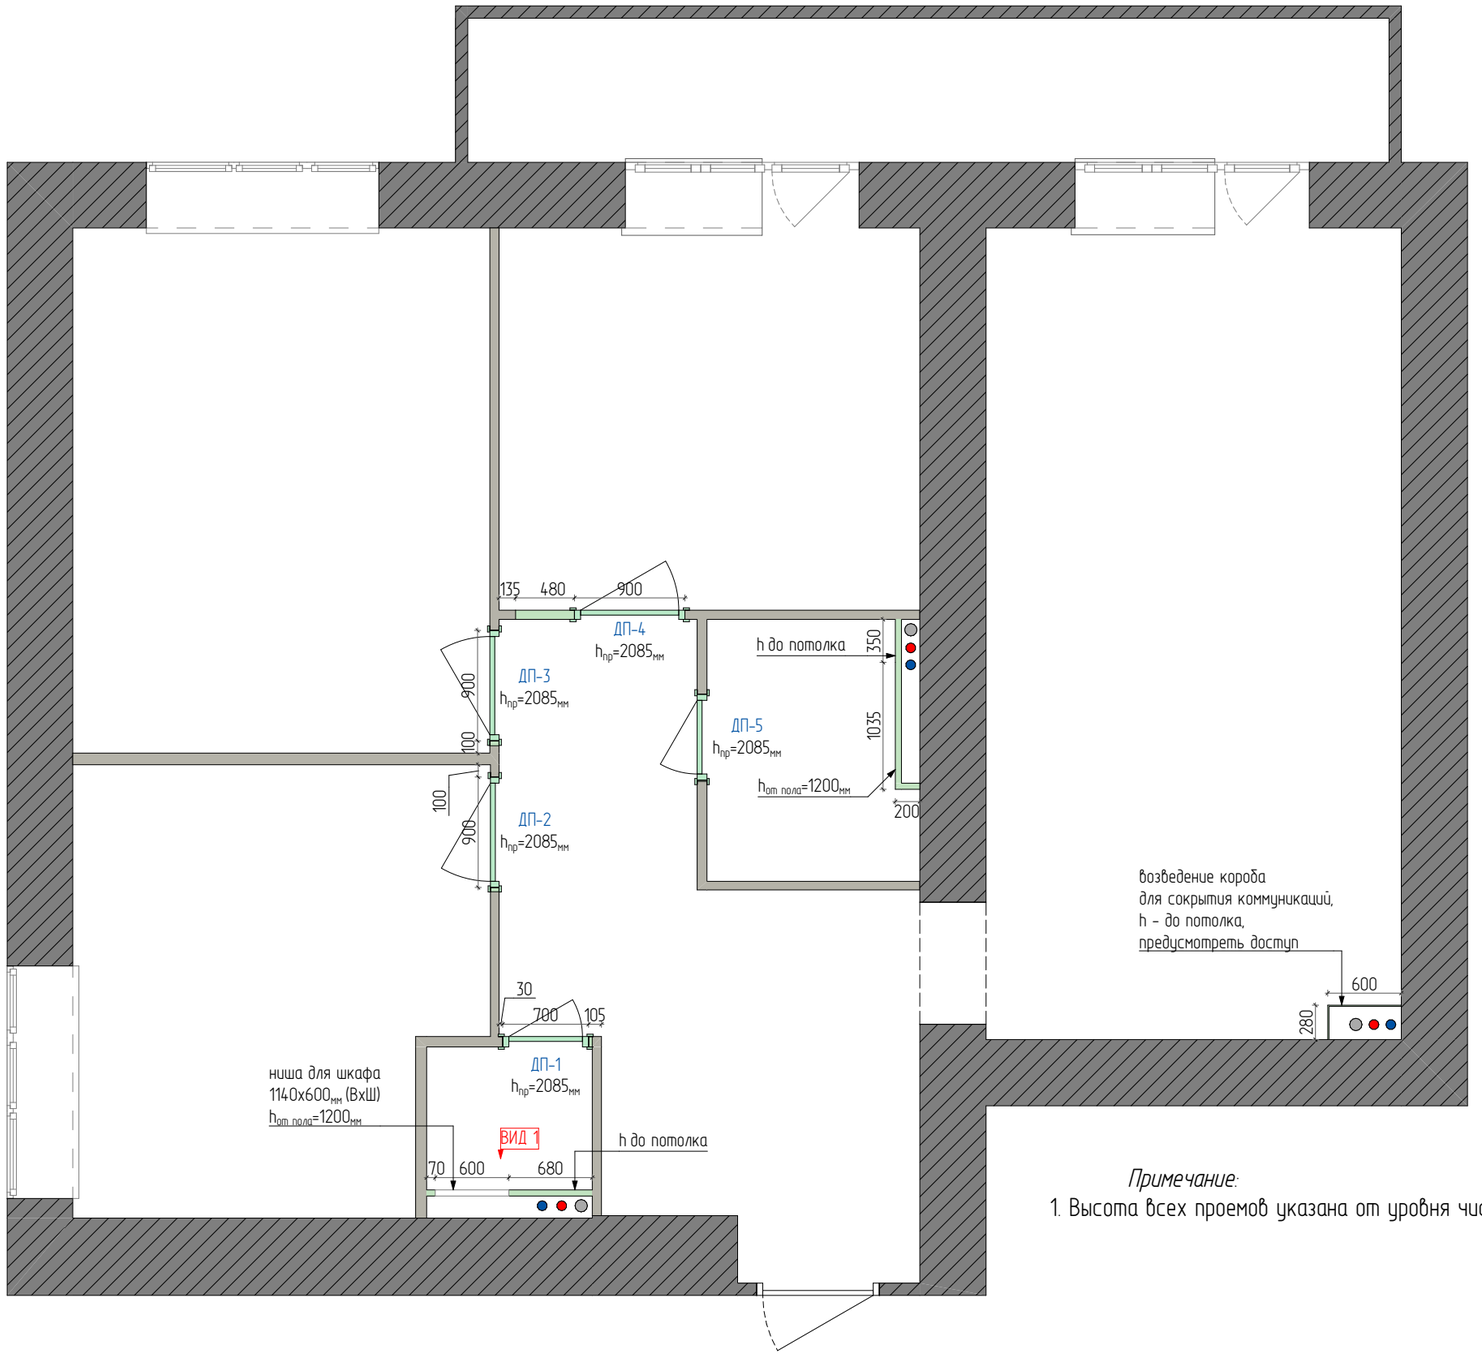

Условные обозначения:

- существующие перегородки
- новые возводимые конструкции

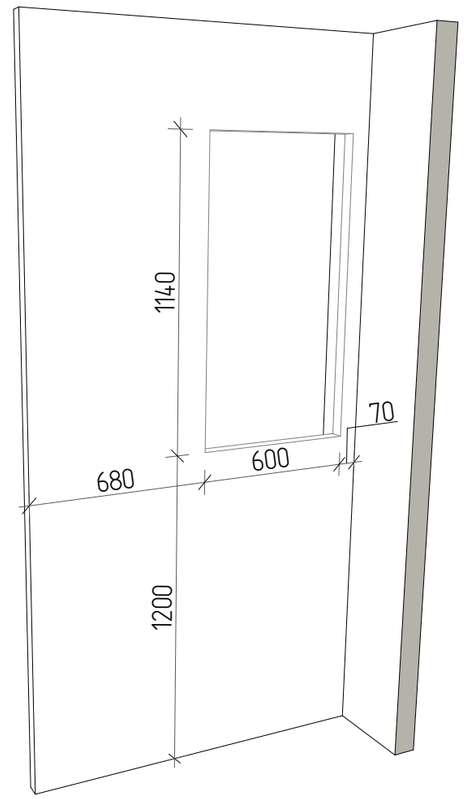

ВИД 1
Ниша для шкафчика

Примечание:

1. Высота всех проемов указана от уровня чистового пола.

Дизайнер	Екатерина Шинкевич	Дизайн-проект квартиры по адресу:	План возводимых перегородок с маркировкой дверных проемов	Стадия	Лист	Листов
				РП	03	26
Телефон	+7 (931) 271-59-56	адрес	Масштаб 1:50, 1:211,55	SHEM		

Спецификация дверей с указанием размеров дверных проемов



Спецификация дверей									
ID	Наименование	Размеры полотна	Размеры проёма	Артикул	Открывание	Толщина стены, мм	Кол-во	Расположение	Примечание
ДП-1	Дверь межкомнатная Каролина	600×2000	700×2085	91600569 (lemanapro.ru)	П	85	1	санузел	эмаль белая
ДП-2	Дверь межкомнатная Каролина	800×2000	900×2085	91600571 (lemanapro.ru)	Л	70	1	детская мальчики	эмаль белая
ДП-3	Дверь межкомнатная Каролина	800×2000	900×2085	91600571 (lemanapro.ru)	П	75	1	детская девочки	эмаль белая
ДП-4	Дверь межкомнатная Каролина	800×2000	900×2085	91600571 (lemanapro.ru)	П	75	1	спальня	эмаль белая
ДП-5	Дверь межкомнатная Каролина	600×2000	700×2085	91600569 (lemanapro.ru)	Л	80	1	ванная	эмаль белая



Ручка дверная межкомнатная BUSSARE CANTO ERA A-21-50 матовый хром 905656387 (ozon.ru)




Дверь межкомнатная Двери регионов Каролина глухая без замка и петель в комплекте

Примечание:

1. Высота дверного проема указана от чистового пола.
2. Цвет дверей - эмаль белая.
3. Все размеры уточнить по месту.

Дизайнер	Екатерина Шинкевич	Дизайн-проект квартиры по адресу:	Спецификация дверей с указанием размеров дверных проемов	Стадия: РП; Лист: 04; Листов: 26
Телефон	+7 (931) 271-59-56	адрес	Масштаб 1:70	SHEM

План после перепланировки

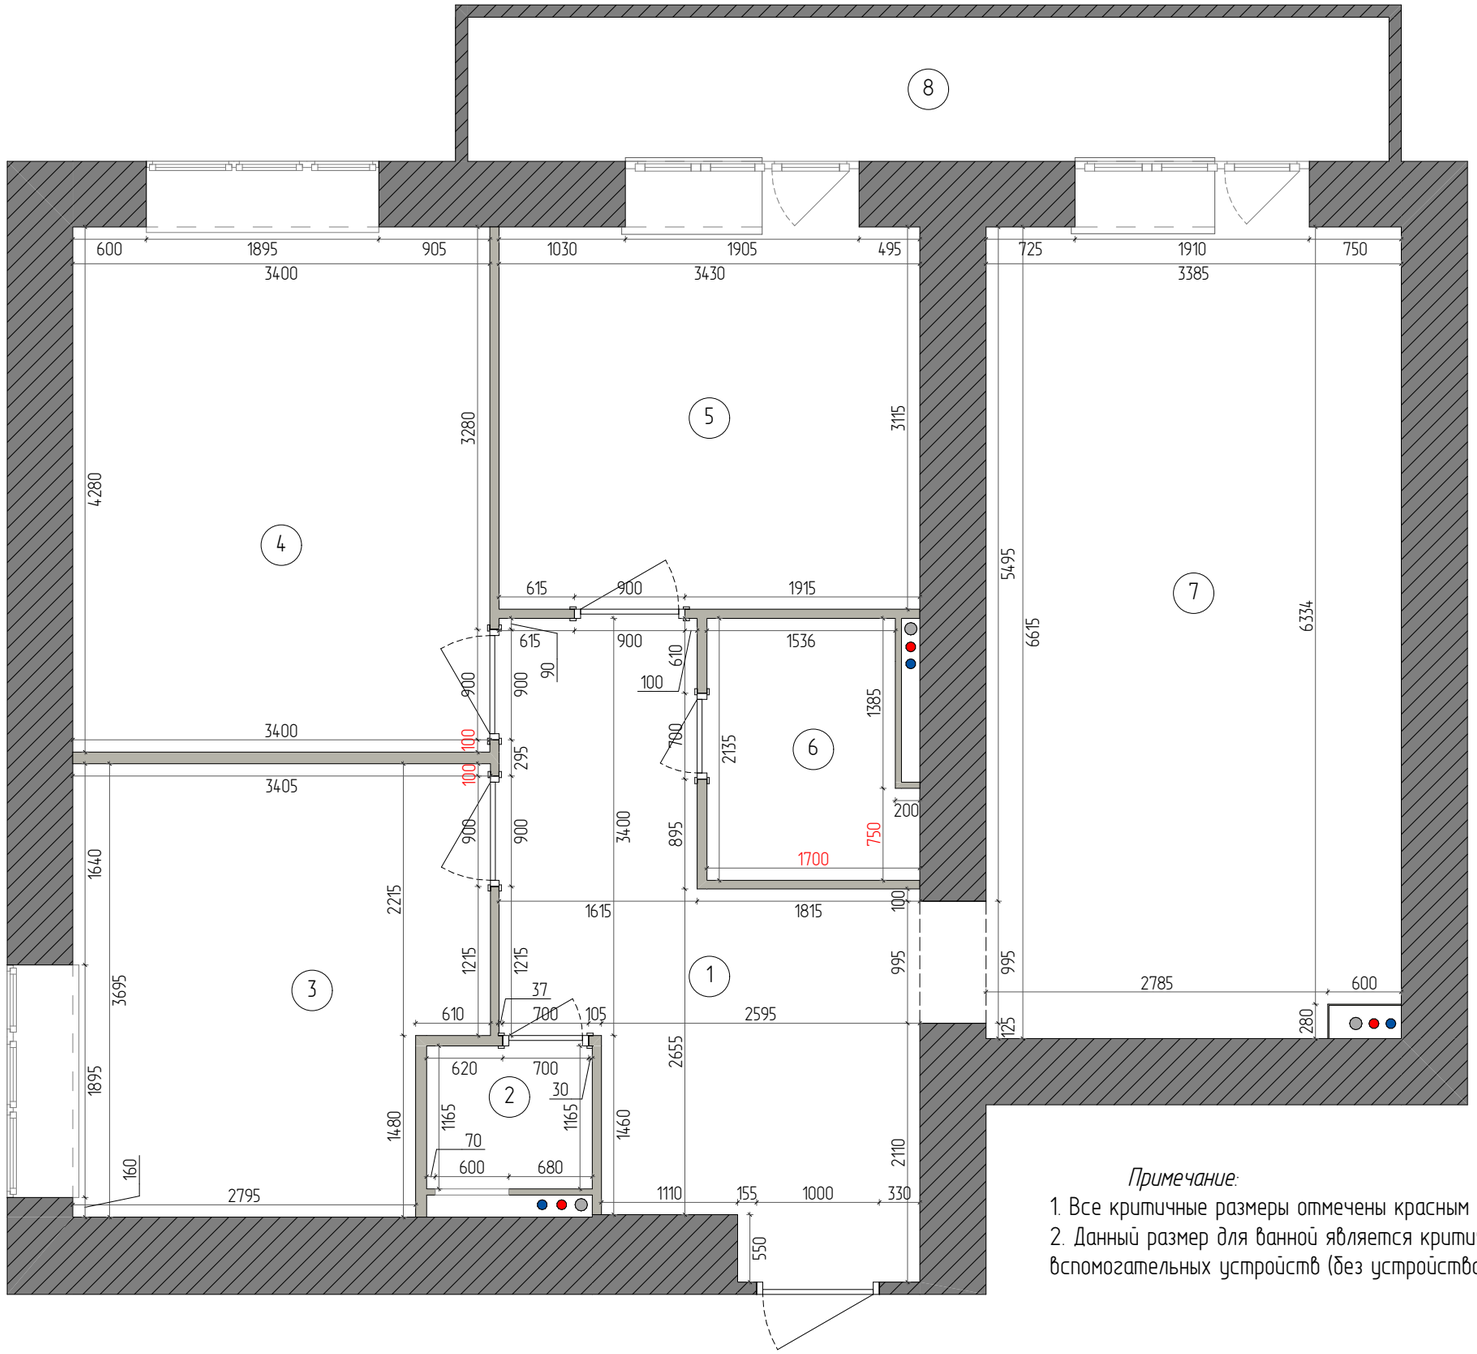


Экспликация помещений		
№	Название помещения	Площадь, кв.м
1	Коридор	12,27
2	Санузел	1,88
3	Детская мальчики	11,68
4	Детская девочки	14,55
5	Спальня	10,69
6	Ванная	3,70
7	Кухня-гостиная	22,25
8	Лоджия	8,82
		85,84 м²

Примечание:

1. Все критичные размеры отмечены красным на чертеже.
2. Данный размер для ванной является критичным. Выполнить выравнивание стен с учетом дальнейшей установки ванны без вспомогательных устройств (без устройства короба между стеной и ванной).

Дизайнер	Екатерина Шинкевич	Дизайн-проект квартиры по адресу:	План после перепланировки	Стадия	Лист	Листов
				РП	05	26
Телефон	+7 (931) 271-59-56	адрес	Масштаб 1:50	SHEM		

План расстановки мебели

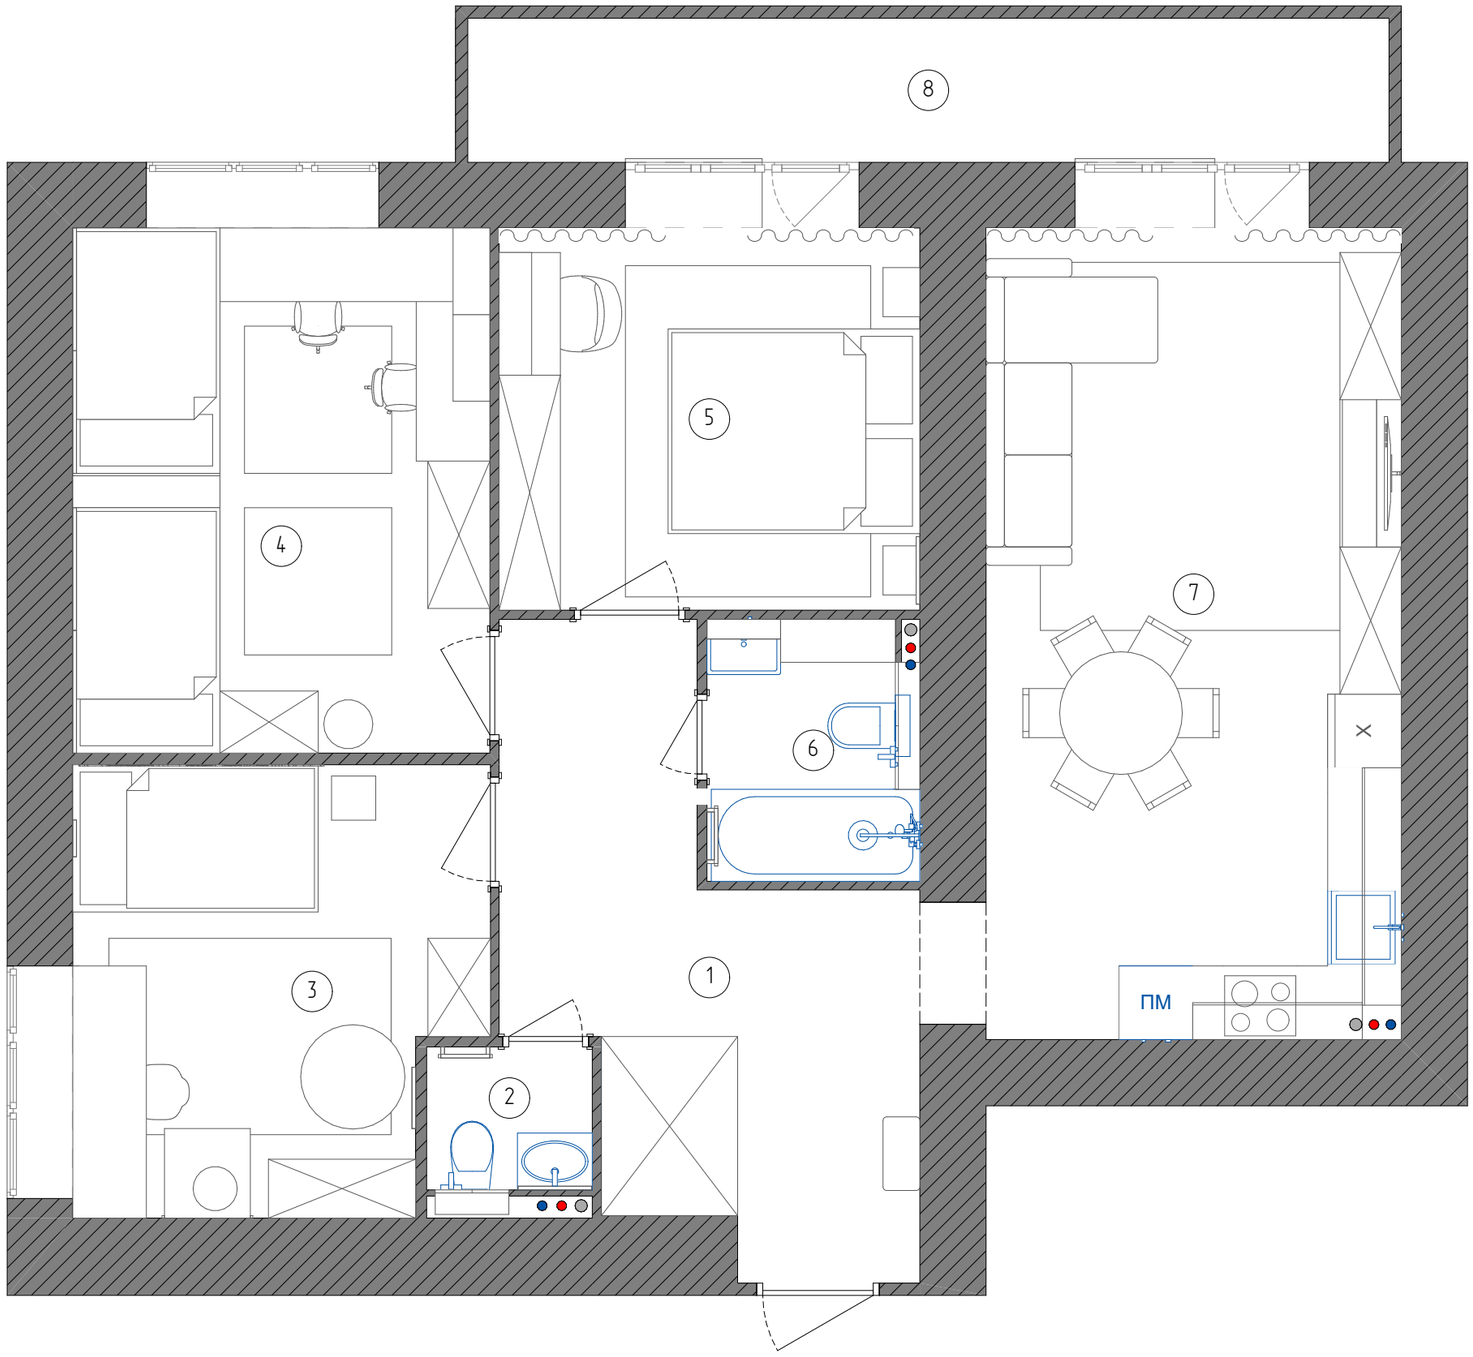

Экспликация помещений		
№	Название помещения	Площадь, кв.м
1	Коридор	12,27
2	Санузел	1,88
3	Детская мальчики	11,68
4	Детская девочки	14,55
5	Спальня	10,69
6	Ванная	3,70
7	Кухня-гостиная	22,25
8	Лоджия	8,82
		85,84 м²

Дизайнер	Екатерина Шинкевич	Дизайн-проект квартиры по адресу:	План расстановки мебели	Стадия	Лист	Листов
				РП	06	26
Телефон	+7 (931) 271-59-56	адрес	Масштаб 1:50	SHEM		


План с мебельными размерами и описанием



Экспликация помещений		
№	Название помещения	Площадь, кв.м
1	Коридор	12,27
2	Санузел	1,88
3	Детская мальчики	11,68
4	Детская девочки	14,55
5	Спальня	10,69
6	Ванная	3,70
7	Кухня-гостиная	22,25

Дизайнер	Екатерина Шинкевич	Дизайн-проект квартиры по адресу:	План с мебельными размерами и описанием	Стадия	Лист	Листов
				РП	07	26
Телефон	+7 (931) 271-59-56	адрес	Масштаб 1:50	SHEM		

План размещения осветительных приборов, привязка выпусков освещения

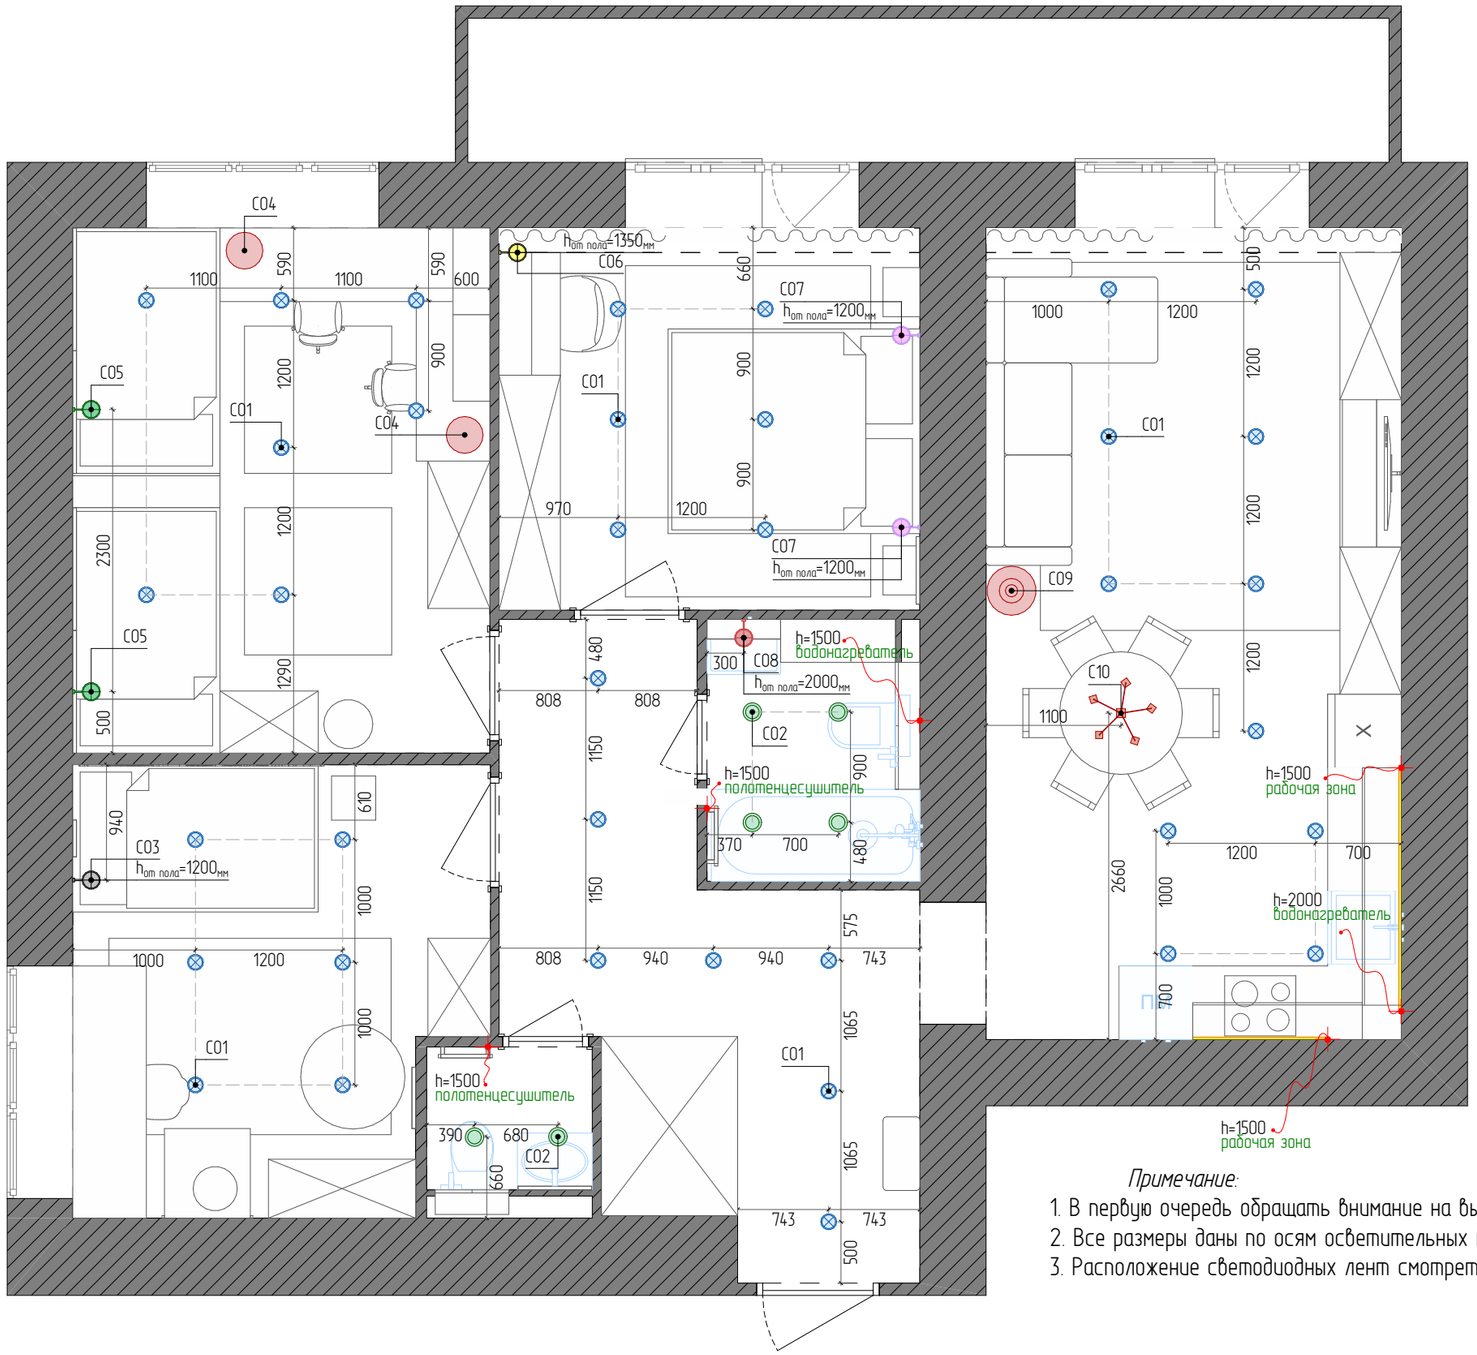

Условное обозначение светильников				
ID	Изображение	Тип светильника	Расположение	Кол-во
С01		светильник потолочный	коридор, детская девочки	37
С02		светильник точечный встраиваемый	санузел	6
С03		бра настенный	детская мальчики	1
С04		лампа настольная	детская девочки	2
С05		настенный светильник	детская девочки	2
С06		светильник линейный	спальня	1
С07		бра	спальня	2
С08		подсветка ванной	ванная	1
С09		напольный светильник	кухня-гостиная	1
С10		люстра	кухня-гостиная	1

LED лента			
ID	Условное обозначение	Наименование	Длина, мм
С01		подсветка рабочей зоны	3084

Примечание:

1. В первую очередь обращать внимание на выносные надписи.
2. Все размеры даны по осям осветительных приборов.
3. Расположение светодиодных лент смотреть в развертках.


Дизайнер	Екатерина Шинкевич	Дизайн-проект квартиры по адресу:	План размещения осветительных приборов, привязка выпусков освещения	Стадия	Лист	Листов
				РП	08	26
Телефон	+7 (931) 271-59-56	адрес	Масштаб 1:50	SHEM		

План выключателей с указанием включения групп светильников



Условное обозначение светильников				
ID	Изображение	Тип светильника	Расположение	Кол-во
C01		светильник потолочный	коридор, детская девочки	37
C02		светильник точечный встраиваемый	санузел	6
C03		бра настенный	детская мальчики	1
C04		лампа настольная	детская девочки	2
C05		настенный светильник	детская девочки	2
C06		светильник линейный	спальня	1
C07		бра	спальня	2
C08		подсветка ванной	ванная	1
C09		напольный светильник	кухня-гостиная	1
C10		люстра	кухня-гостиная	1


Выключатели		
Условное обозначение	Наименование	Кол-во, шт
	Выключатель двухклавишный	2
	Выключатель одноклавишный	8
	Выключатель одноклавишный перекрестный	10
	Выключатель одноклавишный проходной	2

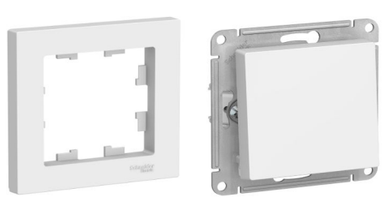

электрика SCHNEIDER ELECTRIC
серия ATLAS DESIGN
цвет БЕЛЫЙ

Дизайнер	Екатерина Шинкевич	Дизайн-проект квартиры по адресу:	План выключателей с указанием включения групп светильников	Стадия	Лист	Листов
				РП	09	26
Телефон	+7 (931) 271-59-56	адрес	Масштаб 1:50	SHEM		

План размещения электрических розеток с привязкой размеров

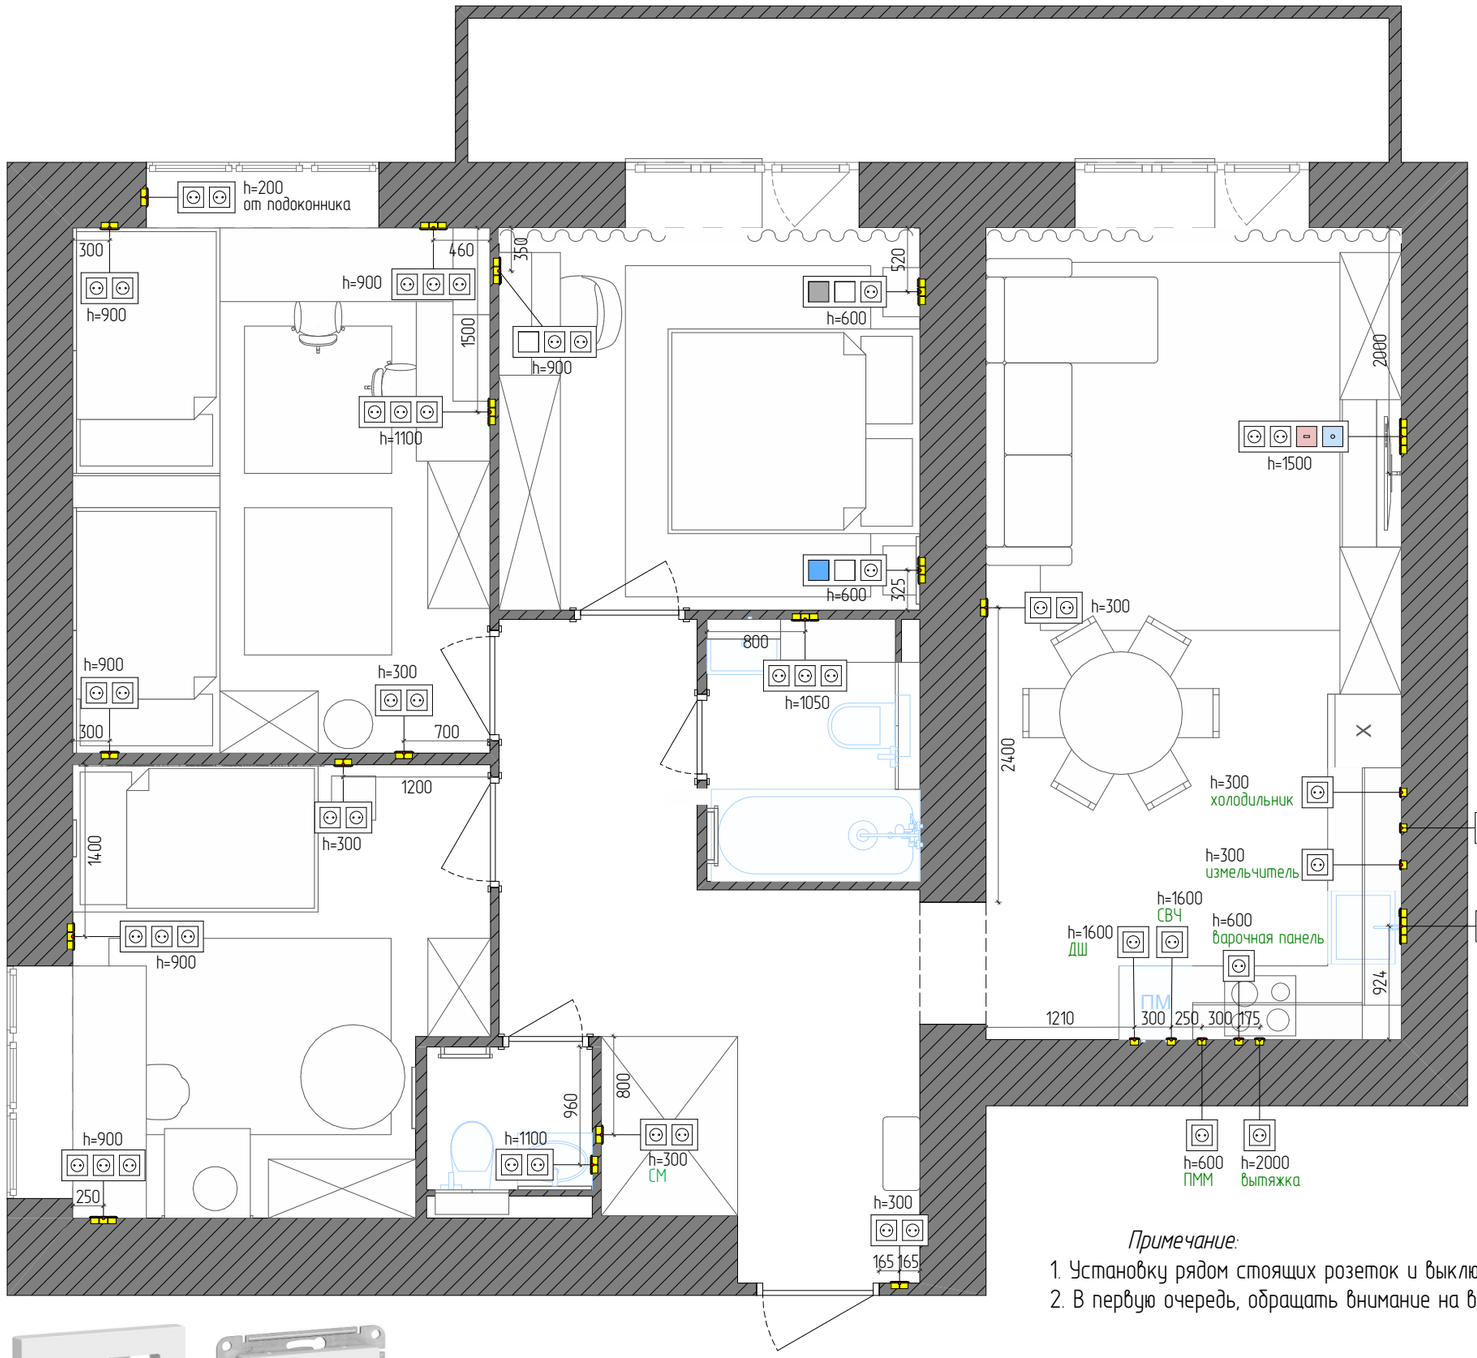


Условное обозначение	Наименование	Кол-во, шт
	Интернет-розетка	1
	Розетка бытовая	50
	Розетка телевизионная	1

Рамки (общее количество)		
Тип рамки (блока)	Рамка ориентация	Кол-во
Рамка x1	Горизонтальная	14
Рамка x2	Горизонтальная	11
Рамка x3	Горизонтальная	9
Рамка x4	Горизонтальная	3

Примечание:


1. Установку рядом стоящих розеток и выключателей произвести под общую рамку.
2. В первую очередь, обращать внимание на выносные надписи.

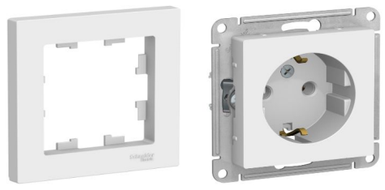

электрика SCHNEIDER ELECTRIC
серия ATLAS DESIGN
цвет БЕЛЫЙ

Дизайнер	Екатерина Шинкевич	Дизайн-проект квартиры по адресу:	План размещения электрических розеток с привязкой размеров	Стадия	Лист	Листов
				РП	10	26
Телефон	+7 (931) 271-59-56	адрес	Масштаб 1:50, 1:1	SHEM		

План полов с указанием типа напольных покрытий

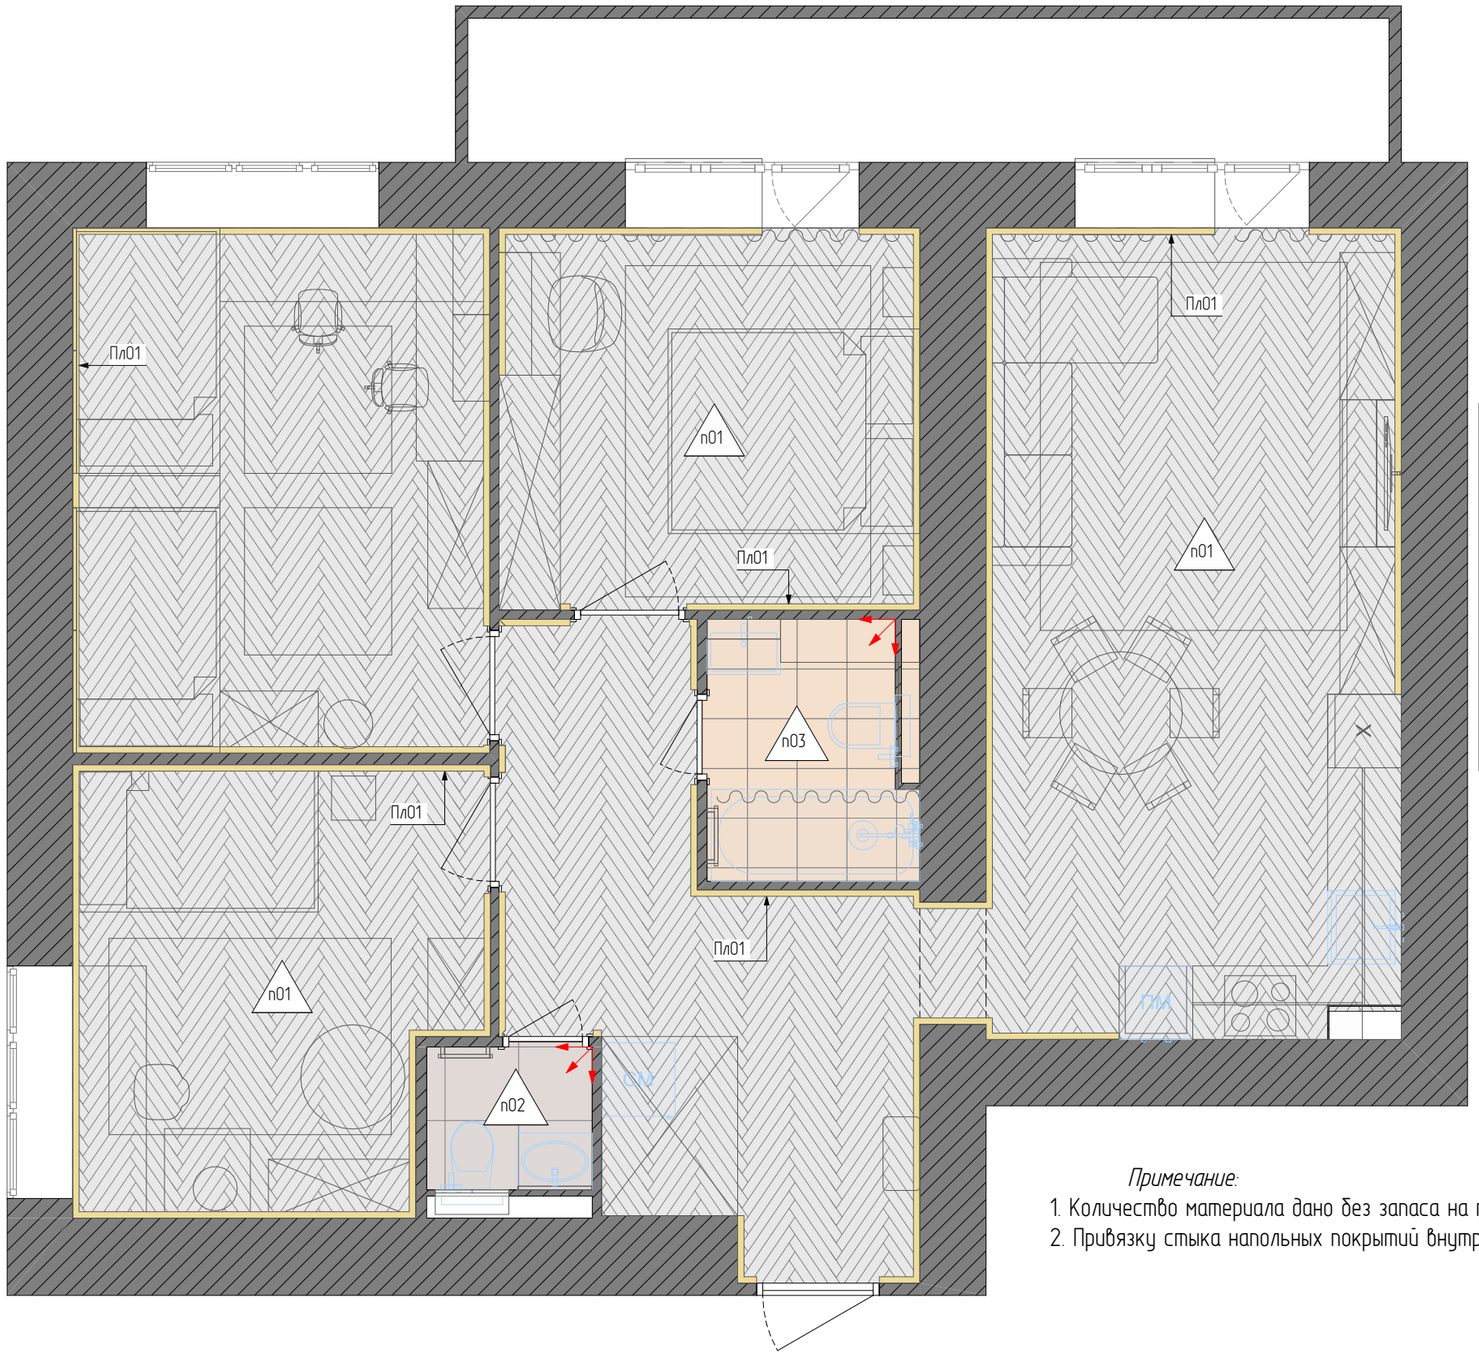

Условные обозначения:

- направление укладки плитки

02 - обозначение типа пола

Напольные покрытия				
ID	Условное обозначение	Наименование	Площадь, кв.м (без запаса)	Изображение
п01		Каменный ламинат SPC BETTA CHALET A808 МОРЗИН	72,24	
п02		Глазурованный керамогранит Ceramente Stellare Cement Pro 60х60см матовый цвет светло-серый	1,60	
п03		Глазурованный керамогранит Estima Jam JA01 40.5х40.5см неполированный цвет бежевый/зеленый с принтом	3,72	

Спецификация плинтуса					
ID	Условное обозначение	Наименование	Производитель	Длина, мм	Примечание
ПлО1		Плинтус	Quadro	59221	h = 80мм

Примечание:

1. Количество материала дано без запаса на подрезку.
2. Привязку стыка напольных покрытий внутри дверных проемов уточнить у поставщика дверей.

Дизайнер	Екатерина Шинкевич	Дизайн-проект квартиры по адресу:	План полов с указанием типа напольных покрытий	Стадия	Лист	Листов
				РП	11	26
Телефон	+7 (931) 271-59-56	адрес	Масштаб 1:50	SHEM		

План потолков с указанием типа используемых материалов



Условные обозначения:

02 – обозначение типа потолка

+2 620 – отметка высоты относительно чистового пола


Ведомость потолков			
ID	Условное обозначение	Наименование	Площадь, кв.м (без запаса)
01		Натяжной потолок	75,05
02		штукатурка + покраска	1,37

Примечание:

1. За отметку 0,000 принята высота чистового пола.
2. Подвесной потолок опустить на 70$_{мм}$, от самой нижней точки чернового потолка в конкретном помещении.
3. Отметки высот указаны от чистового пола.
4. На развертках все высоты даны от чистового пола.

Дизайнер	Екатерина Шинкевич	Дизайн-проект квартиры по адресу:	План потолков с указанием типа используемых материалов	Стадия	Лист	Листов
				РП	12	26
Телефон	+7 (931) 271-59-56	адрес	Масштаб 1:50	SHEM		

План расположения систем отопления и вентиляции

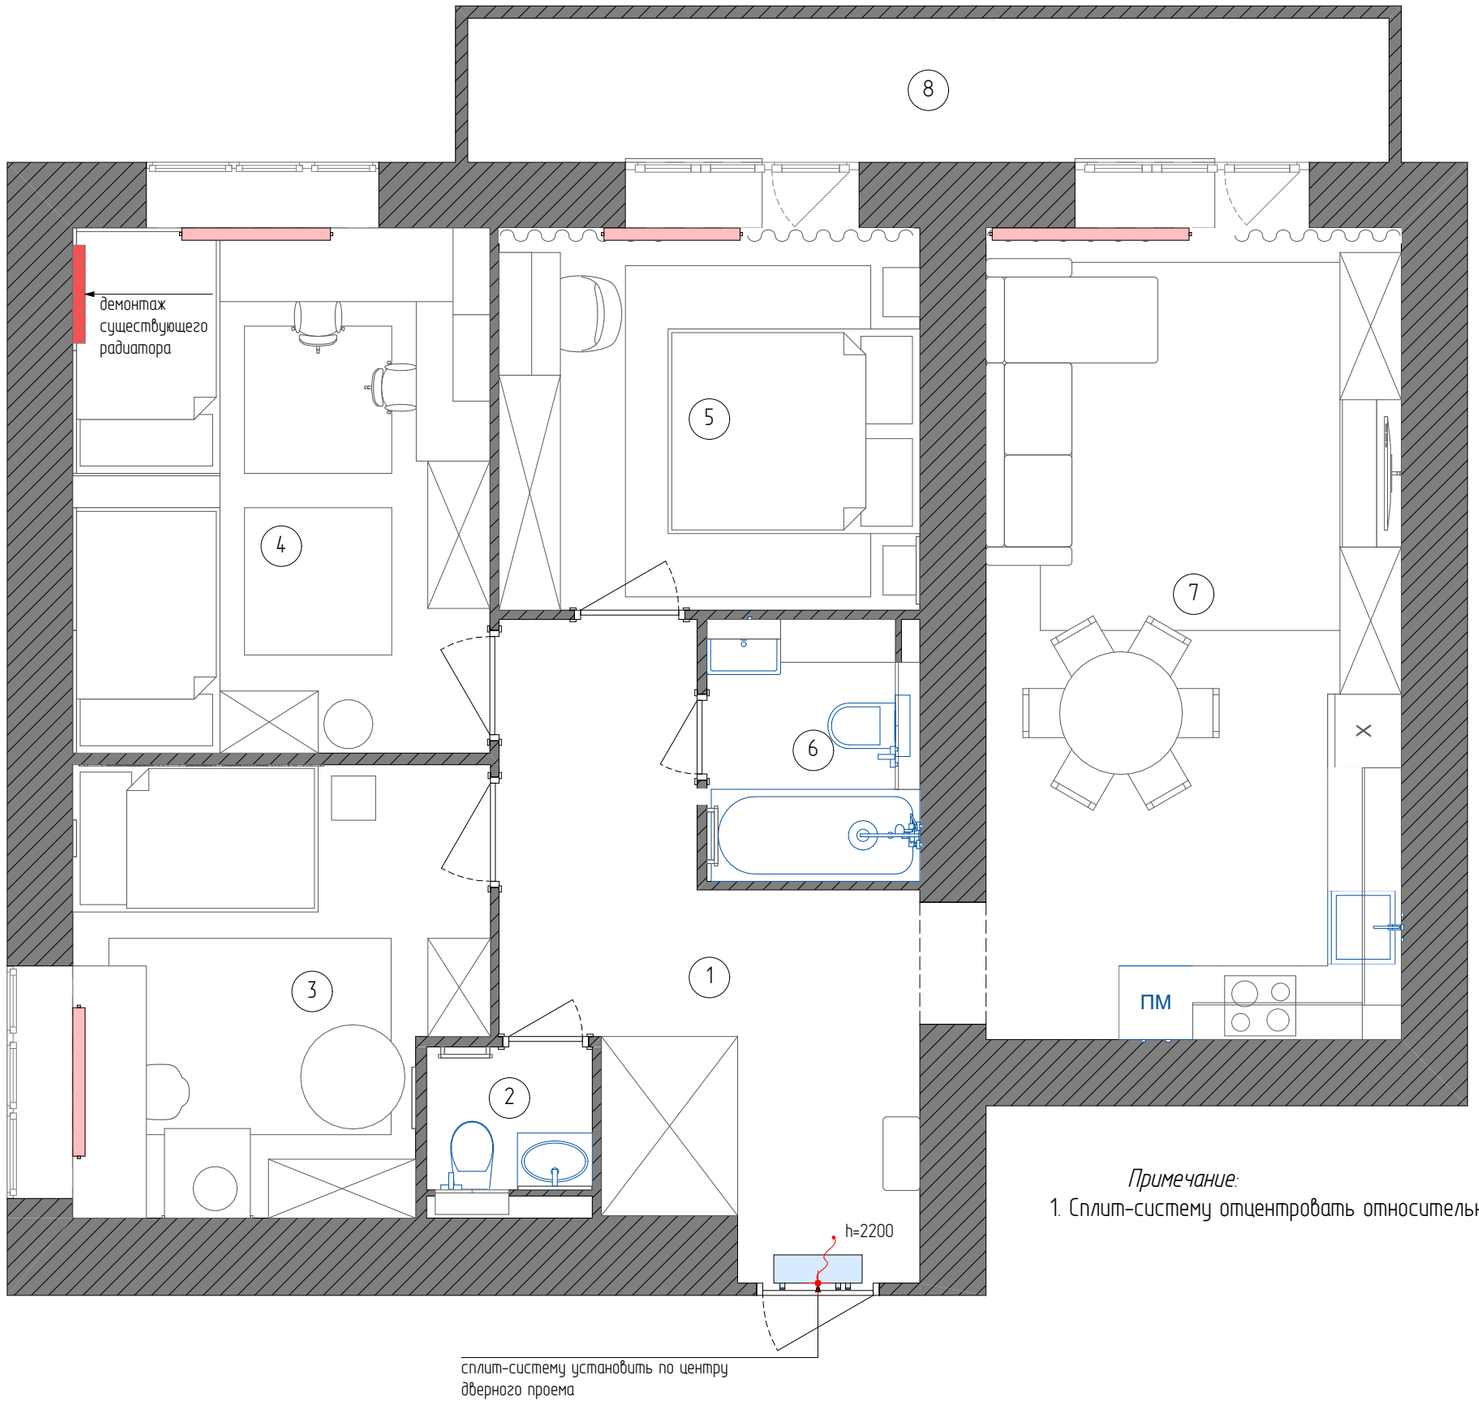

Экспликация помещений		
№	Название помещения	Площадь, кв.м
1	Коридор	12,27
2	Санузел	1,88
3	Детская мальчики	11,68
4	Детская девочки	14,55
5	Спальня	10,69
6	Ванная	3,70
7	Кухня-гостиная	22,25
8	Лоджия	8,82
		85,84 м²

Условные обозначения:

– радиаторы отопления


– сплит-система

Примечание:

1. Сплит-систему отцентровать относительно дверного проема.

Дизайнер	Екатерина Шинкевич	Дизайн-проект квартиры по адресу:	План расположения систем отопления и вентиляции	Стадия	Лист	Листов
				РП	13	26
Телефон	+7 (931) 271-59-56	адрес	Масштаб 1:50	SHEM		

План размещения санитарно-технического оборудования

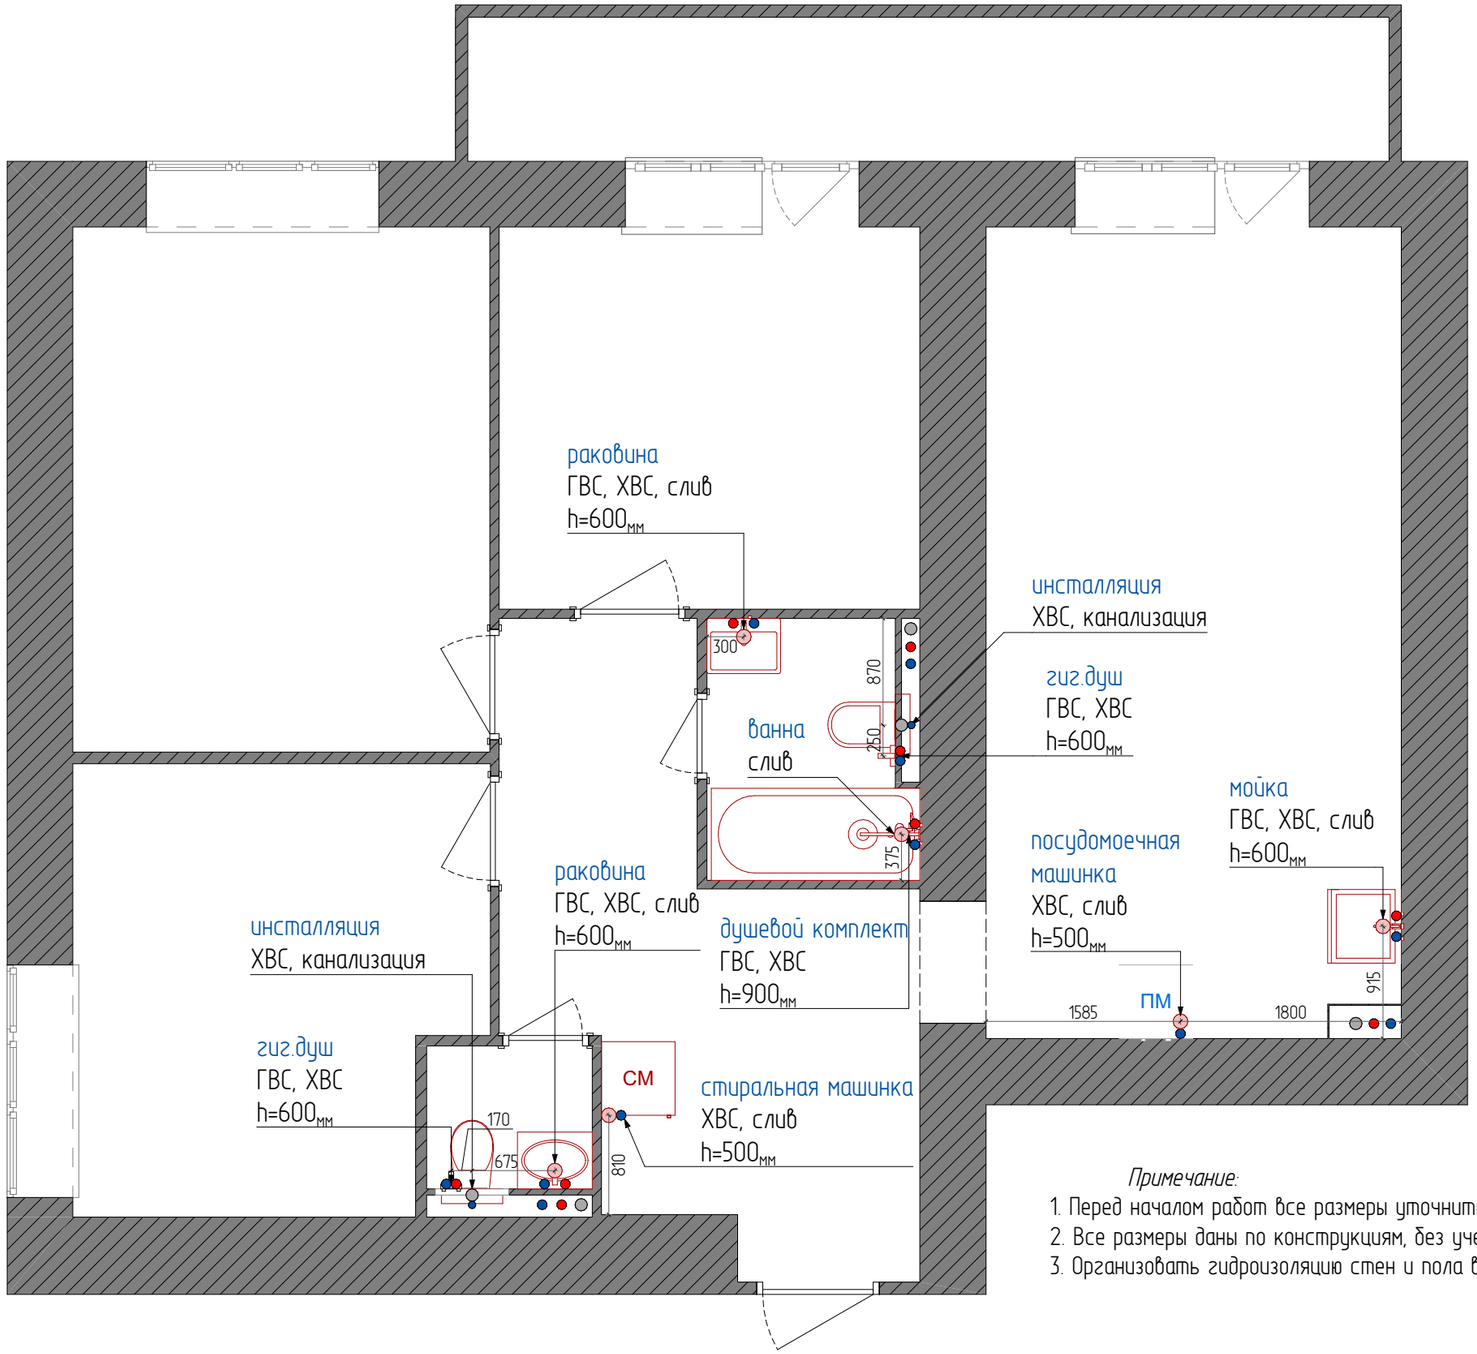

Условные обозначения:

- канализационная труба
- труба подачи горячего водоснабжения
- труба подачи холодного водоснабжения
- размещение стока раковин и сливов

Примечание:

1. Перед началом работ все размеры уточнить по месту.
2. Все размеры даны по конструкциям, без учета плитки и клея.
3. Организовать гидроизоляцию стен и пола в ванной и санузле.

Дизайнер	Екатерина Шинкевич	Дизайн-проект квартиры по адресу:	План размещения санитарно-технического оборудования	Стадия	Лист	Листов
				РП	14	26
Телефон	+7 (931) 271-59-56	адрес	Масштаб 1:50	SHEM		


План отделочных материалов по стенам





Условное обозначение	Наименование	Помещение
	Плитка настенная Kerama Marazzi Монпарнас	ванная
	Краска Tikkurila для влаж. помещений	ванная, санузел
	Обои акцентные	детская девочки
	Обои база	детская девочки
	Обои база	детская мальчики
	Обои акцентные	детская мальчики
	Глазурованный керамогранит Ceradim Calacatta Goddes 120х60 см	кухня-гостиная
	Обои	кухня-гостиная, прихожая, спальня
	Декоративные рейки	прихожая
	Плитка настенная Azori Forest	санузел


Дизайнер	Екатерина Шинкевич	Дизайн-проект квартиры по адресу:	План отделочных материалов по стенам	Стадия	Лист	Листов
				РП	15	26
Телефон	+7 (931) 271-59-56	адрес	Масштаб 1:50	SHEM		


Развертки по стенам. Прихожая

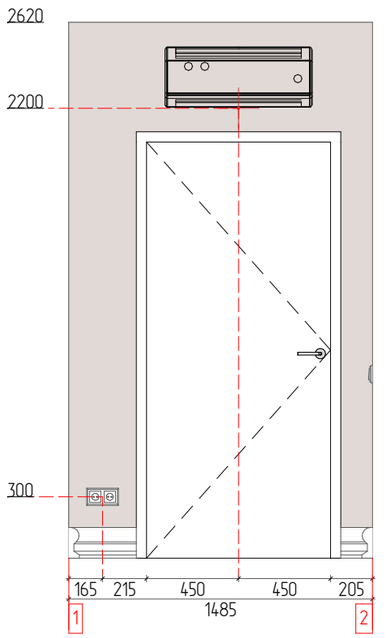


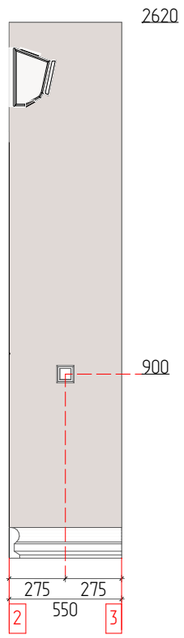


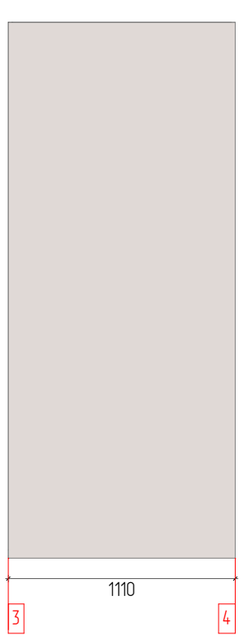


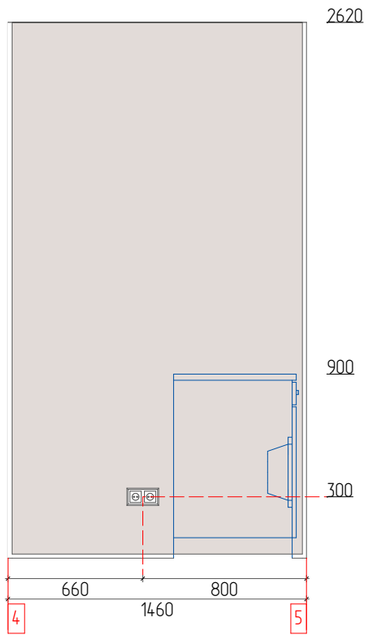

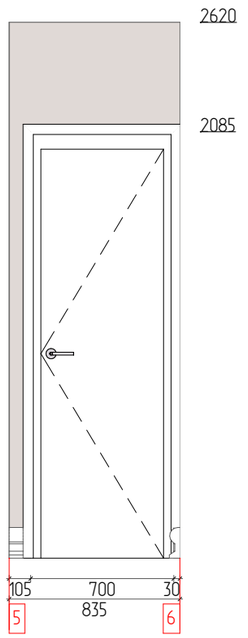

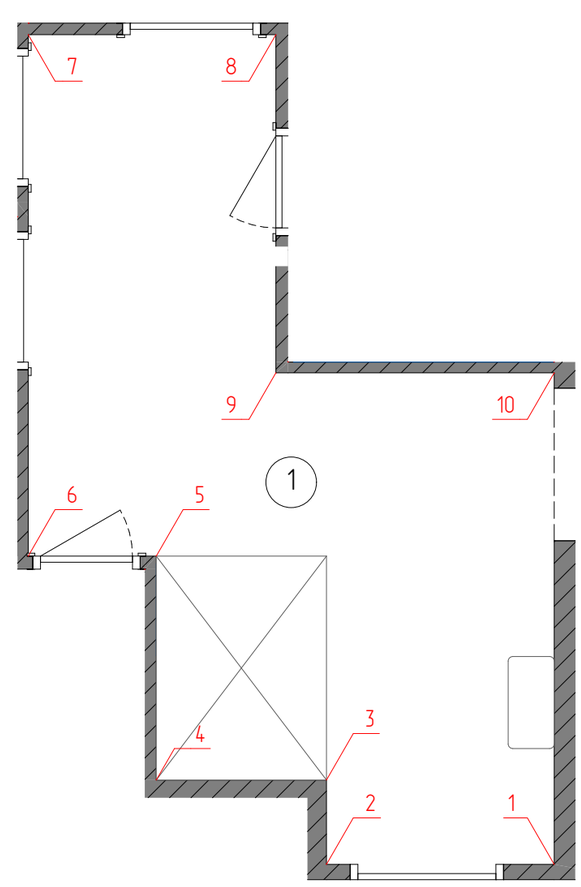

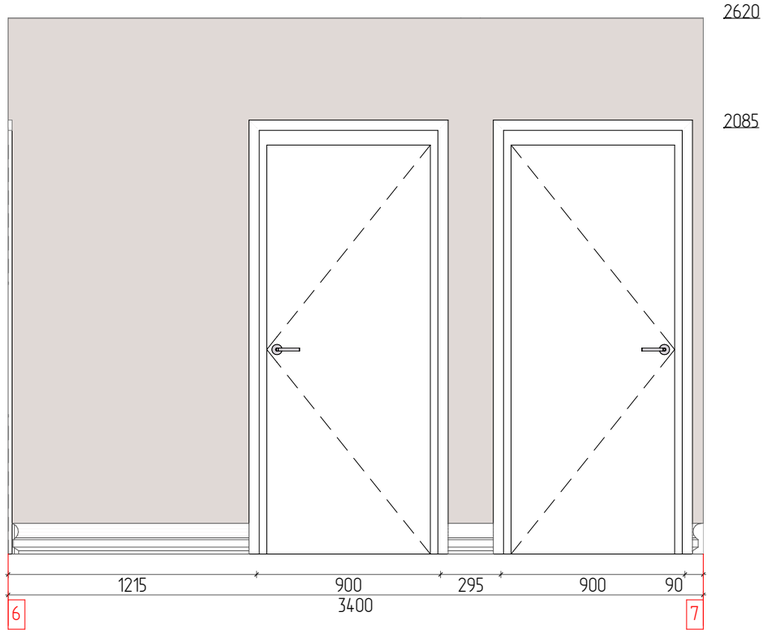

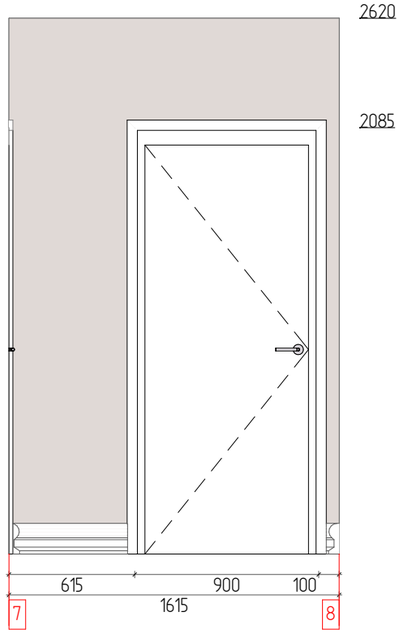


Расход материалов. Прихожая			
Наименование	Условное обозначение	Площадь, кв.м (без запаса)	Примечание
Обои серо-бежевые		33,86	


Примечание:


1. Количество материала для отделки стен дано без запаса.
2. Пересчитать все материалы перед заказом с менеджером бренда (используя данные проекта).
3. Размеры и описание изделий по индивидуальным заказам смотреть на соответствующих листах проекта.


Дизайнер	Екатерина Шинкевич	Дизайн-проект квартиры по адресу:	Развертки по стенам. Прихожая	Стадия	Лист	Листов
				РП	16	26
Телефон	+7 (931) 271-59-56	адрес	Масштаб 1:40, 1:30	SHEM		


Развертки по стенам. Прихожая

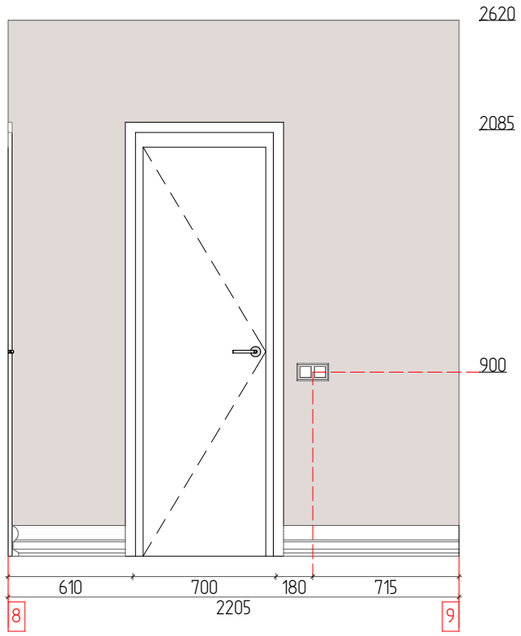

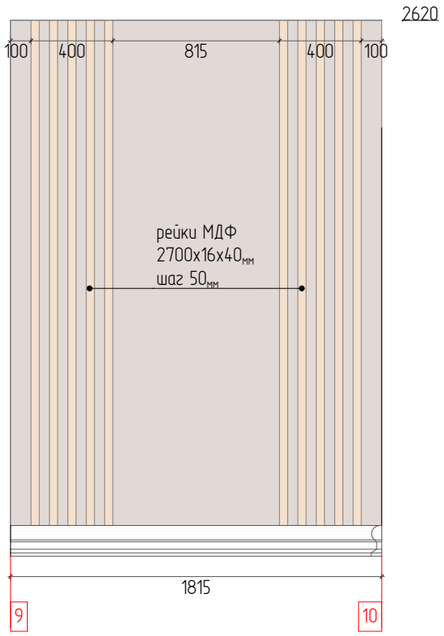

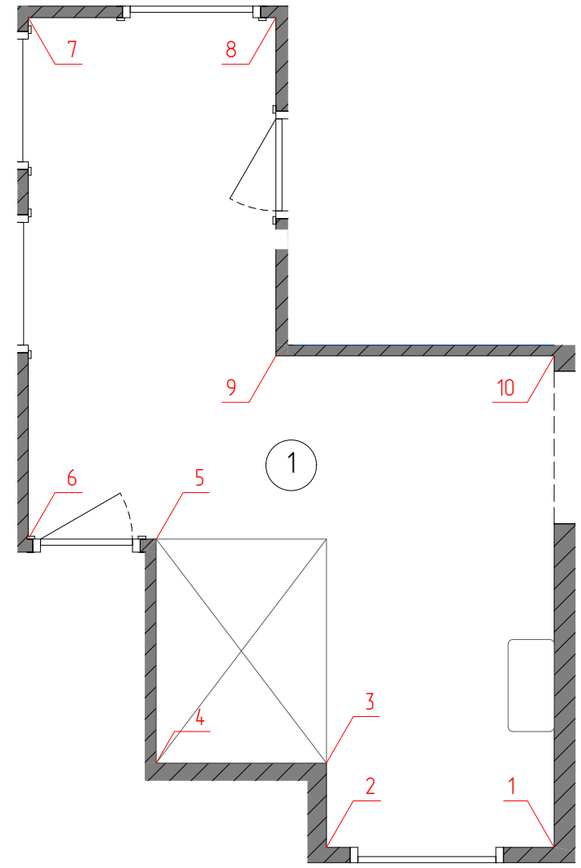

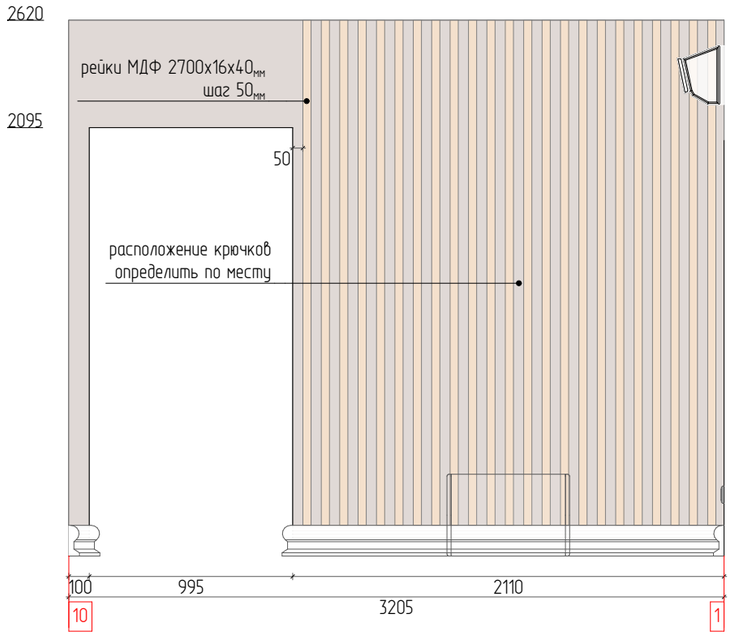

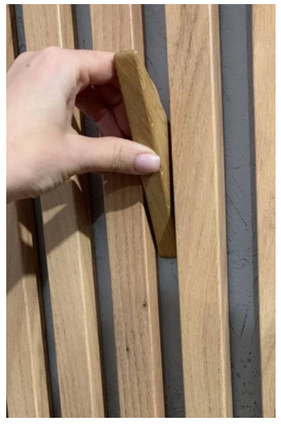

Крючки настенные


Примечание:


1. Количество материала для отделки стен дано без запаса.
2. Пересчитать все материалы перед заказом с менеджером бренда (используя данные проекта).
3. Размеры и описание изделий по индивидуальным заказам смотреть на соответствующих листах проекта.


Расход материалов. Прихожая			
Наименование	Условное обозначение	Площадь, кв.м (без запаса)	Примечание
Обои серо-бежевые		33,86	


Дизайнер	Екатерина Шинкевич	Дизайн-проект квартиры по адресу:	Развертки по стенам. Прихожая	Стадия	Лист	Листов
				РП	17	26
Телефон	+7 (931) 271-59-56	адрес	Масштаб 1:40, 1:30	SHEM		


Развертки по стенам. Санузел

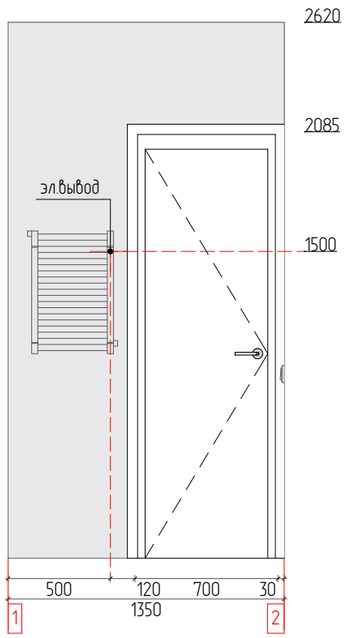

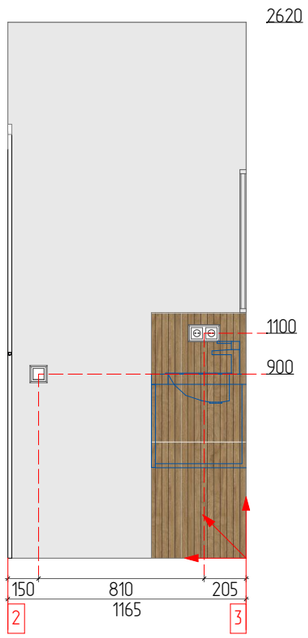

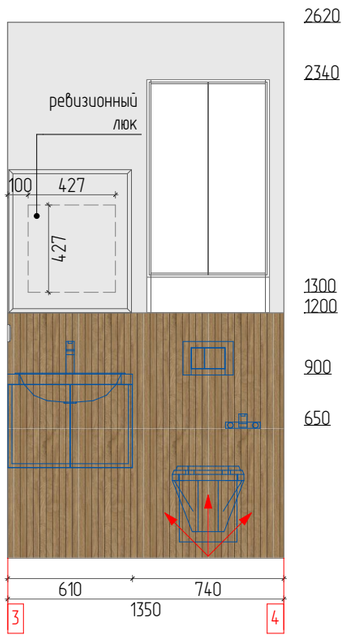

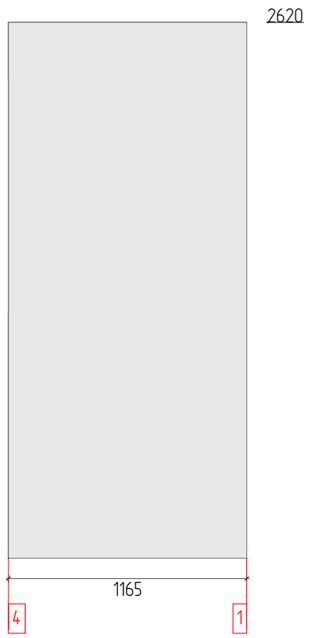

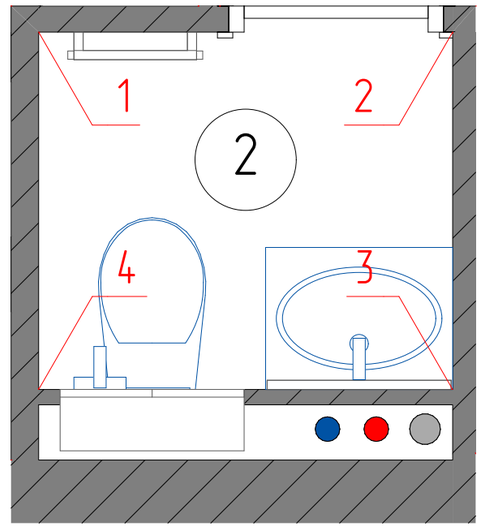


Расход материалов. Санузел			
Наименование	Условное обозначение	Площадь, кв.м (без запаса)	Примечание
Краска Tikkurila		8,86	TVT F 456, TVT F 457, TVT Y 456, TVT F 395, TVT F 396
Плитка настенная Azori Forest		2,18	матовая цвет коричневое дерево 31.5х63 см


Примечание:


1. Количество материала для отделки стен дано без запаса.
2. Пересчитать все материалы перед заказом с менеджером бренда (используя данные проекта).
3. Размеры и описание изделий по индивидуальным заказам смотреть на соответствующих листах проекта.


Дизайнер	Екатерина Шинкевич	Дизайн-проект квартиры по адресу:	Развертки по стенам. Санузел	Стадия	Лист	Листов
				РП	18	26
Телефон	+7 (931) 271-59-56	адрес	Масштаб 1:20, 1:30, 1:1	SHEM		


Развертки по стенам. Детская мальчики

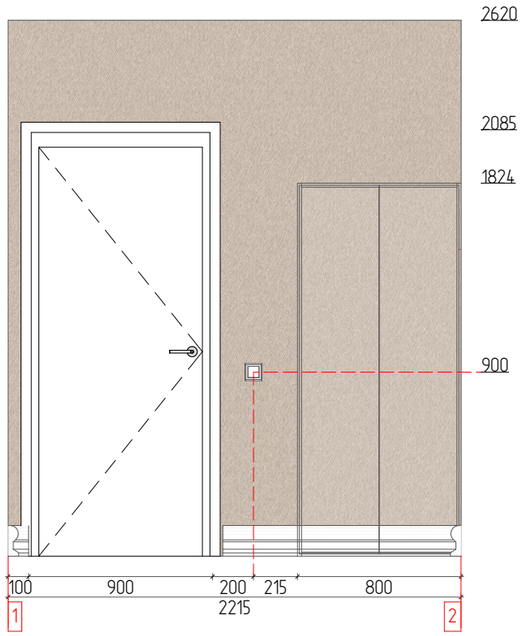


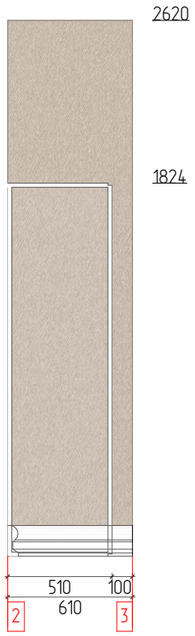


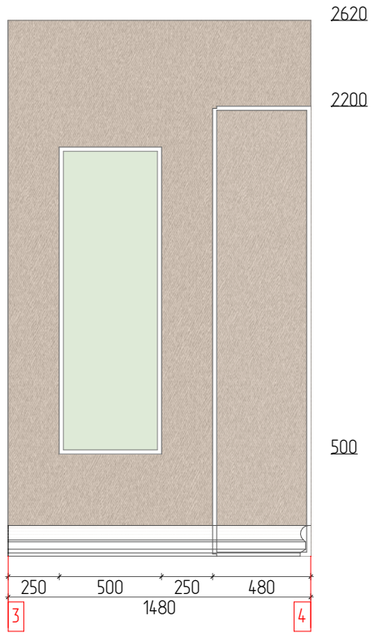

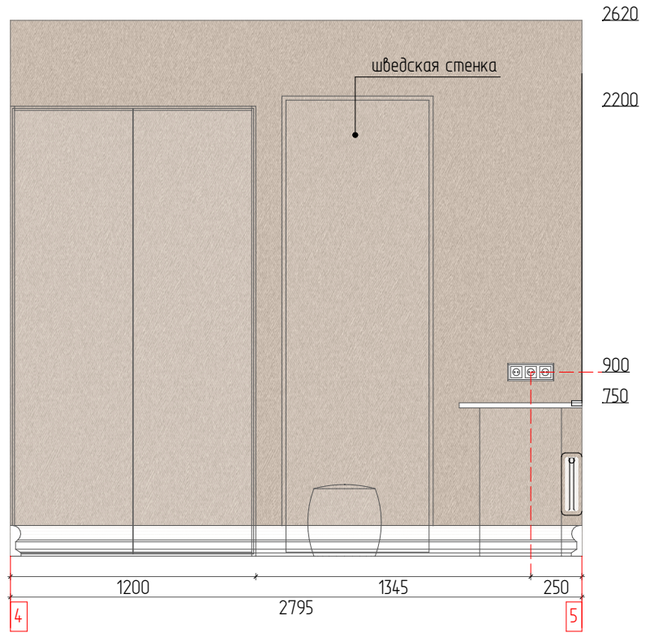

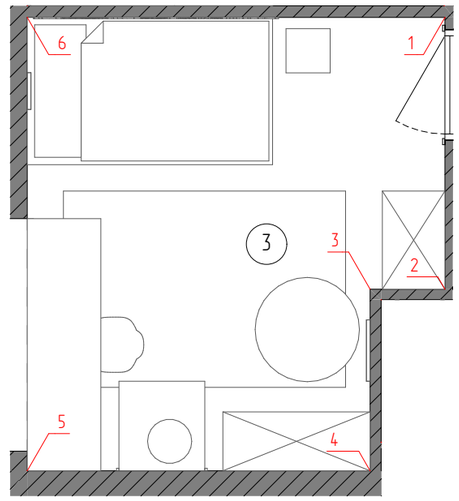

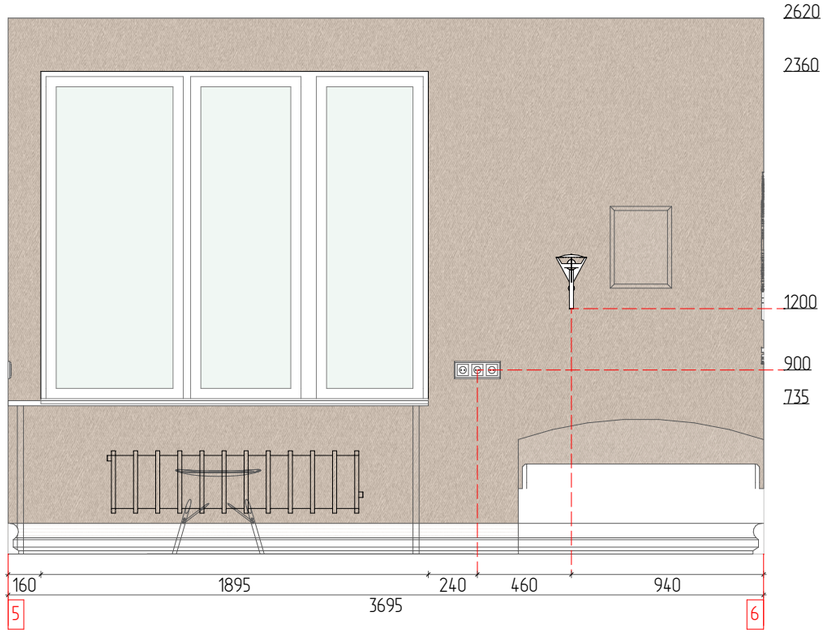

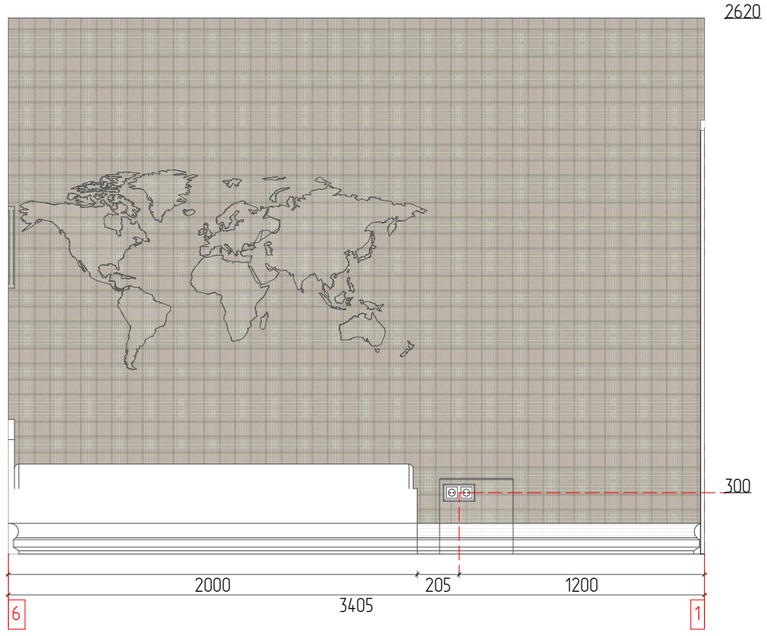


Расход материалов. Детская мальчики			
Наименование	Условное обозначение	Площадь, кв.м (без запаса)	Примечание
Обои виниловые		19,45	215233958 (wildberries.ru)
Обои клетка виниловые		8,92	198706209 (wildberries.ru)


Примечание:


1. Количество материала для отделки стен дано без запаса.
2. Пересчитать все материалы перед заказом с менеджером бренда (используя данные проекта).
3. Размеры и описание изделий по индивидуальным заказам смотреть на соответствующих листах проекта.


Дизайнер	Екатерина Шинкевич	Дизайн-проект квартиры по адресу:	Развертки по стенам. Детская мальчики	Стадия	Лист	Листов
				РП	19	26
Телефон	+7 (931) 271-59-56	адрес	Масштаб 1:50, 1:30	SHEM		


Развертки по стенам. Детская девочки

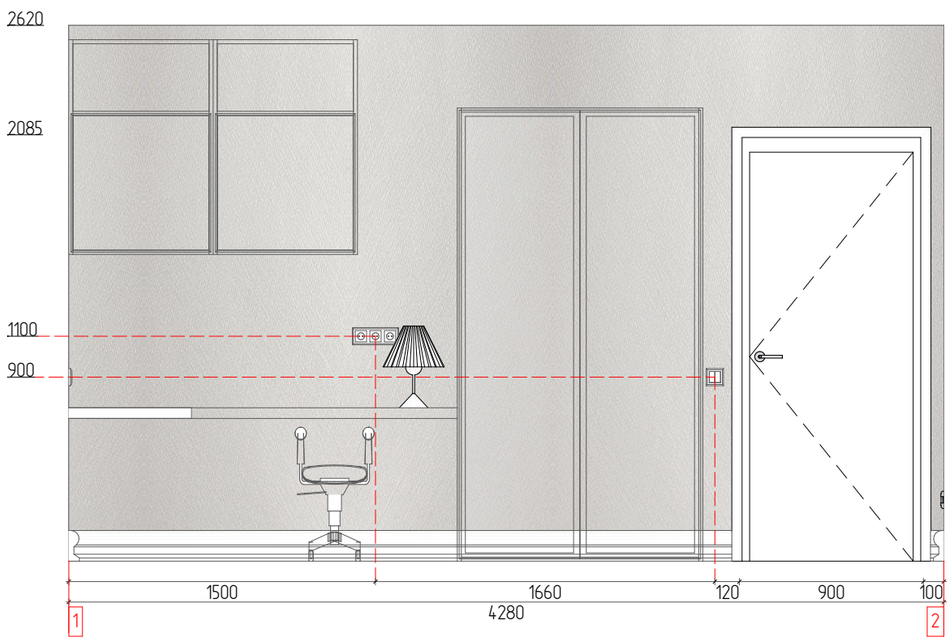

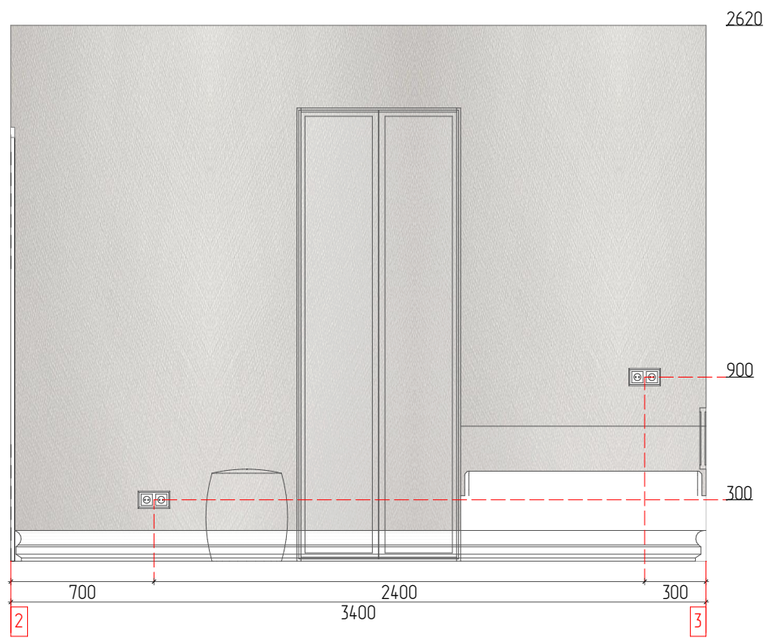

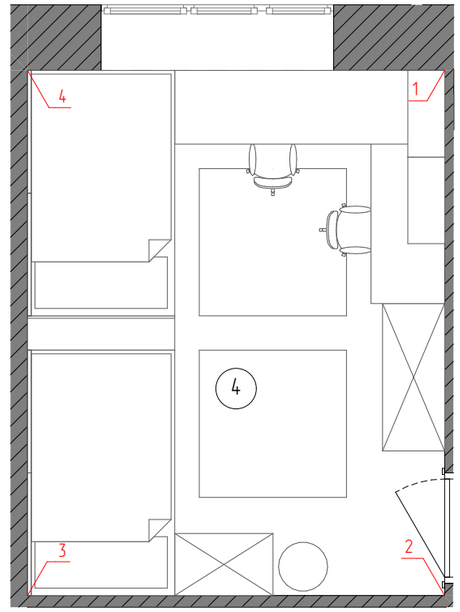

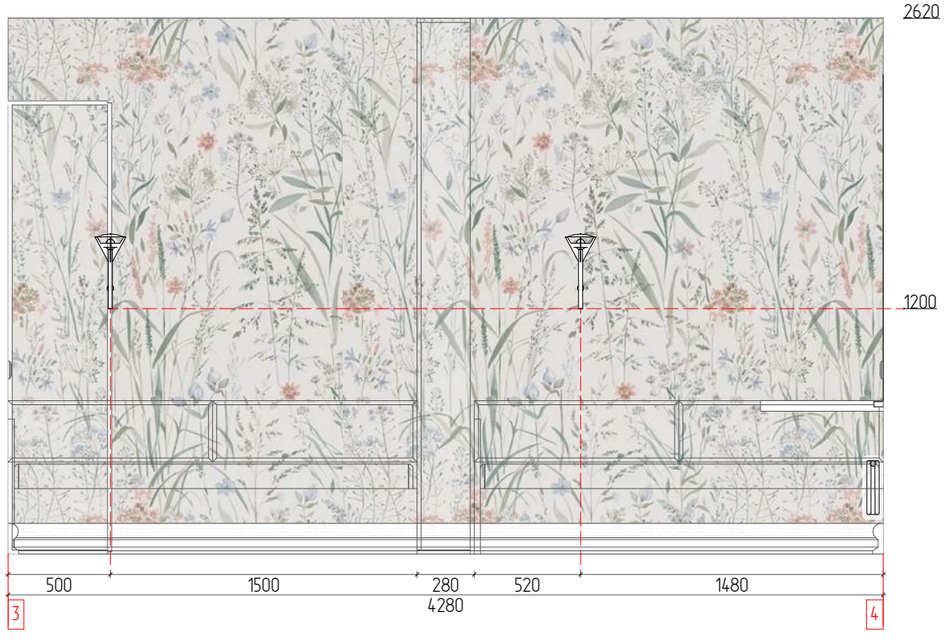

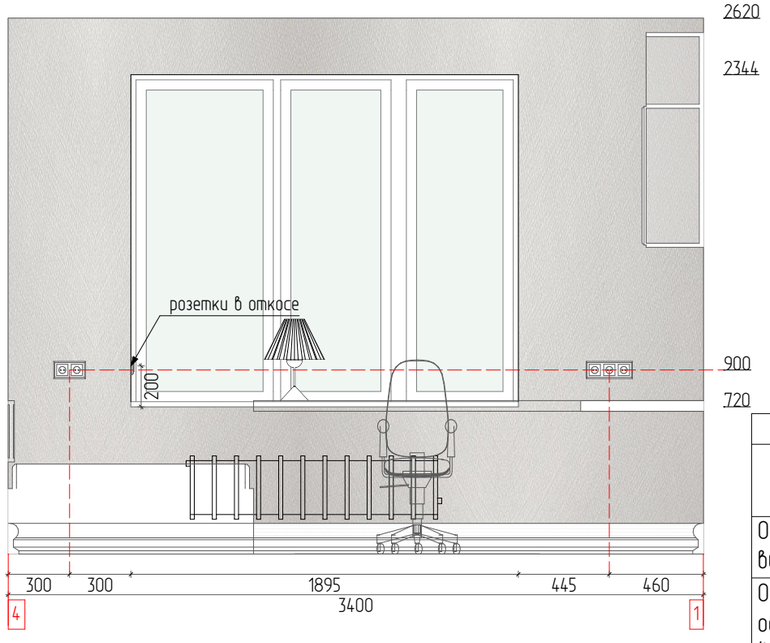

Расход материалов. Детская девочки			
Наименование	Условное обозначение	Площадь, кв.м (без запаса)	Примечание
Обои метровые виниловые		11,21	167532794 (wildberries.ru)
Обои серые однотонные Textile (Moda Interio)		24,08	1410720452 (ozon.ru)


Примечание:


1. Количество материала для отделки стен дано без запаса.
2. Пересчитать все материалы перед заказом с менеджером бренда (используя данные проекта).
3. Размеры и описание изделий по индивидуальным заказам смотреть на соответствующих листах проекта.


Дизайнер	Екатерина Шинкевич	Дизайн-проект квартиры по адресу:	Развертки по стенам. Детская девочки	Стадия	Лист	Листов
Телефон	+7 (931) 271-59-56	адрес	Масштаб 1:55, 1:50, 1:30	РП	20	26


SHEM


Развертки по стенам. Спальня

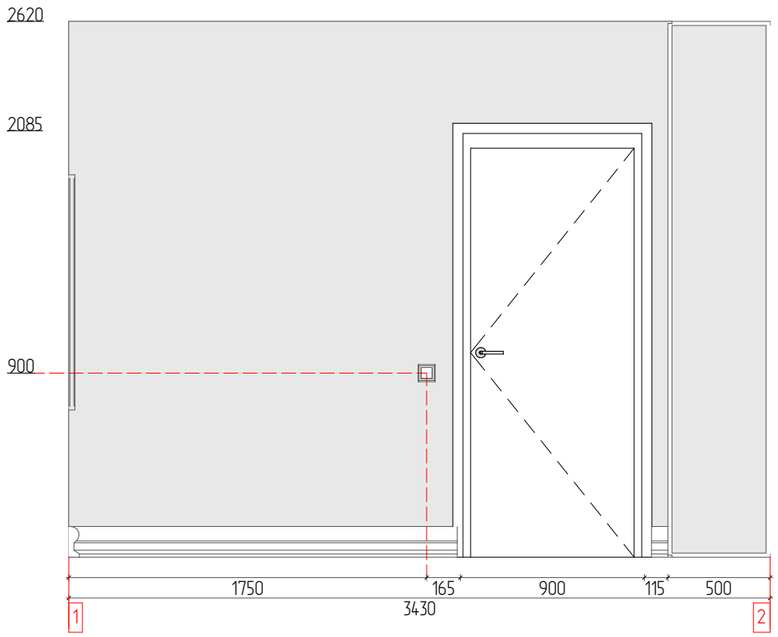

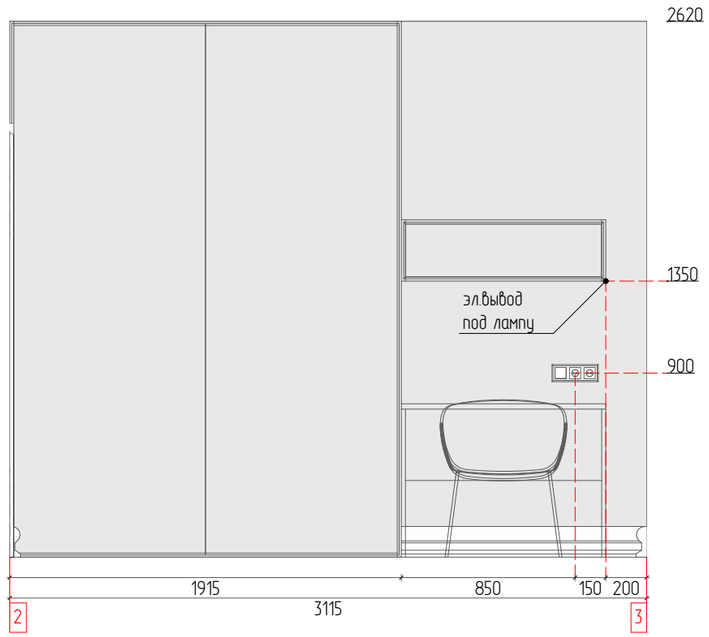

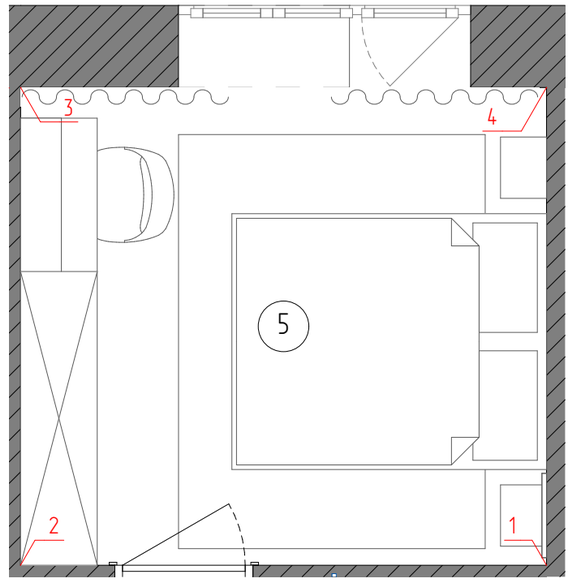

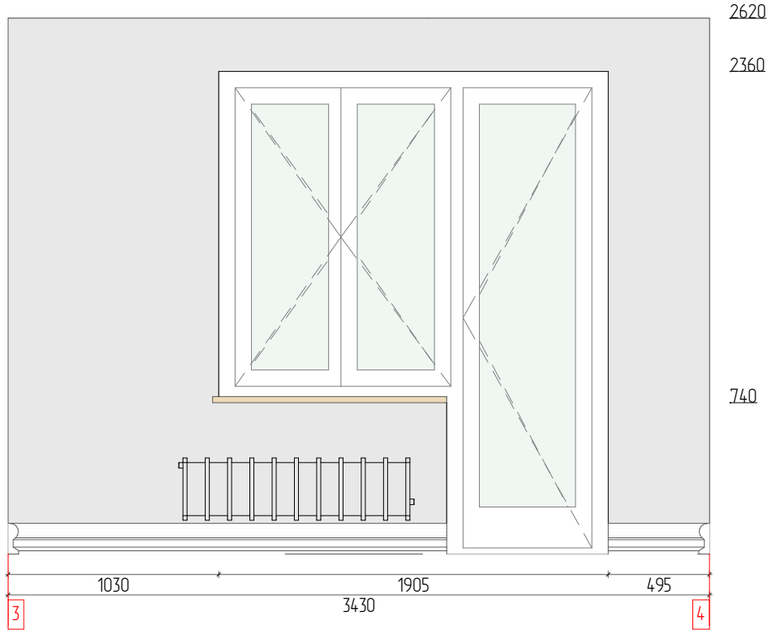

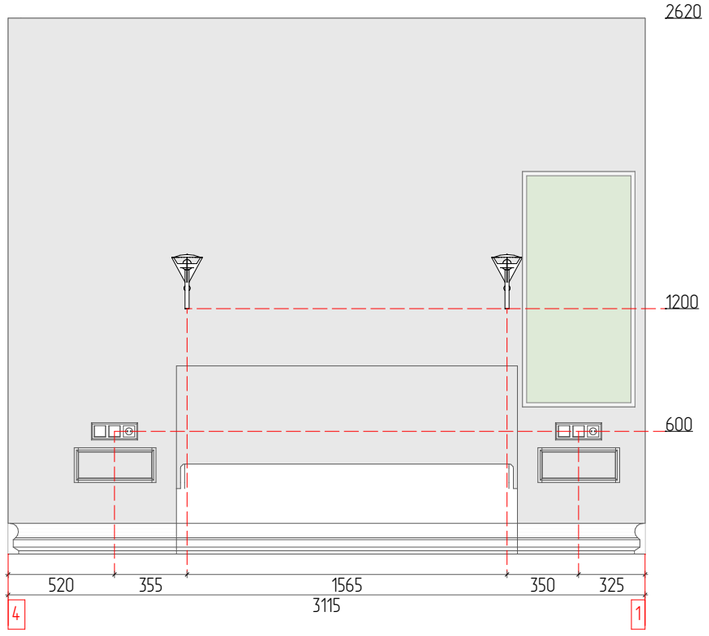


Расход материалов. Спальня			
Наименование	Условное обозначение	Площадь, кв.м (без запаса)	Примечание
Обои под покраску флизелиновые антивандальные Erismann Defender Рогожка белые		28,78	89364431 (lemanapro.ru)
Обои флизелиновые Erismann Anny бежевые		28,78	84774830 (lemanapro.ru)


Примечание:


1. Количество материала для отделки стен дано без запаса.
2. Пересчитать все материалы перед заказом с менеджером бренда (используя данные проекта).
3. Размеры и описание изделий по индивидуальным заказам смотреть на соответствующих листах проекта.
4. Обои даны на выбор, один из таблицы материалов.


Дизайнер	Екатерина Шинкевич	Дизайн-проект квартиры по адресу:	Развертки по стенам. Спальня	Стадия	Лист	Листов
				РП	21	26
Телефон	+7 (931) 271-59-56	адрес	Масштаб 1:55, 1:40, 1:30	SHEM		


Развертки по стенам. Ванная

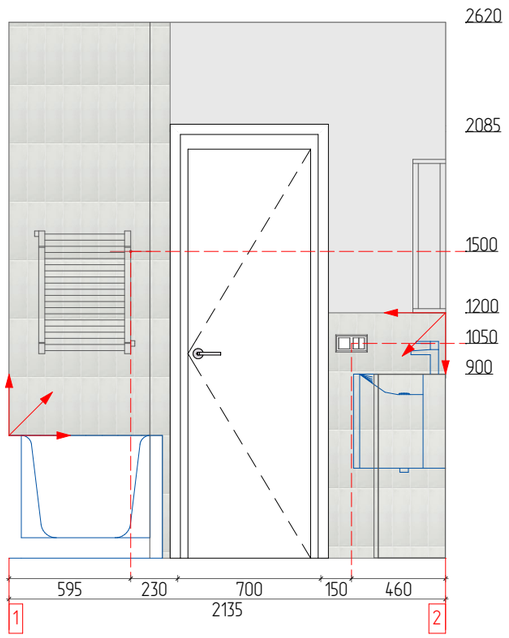


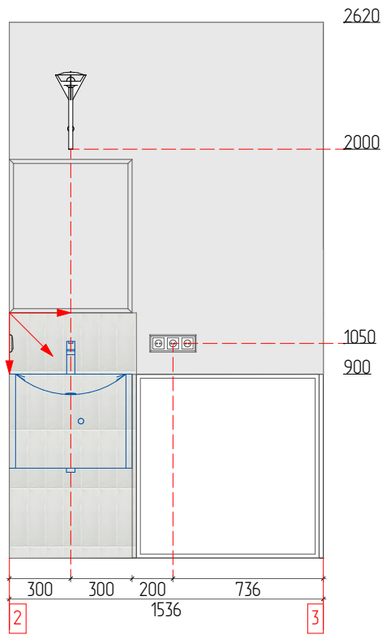


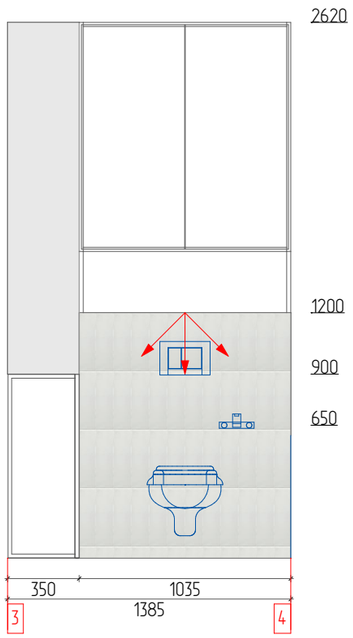

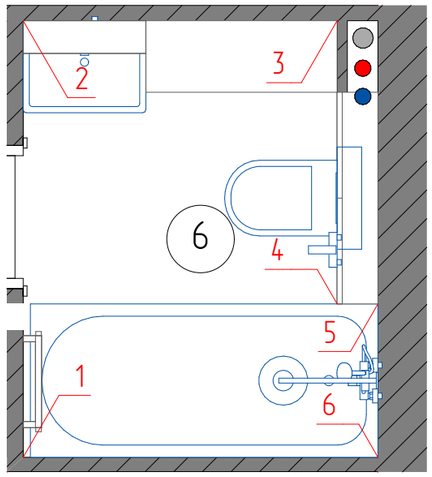

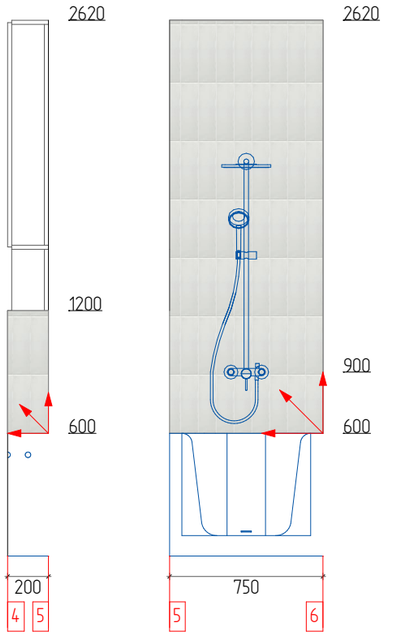

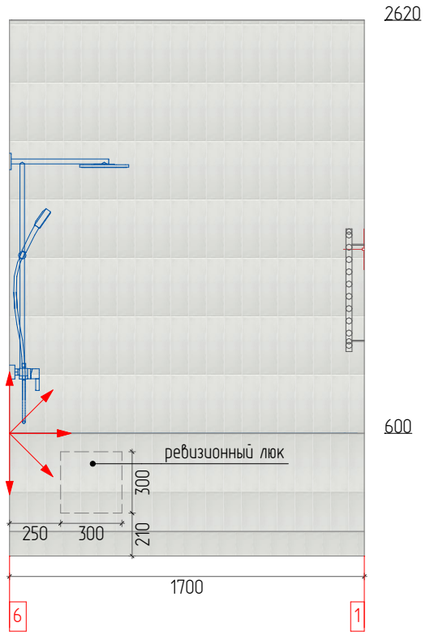

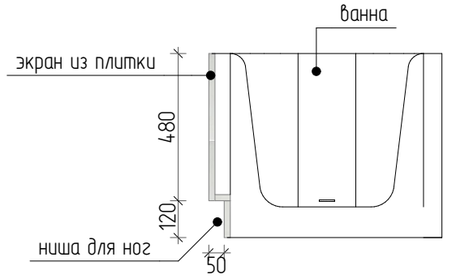

Узел 1
Экран для ванной из плитки
с нишей для ног

Расход материалов. Ванная			
Наименование	Условное обозначение	Площадь, кв.м (без запаса)	Примечание
Краска Tikkurila		4,32	TVT F 456, TVT F 457, TVT Y 456, TVT F 395, TVT F 396
Плитка настенная Kerama Marazzi Монпарнас		10,47	


Примечание:


1. Количество материала для отделки стен дано без запаса.
2. Пересчитать все материалы перед заказом с менеджером бренда (используя данные проекта).
3. Размеры и описание изделий по индивидуальным заказам смотреть на соответствующих листах проекта.


Дизайнер	Екатерина Шинкевич	Дизайн-проект квартиры по адресу:	Развертки по стенам. Ванная	Стадия	Лист	Листов
Телефон	+7 (931) 271-59-56	адрес	Масштаб 1:30, 1:20	РП	22	26

SHEM

Развертки по стенам. Кухня-гостиная

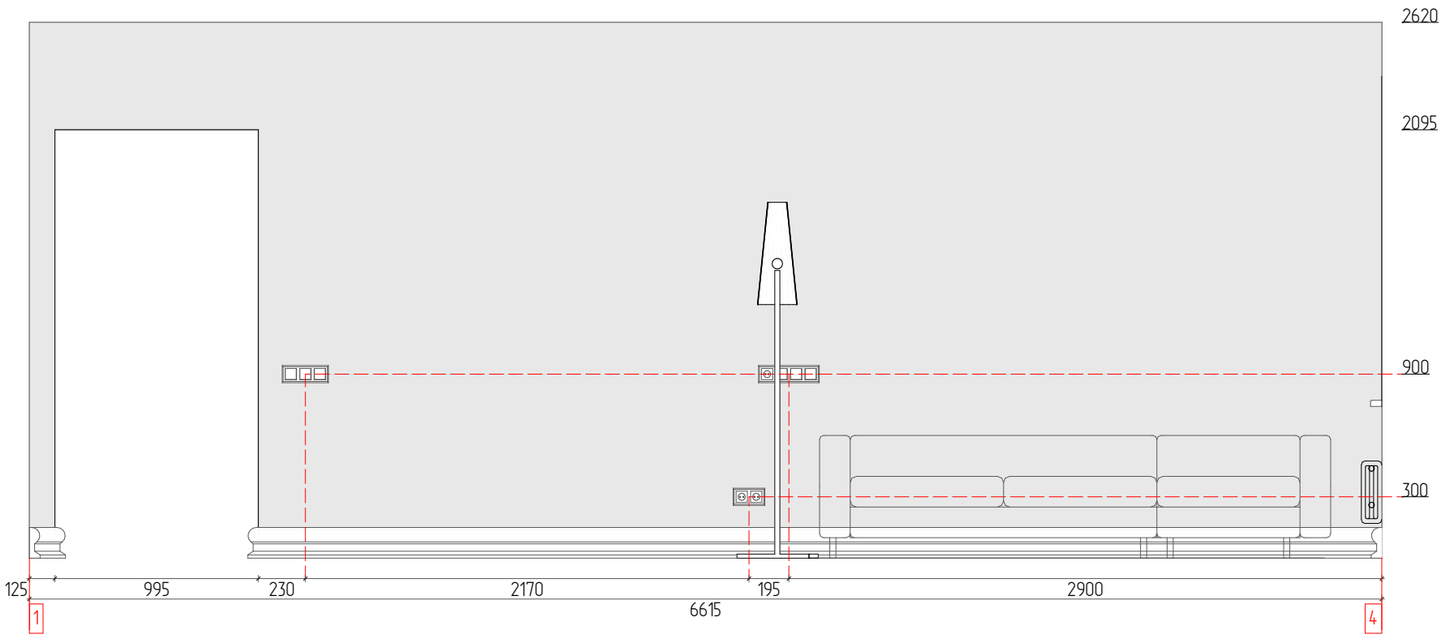

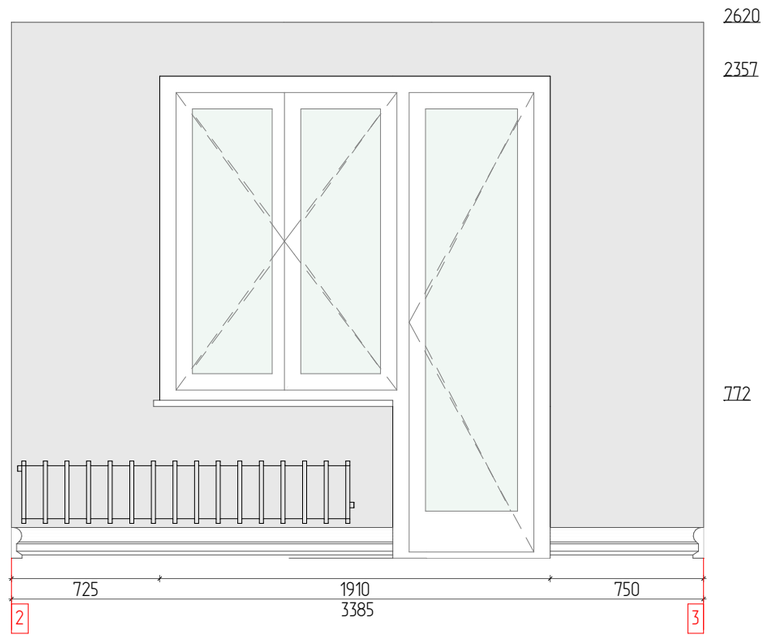

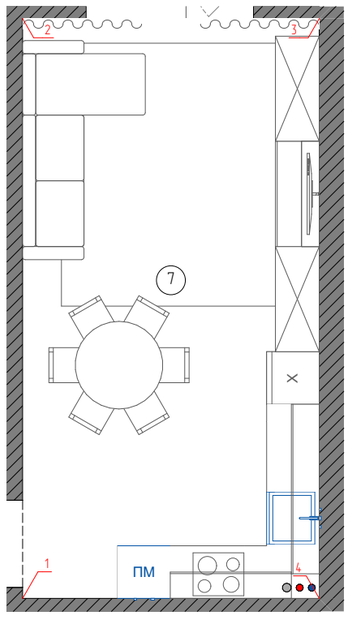


Расход материалов. Кухня-гостиная			
Наименование	Условное обозначение	Площадь, кв.м (без запаса)	Примечание
Глазурованный керамогранит Ceradim Calacatta Goddes 120x60		2,35	89353837 (lemanapro.ru)
Обои под покраску флизелиновые антивандальные Erismann Defender Рогожка белые		44,31	89364431 (lemanapro.ru)
Обои флизелиновые Erismann Anny бежевые		44,31	84774830 (lemanapro.ru)


Примечание:


1. Количество материала для отделки стен дано без запаса.
2. Пересчитать все материалы перед заказом с менеджером бренда (используя данные проекта).
3. Размеры и описание изделий по индивидуальным заказам смотреть на соответствующих листах проекта.
4. Обои даны на выбор, один из таблицы материалов.

Дизайнер	Екатерина Шинкевич	Дизайн-проект квартиры по адресу:	Развертки по стенам. Кухня-гостиная	Стадия	Лист	Листов
				РП	23	26
Телефон	+7 (931) 271-59-56	адрес	Масштаб 1:70, 1:30	SHEM		

Развертки по стенам. Кухня-гостиная

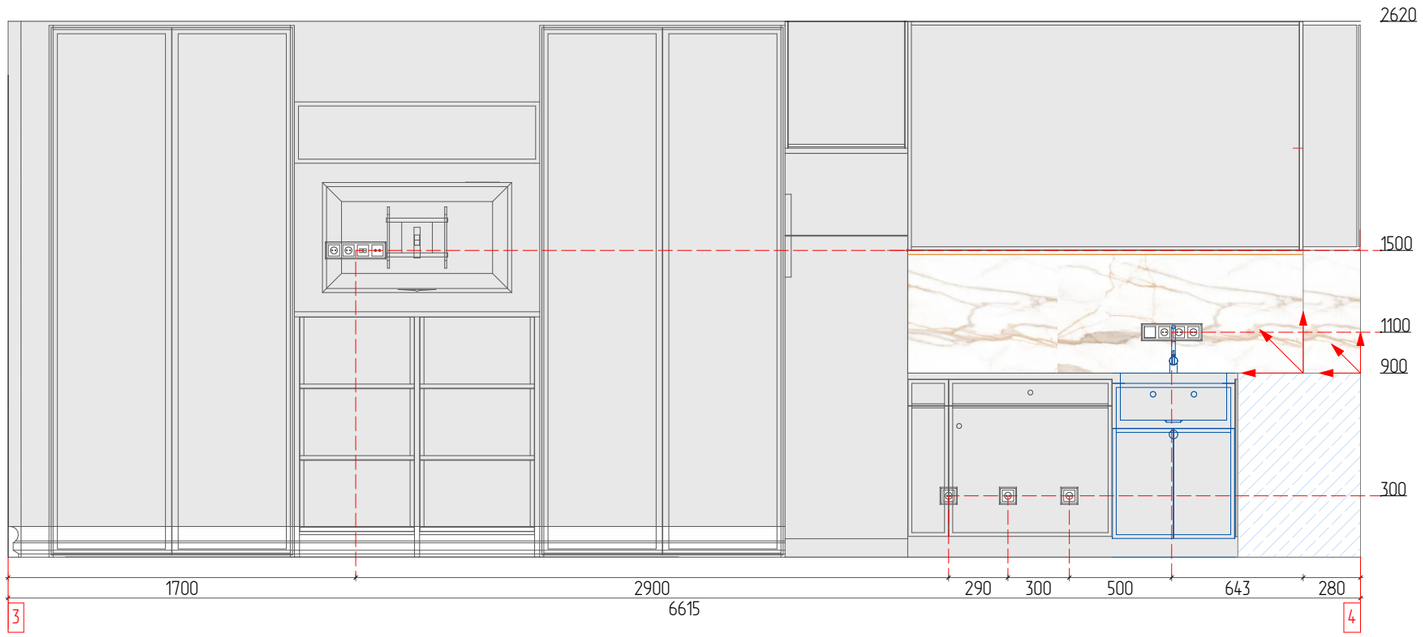

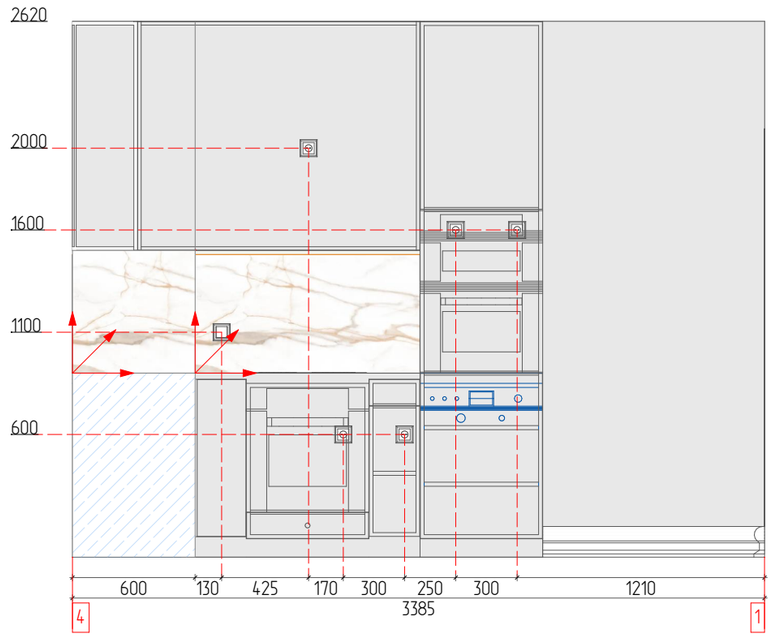

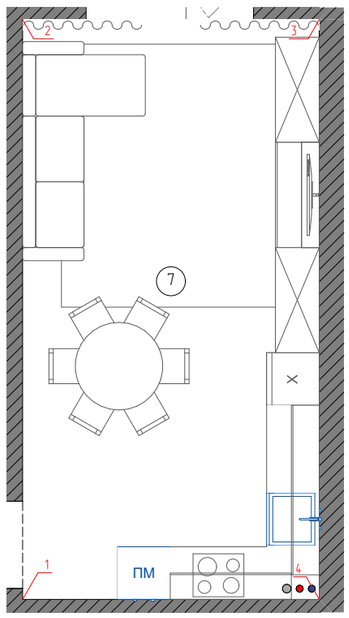


Расход материалов. Кухня-гостиная			
Наименование	Условное обозначение	Площадь, кв.м (без запаса)	Примечание
Глазурованный керамогранит Ceradim Calacatta Goddes 120x60		2,35	89353837 (lemanapro.ru)
Обои под покраску флизелиновые антивандальные Erismann Defender Рогожка белые		44,31	89364431 (lemanapro.ru)
Обои флизелиновые Erismann Anny бежевые		44,31	84774830 (lemanapro.ru)


Примечание:

1. Количество материала для отделки стен дано без запаса.
2. Пересчитать все материалы перед заказом с менеджером бренда (используя данные проекта).
3. Размеры и описание изделий по индивидуальным заказам смотреть на соответствующих листах проекта.
4. Обои даны на выбор, один из таблицы материалов.


Дизайнер	Екатерина Шинкевич	Дизайн-проект квартиры по адресу:	Развертки по стенам. Кухня-гостиная	Стадия	Лист	Листов
				РП	24	26
Телефон	+7 (931) 271-59-56	адрес	Масштаб 1:70, 1:30	SHEM		

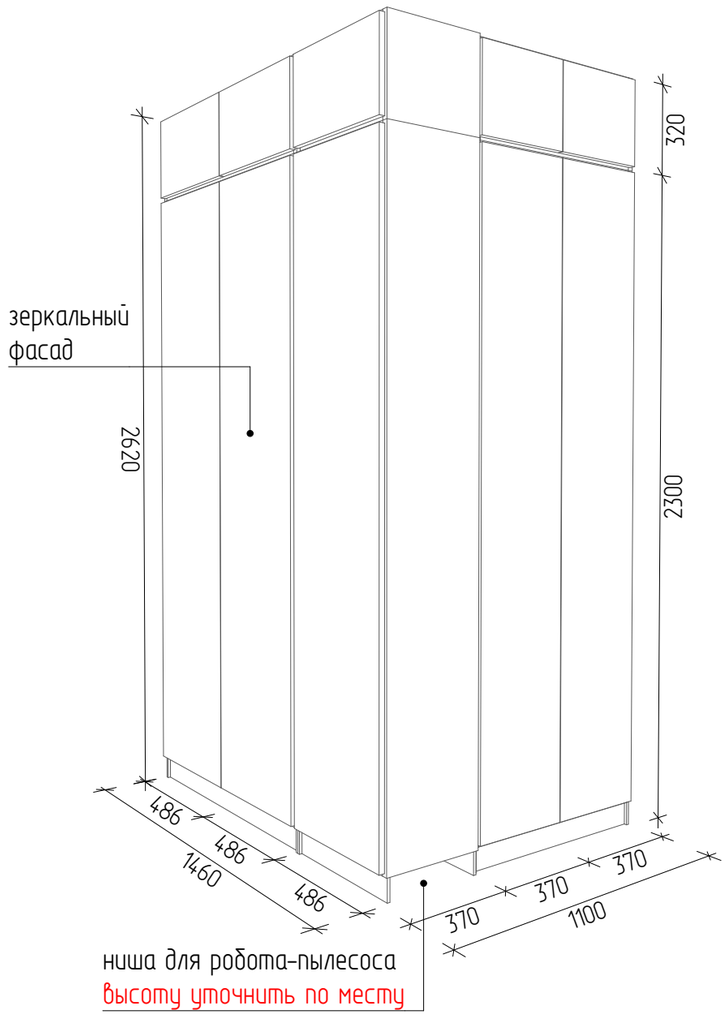


Тип мебели: шкаф
Местоположение: прихожая
Материал: МДФ, цвет белый

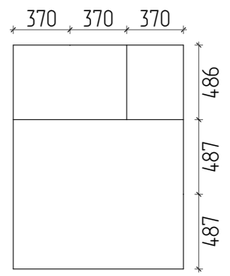


Вид сверху
распределение хранения
в верхних отсеках

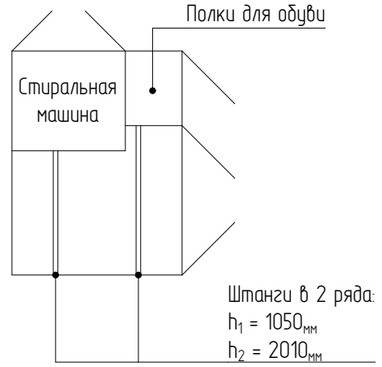

Вид сверху
открывание дверок

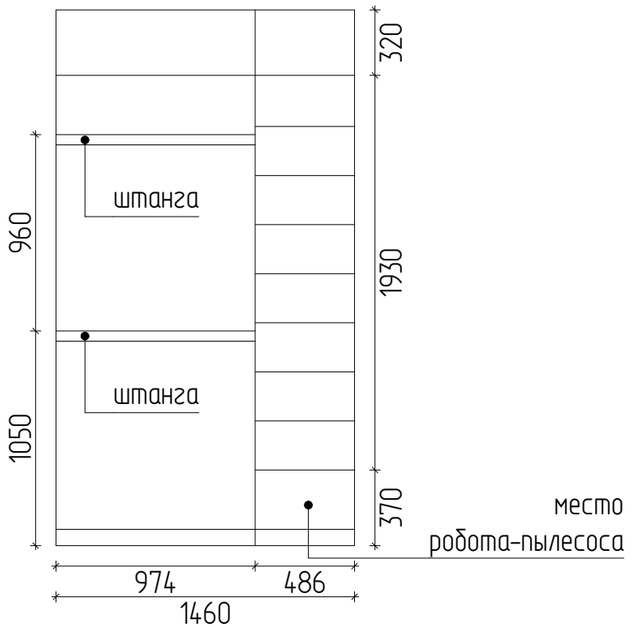

Вид слева
наполнение шкафа

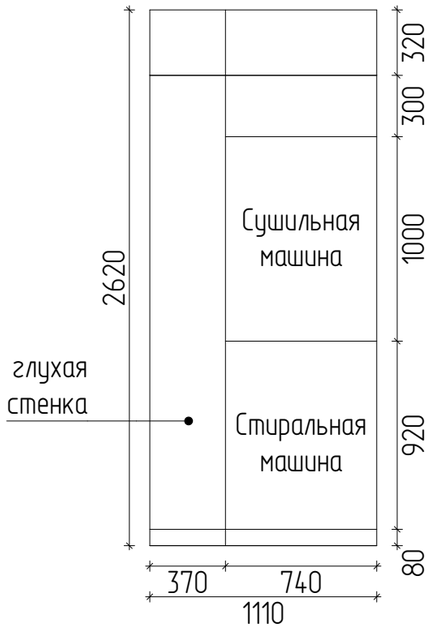


Вид справа
наполнение шкафа

Примечание:


1. Точные размеры всех изделий по индивидуальным заказам уточняются по факту специалистом-исполнителем.
2. Мебельные ручки выбираются совместно с дизайнером.

Дизайнер	Екатерина Шинкевич	Дизайн-проект квартиры по адресу:	Мебель на заказ	Стадия	Лист	Листов
				РП	30	26
Телефон	+7 (931) 271-59-56	адрес	Масштаб 1:200, 1:40, 1:30	SHEM		

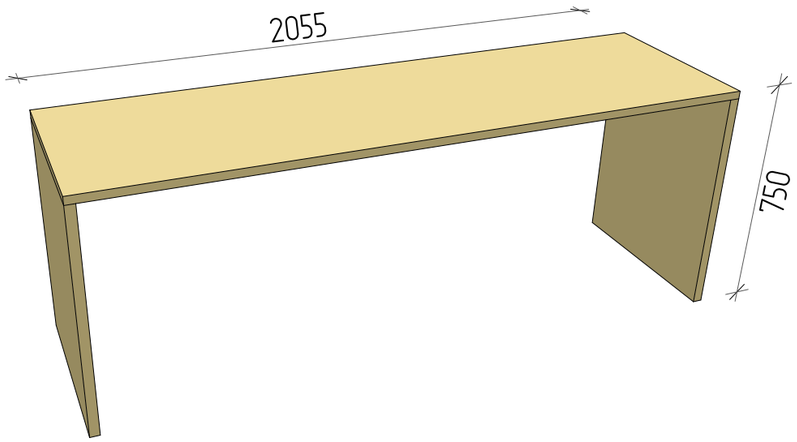




Тип мебели: стол
Местоположение: детская мальчики
Материал: Мебельная деталь ЛДСП Egger H1277ST9 60x220x1.6 см сорт экстра цвет акация лэйклэнд светлая

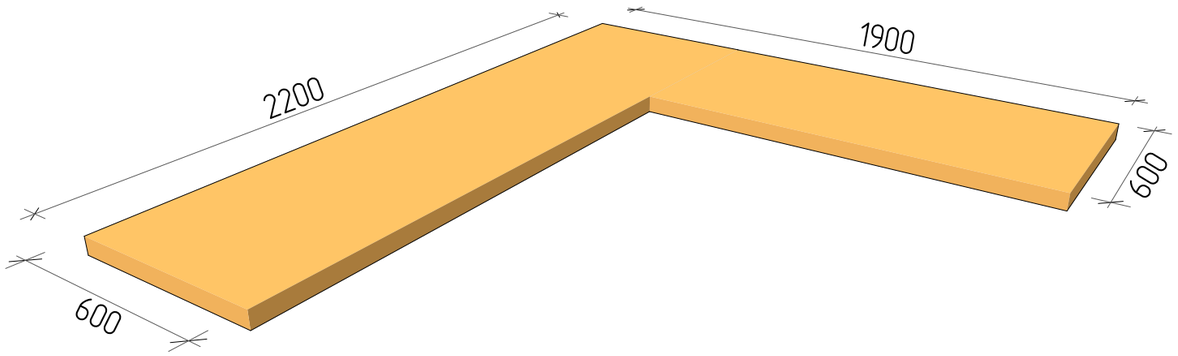

Тип мебели: столешница
Местоположение: детская девочки
Материал: Мебельная деталь ЛДСП Egger H1277ST9 60x220x1.6 см сорт экстра цвет акация лэйклэнд светлая
на 3 кронштейнах: у кровати, в углу, у шкафа

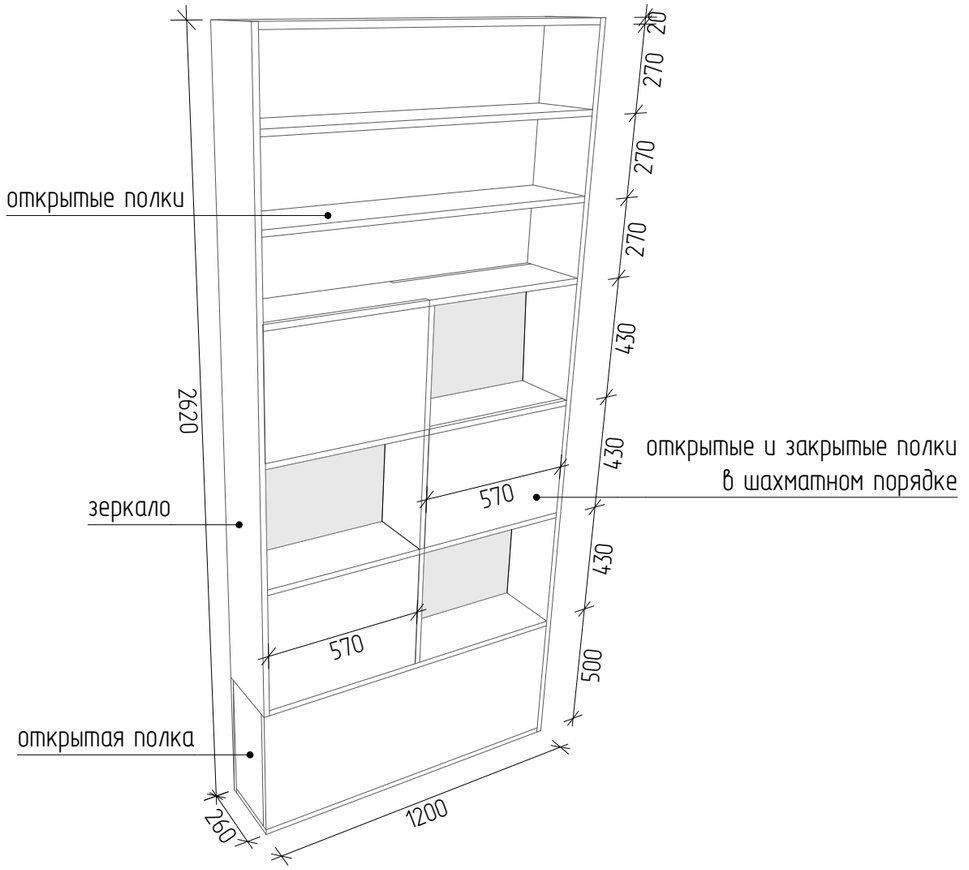


Тип мебели: стеллаж
Местоположение: детская девочки
Материал: МДФ, цвет белый

Примечание:

1. Точные размеры всех изделий по индивидуальным заказам уточняются по факту специалистом-исполнителем.
2. Мебельные ручки выбираются совместно с дизайнером.

Дизайнер	Екатерина Шинкевич	Дизайн-проект квартиры по адресу:	Мебель на заказ	Стадия	Лист	Листов
				РП	31	26
Телефон	+7 (931) 271-59-56	адрес	Масштаб 1:200, 1:100	SHEM		

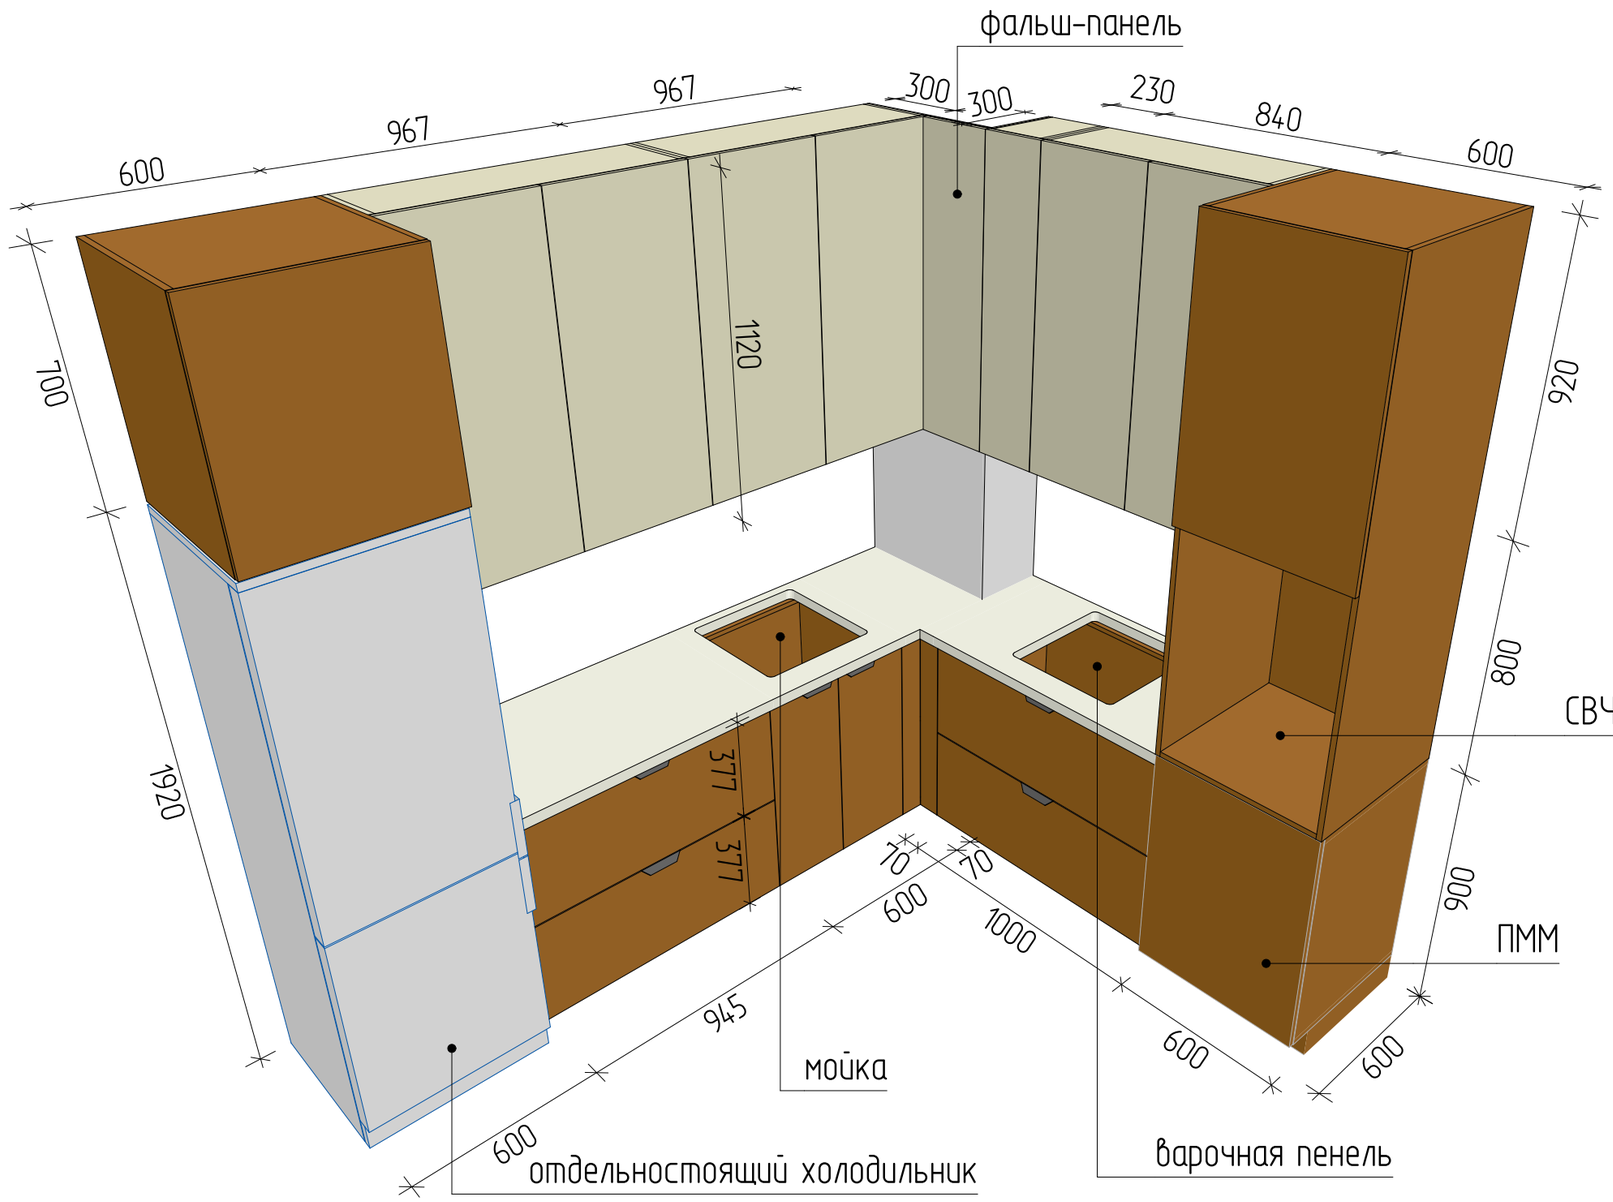




Мебельная ручка MONTE RT110BL.1/160/200

Столешница Diamant white 3497



Нижняя база и шкафы Фасад Original Фрезеровка «Билд»

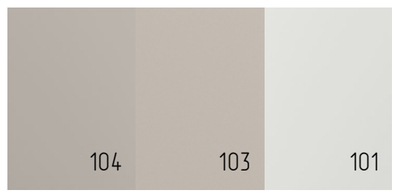

Нижняя база и шкафы Фасад Color Фрезеровка «Билд»





Фасад для СВЧ

Тип мебели: кухонный гарнитур
Местоположение: кухня-гостиная
Материалы:
нижняя база и шкафы: рекомендуемые цвета 531, 236
ручки нижняя база: MONTE RT110BL.1/160/200
верхняя база: рекомендуемые цвета 104, 103, 101
ручки верхняя база: без ручек, имеют свес $15_{мм}$ для открывания за фасад
столешница: Diamant white 3497

Примечание:
1. Точные размеры всех изделий по индивидуальным заказам уточняются по факту специалистом-исполнителем.
2. Мебельные ручки выбираются совместно с дизайнером.

Дизайнер	Екатерина Шинкевич	Дизайн-проект квартиры по адресу:	Мебель на заказ	Стадия	Лист	Листов
				РП	32	26
Телефон	+7 (931) 271-59-56	адрес		SHEM		

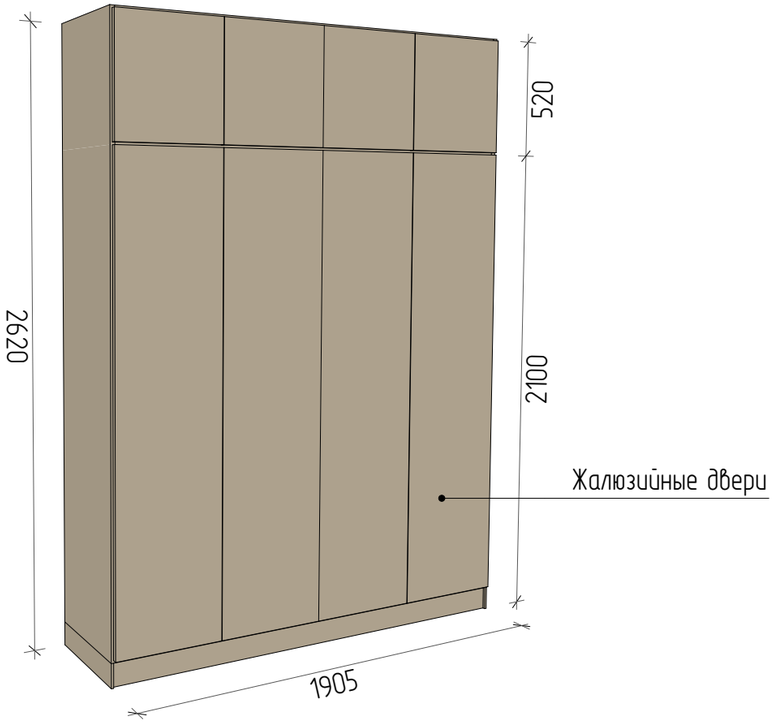

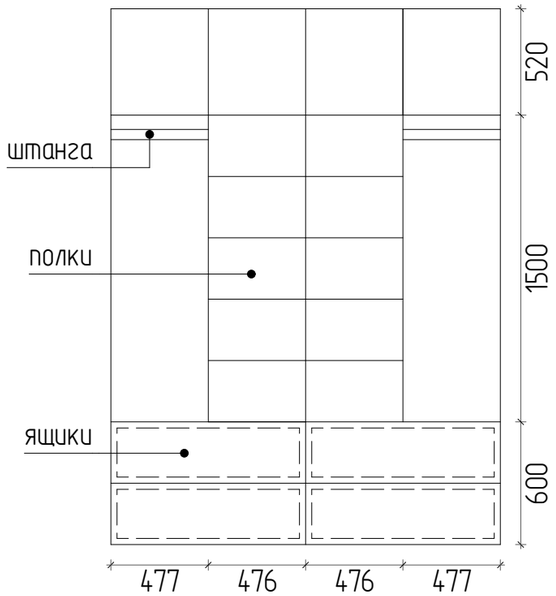

Внутреннее наполнение




Тип мебели: шкаф
Местоположение: спальня
Материалы: корпус лдсп под дерево, фасады жалюзи

Примечание:


1. Точные размеры всех изделий по индивидуальным заказам уточняются по факту специалистом-исполнителем.
2. Мебельные ручки выбираются совместно с дизайнером.

Дизайнер	Екатерина Шинкевич	Дизайн-проект квартиры по адресу:	Мебель на заказ	Стадия	Лист	Листов
				РП	33	26
Телефон	+7 (931) 271-59-56	адрес	Масштаб 1:200, 1:100, 1:30	SHEM		

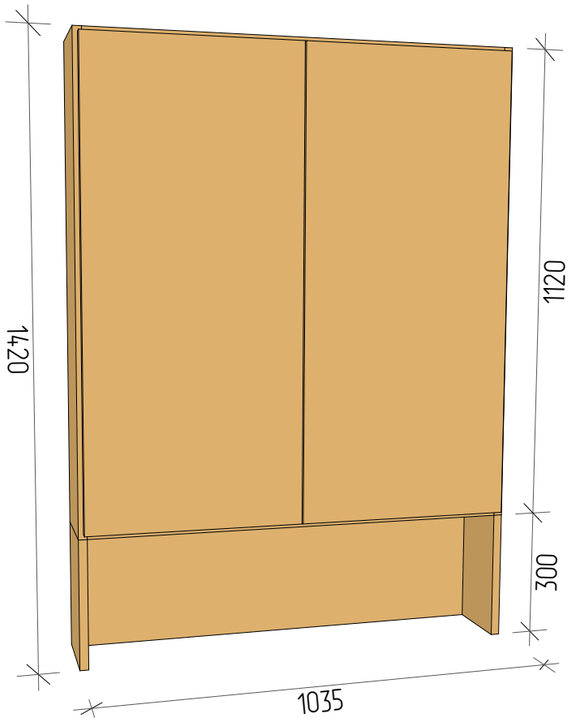

Тип мебели: шкаф над инсталляцией
Местоположение: ванная
Материалы: Деталь мебельная 1200х400х16 мм ЛДСП акация светлая кромка со всех сторон

открытие нажатием

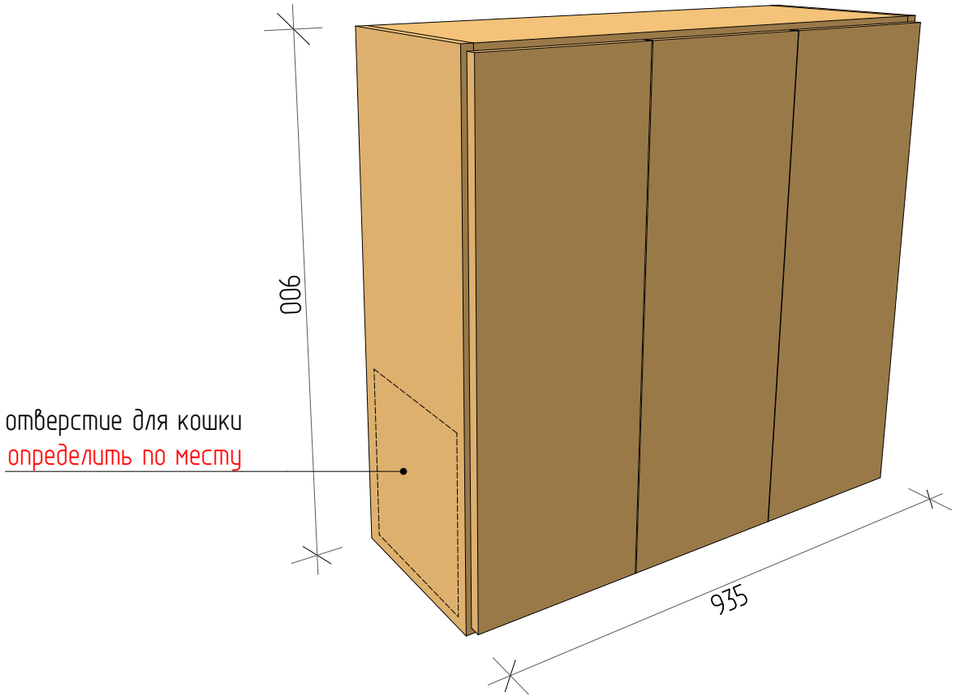



Тип мебели: шкафчик
Местоположение: ванная
Материалы: Деталь мебельная 1200х400х16 мм ЛДСП акация светлая кромка со всех сторон
дверцы купе






Примечание:

1. Точные размеры всех изделий по индивидуальным заказам уточняются по факту специалистом-исполнителем.
2. Мебельные ручки выбираются совместно с дизайнером.


Дизайнер	Екатерина Шинкевич	Дизайн-проект квартиры по адресу:	Мебель на заказ	Стадия	Лист	Листов
				РП	34	26
Телефон	+7 (931) 271-59-56	адрес	Масштаб 1:200	SHEM		

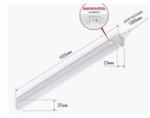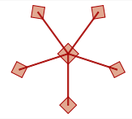Спецификация осветительного оборудования									
ID	Тип светильника	Производитель	Наименование	Артикул	Расположение	Мощность, Вт	Примечание	Изображение	Количество
C01	светильник потолочный	Feron	спот	553690572 (ozon.ru)	коридор, детская девочки	35	цвет: светло-серый		37
C02	светильник точечный встраиваемый	Voltega	Vgl004w	91692638 (lemanapro.ru)	санузел	50	цвет: белый		6
C03	бра настенный	Gala Premium Led	ночник	26607290 (wildberries.ru)	детская мальчики	-	цвет: белый		1
C04	лампа настольная	SVih	-	475371776 (ozon.ru)	детская девочки	60	цвет: белый		2
C05	настенный светильник	17Store	-	1009853363 (ozon.ru)	детская девочки	3	цвет: белый		2
C06	светильник линейный	IN HOME	светодиодный настенный	140360651 (wildberries.ru)	спальня	10	цвет: белый		1
C07	бра	THE MAGIC FIVE	-	139305452 (wildberries.ru)	спальня		цвет: белый		2
C08	подсветка ванной	Lightning Design	светильник для зеркала	13744450 (wildberries.ru)	ванная	-	цвет: белый		1
C09	напольный светильник	Ultra LIGHT	Торшер	202614496 (wildberries.ru)	кухня-гостиная	-	цвет: белый матовый		1
C10	люстра				кухня-гостиная		НЕ ВЫБРАНА		1

Дизайнер	Екатерина Шинкевич	Дизайн-проект квартиры по адресу:	Спецификация осветительного оборудования	Стадия	Лист	Листов
				РП	35	26
Телефон	+7 (931) 271-59-56	адрес		SHEM		

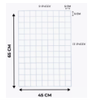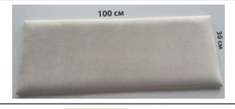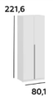Спецификация мебели							
Тип мебели	Производитель	Наименование	Артикул	Изображение	Кол-во	Расположение	Примечание
тумба под раковину	Айсберг	"Bazis 60" Ева	169776516 (wildberries.ru)		1	ванная	подвесная белая
полотенцесушитель	Арго	Классика Гранд	87049102 (lemanapro.ru)		1	ванная	электрический
люк ревизионный	Лючки рф	Секрет-3-0	90698737 (lemanapro.ru)		1	ванная	300х300 алюминий, цвет: серебристый
зеркальный шкаф	IKA	Адель 60	14504301 (wildberries.ru)		1	ванная	цвет: белый 600х160х750мм
органайзер	It's your TIME	настенный держатель	1416225588 (ozon.ru)		2	детская девочки	36х13см, 3 секции
органайзер настенный	House_Boutique	Мудборд	145939383 (wildberries.ru)		1	детская девочки	65х45см, цвет: белый
стеновая панель	Альтерия	мягкая	143409193 (wildberries.ru)		4	детская девочки	100х30см, цвет: бежевый
кровать	Эра Мебельное Производство	Односпальная	1524878568 (ozon.ru)		2	детская девочки	120х200см, цвет: белый
ковер	Sundelica	круглый комнатный	143752368 (wildberries.ru)		2	детская девочки	120х120
кресло	BYROOM	Office Fix grey	1404278314 (ozon.ru)		2	детская девочки	цвет: серый
пуф	Skavhome	Лимоны	1340626014 (ozon.ru)		1	детская девочки	рисунок: бабочки
тумба	МАЛЬТА	выкатная	1045490918 (ozon.ru)		2	детская девочки	40х45х60см, цвет: белый
стеллаж	LETTA	Монтессори	373097798 (ozon.ru)		2	детская девочки	цвет: бежевый
шкаф	НОНТОН	шкаф	1525526262 (ozon.ru)		1	детская девочки	цвет: белый


Дизайнер	Екатерина Шинкевич	Дизайн-проект квартиры по адресу:	Спецификация мебели	Стадия	Лист	Листов
Телефон	+7 (931) 271-59-56	адрес		РП	36	26

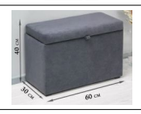Спецификация мебели							
Тип мебели	Производитель	Наименование	Артикул	Изображение	Кол-во	Расположение	Примечание
шкаф	НОНТОН	шкаф	1467806699 (ozon.ru)		1	детская девочки	цвет: белый
пуф	Remeco collection	Клетка	984275880 (ozon.ru)		1	детская мальчика	складной
ковер	Фабрика ковров Белка	пушистый комнатный	150839427 (wildberries.ru)		1	детская мальчика	160х230 с длинным ворсом
карта	WoodenCountry	Карта мира настенная из дерева	1166555271 (ozon.ru)		1	детская мальчика	цвет: сиена (русский язык)
шкаф	HomeGrad	Mika 1200	180620852 (wildberries.ru)		1	детская мальчики	цвет: белый
кресло-мешок	COOLPOUF	Груша	1579786164 (ozon.ru)		1	детская мальчики	размер: XXL, цвет:светло-бежевый
зеркало	Monro Mirror	интерьерное	965390351 (ozon.ru)		1	детская мальчики	цвет: серебристый, 50х150 см
корзина	LINGON	для игрушек	979639408 (ozon.ru)		1	детская мальчики	цвет: белый-песчаный
постер	Scanditone	Bonjour - Добрый день	1119616524 (ozon.ru)		1	детская мальчики	30х40 см
шведская стенка	Backwood	деревянная с турником	664750266 (ozon.ru)		1	детская мальчики	цвет: бежевый
детский стул	ДВИЖЕНИЕ - ЖИЗНЬ	Растущий стул	397280663 (ozon.ru)		1	детская мальчики	цвет: светло-серый, светло-бежевый
шкаф	ARNIKA	распашной	204113373 (wildberries.ru)		1	детская мальчики	цвет: белый
пуфик	Sofline	с ящиком мягкий прямоугольный	237369183 (wildberries.ru)		1	коридор	цвет: графит, темно-серый
полка	Мебельер	навесная настенная	153692012 (wildberries.ru)		4	кухня-гостиная	цвет: дуб ватан, коричневый • 2 шт в комплекте

Дизайнер	Екатерина Шинкевич	Дизайн-проект квартиры по адресу:	Спецификация мебели
Телефон	+7 (931) 271-59-56	адрес	


Стадия	Лист	Листов
РП	37	26

SHEM

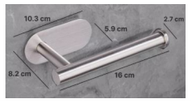Спецификация мебели							
Тип мебели	Производитель	Наименование	Артикул	Изображение	Кол-во	Расположение	Примечание
стул	Studioakd	мягкие со спинкой	207693753 (wildberries.ru)		6	кухня-гостиная	цвет: серый, пепел • 2 шт в комплекте
стол	МФ "Стендмебель"	Обеденный	226725034 (wildberries.ru)		1	кухня-гостиная	цвет: дуб крафт золотой, черный
ковер	KoverCity	-	1593333870 (ozon.ru)		1	кухня-гостиная	250х300см цвет: бежевый, кремовый
комод	LETTA	City Plus	104516126 (wildberries.ru)		1	кухня-гостиная	120х500х1200 см, цвет: белый
шкаф	HomeGrad	Boston	220256751 (wildberries.ru)		2	кухня-гостиная	120 см, цвет: белый
крючки	Дубовый двор	Настенные деревянные	94517005 (wildberries.ru)		3	прихожая	цвет: коричневый • 4 шт
шкаф	Keo	пенал	163698413 (wildberries.ru)		1	санузел	цвет: мягкий белый
полотенцесушитель	Арго Орион	Орион	87823496 (lemanapro.ru)		1	санузел	электрический
держатель для туалетной бумаги	MOKKI`	самоклеящийся без сверления	172347231 (wildberries.ru)		1	санузел	цвет: серебристый, хром, сталь
тумба под раковину	kaksa	Енисей Como "UNO 60"	168919581 (wildberries.ru)		1	санузел	подвесная белая
люк ревизионный	Evecs	PUSH L4040N	91469643 (arkhangelsk.lemanapro.ru)		1	санузел	цвет: белый
ёршик для унитаза	LY design	подвесной настенный	141035706 (wildberries.ru)		1	санузел	цвет: хром матовый
кресло	Rifforma	Компьютерное офисное	183628291 (wildberries.ru)		1	спальня	цвет: светло-бежевый
зеркало	МебельСтиль	-	219502901 (wildberries.ru)		1	спальня	цвет: белый, белый шагрень

Дизайнер	Екатерина Шинкевич	Дизайн-проект квартиры по адресу:	Спецификация мебели	Стадия	Лист	Листов
Телефон	+7 (931) 271-59-56	адрес		РП	38	26

SHEM

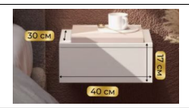Спецификация мебели							
Тип мебели	Производитель	Наименование	Артикул	Изображение	Кол-во	Расположение	Примечание
пенал	-	навесной	136589199 (wildberries.ru)		1	спальня	цвет: белый
ковровое покрытие	Зартекс	Глория	89334422 (lemanapro.ru)		1	спальня	цвет: светло-оливковый
тумба	МК Мебель	Прикроватная подвесная	224920360 (wildberries.ru)		2	спальня	цвет: белый, белый шагрень
стол	ГайваМебель	ОСКАР	600824066 (ozon.ru)		1	спальня	100х50х75см, цвет:белый
кровать	sleep and smile	двуспальная деревянная	181200566 (wildberries.ru)		1	спальня	цвет: белый • 160х200 см

Дизайнер	Екатерина Шинкевич	Дизайн-проект квартиры по адресу:	Спецификация мебели	Стадия	Лист	Листов
				РП	39	26
Телефон	+7 (931) 271-59-56	адрес		SHEM		

Спецификация сантехнического оборудования						
Тип сантехнического оборудования	Производитель	Наименование	Изображение	Количество	Расположение	Примечание
душевой комплект	Agger	Right Right		1	ванная	верхний душ / душевая стойка / смеситель для ванны с душем
смеситель	San's	для раковины		1	ванная	цвет: сатиновый, нержавеющая сталь, металл • сталь
раковина	Cersanit	MODUO		1	ванная	цвет: белый
ванна		Нирвана		1	ванная	170х75 см акрил
инсталляция	WeltWasser	Комплект 381 с подвесным унитазом		2	ванная, санузел	модель продукта Telbach
смеситель для кухни	Domaci	Ливорно		1	кухня-гостиная	цвет: черный
смеситель	Bach	для раковины		1	санузел	цвет: серый, сатиновый • нержавеющая сталь
раковина	kaksa	Енисей 60		1	санузел	цвет: белый
гиг.душ	Haiba	HB01		2	санузел	цвет: хром

Примечание:

1. Окончательный выбор и возможность монтажа сантехнического оборудования согласовать со специалистом сантехником.
2. Проверить совместимость смесителей с раковиной до момента покупки.

Дизайнер	Екатерина Шинкевич	Дизайн-проект квартиры по адресу:	Спецификация сантехнического оборудования	Стадия	Лист	Листов
				РП	40	26
Телефон	+7 (931) 271-59-56	адрес		SHEM		

Спецификация отделочных материалов стен		
Наименование	Площадь, кв.м (без запаса)	Примечание
Глазурованный керамогранит Ceradim Calacatta Goddes 120x60	2,35	89353837 (lemanapro.ru)
Краска Tikkurila	13,18	TVT F 456, TVT F 457, TVT Y 456, TVT F 395, TVT F 396
Обои виниловые	19,45	215233958 (wildberries.ru)
Обои клетка виниловые	8,92	198706209 (wildberries.ru)
Обои метровые виниловые	11,21	167532794 (wildberries.ru)
Обои под покраску флизелиновые антивандальные Erismann Defender Рогожка белые	73,09	89364431 (lemanapro.ru)
Обои серо-бежевые	33,86	
Обои серые однотонные Textile (Moda Interio)	24,08	1410720452 (ozon.ru)
Обои флизелиновые Erismann Anny бежевые	73,09	84774830 (lemanapro.ru)
Плитка настенная Azori Forest	2,18	матовая цвет коричневое дерево 31.5x63 см
Плитка настенная Kerama Marazzi Монпарнас	10,47	

Спецификация полов/потолков			
ID	Наименование	S нетто, кв.м (без запаса)	Примечание
01	Натяжной потолок	75,05	
02	штукатурка + покраска	1,37	
п01	Каменный ламинат SPC BETTA CHALET A808 МОРЗИН	72,24	
п02	Глазурованный керамогранит Ceramente Stellare Cement Pro 60x60см матовый цвет светло-серый	1,60	
п03	Глазурованный керамогранит Estima Jam JA01 40.5x40.5см неполированный цвет бежевый/зеленый с принтом	3,72	

Спецификация карнизов/молдингов/плинтусов				
ID	Наименование	Производитель	Длина, мм	Примечание
Пл01	Плинтус	Quadro	59221	h = 80мм

Дизайнер	Екатерина Шинкевич	Дизайн-проект квартиры по адресу:	Спецификация отделочных материалов	Стадия	Лист	Листов
				РП	41	26
Телефон	+7 (931) 271-59-56	адрес		SHEM		